



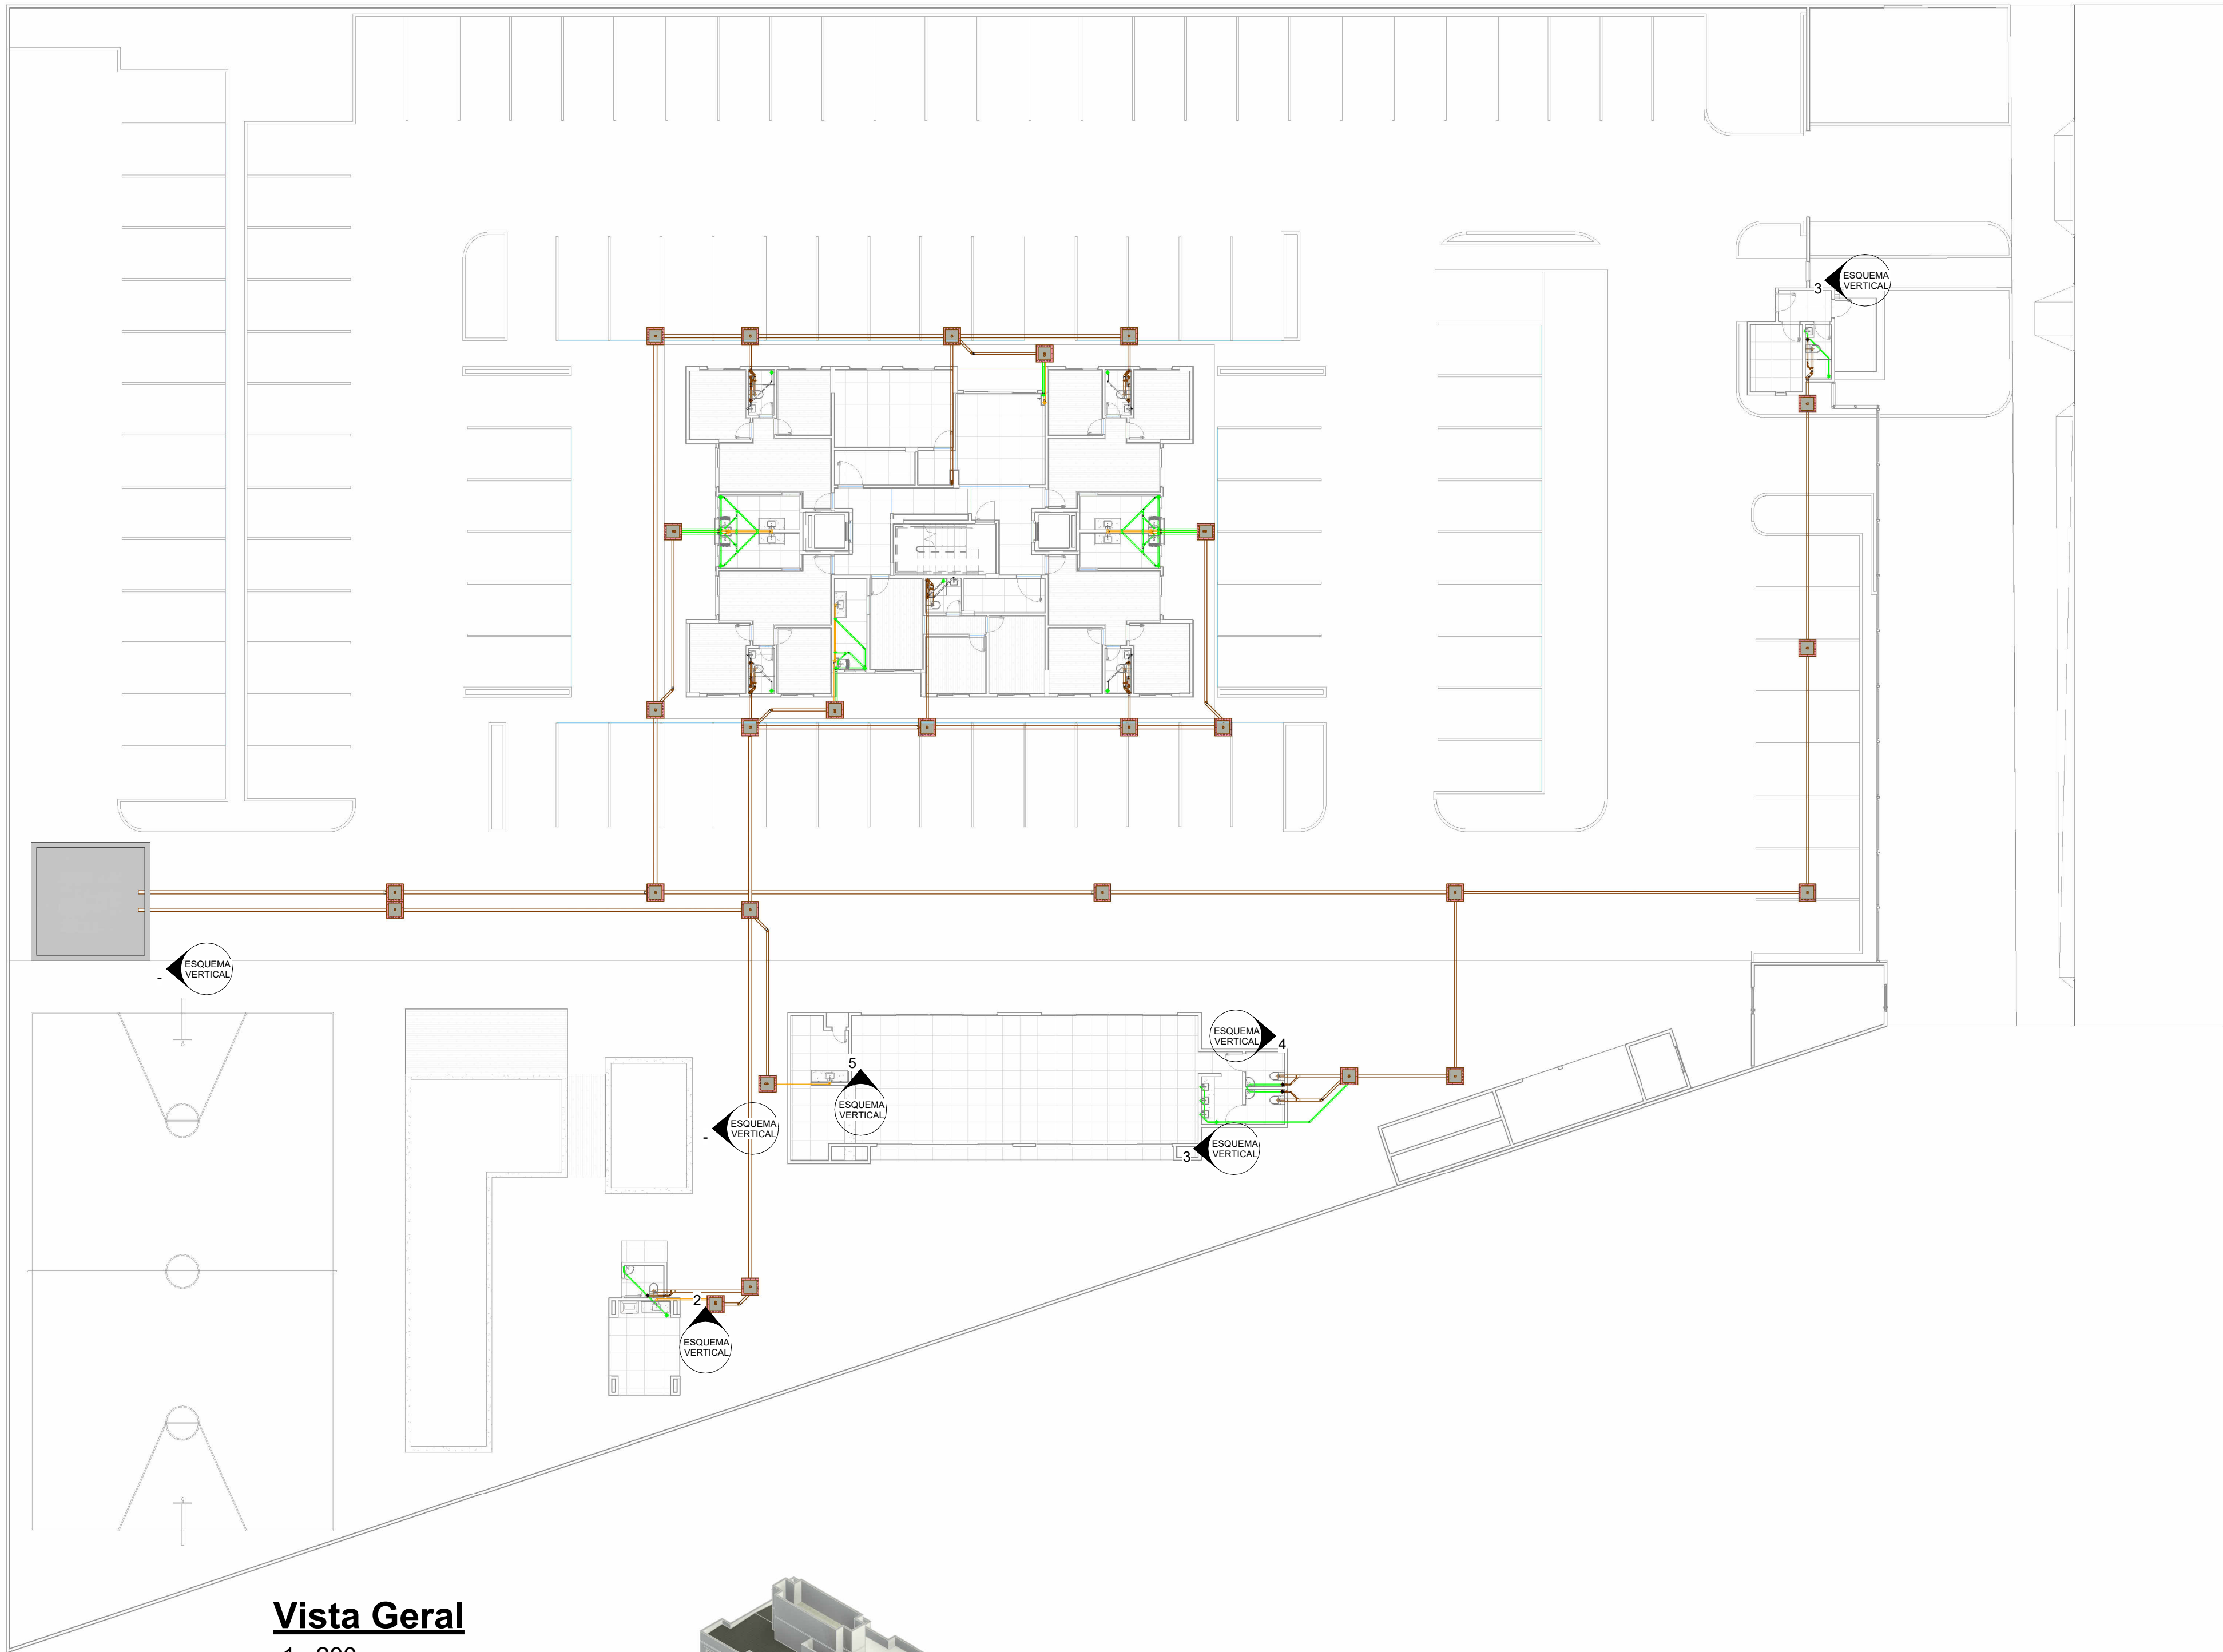

Vista Geral
1 : 200

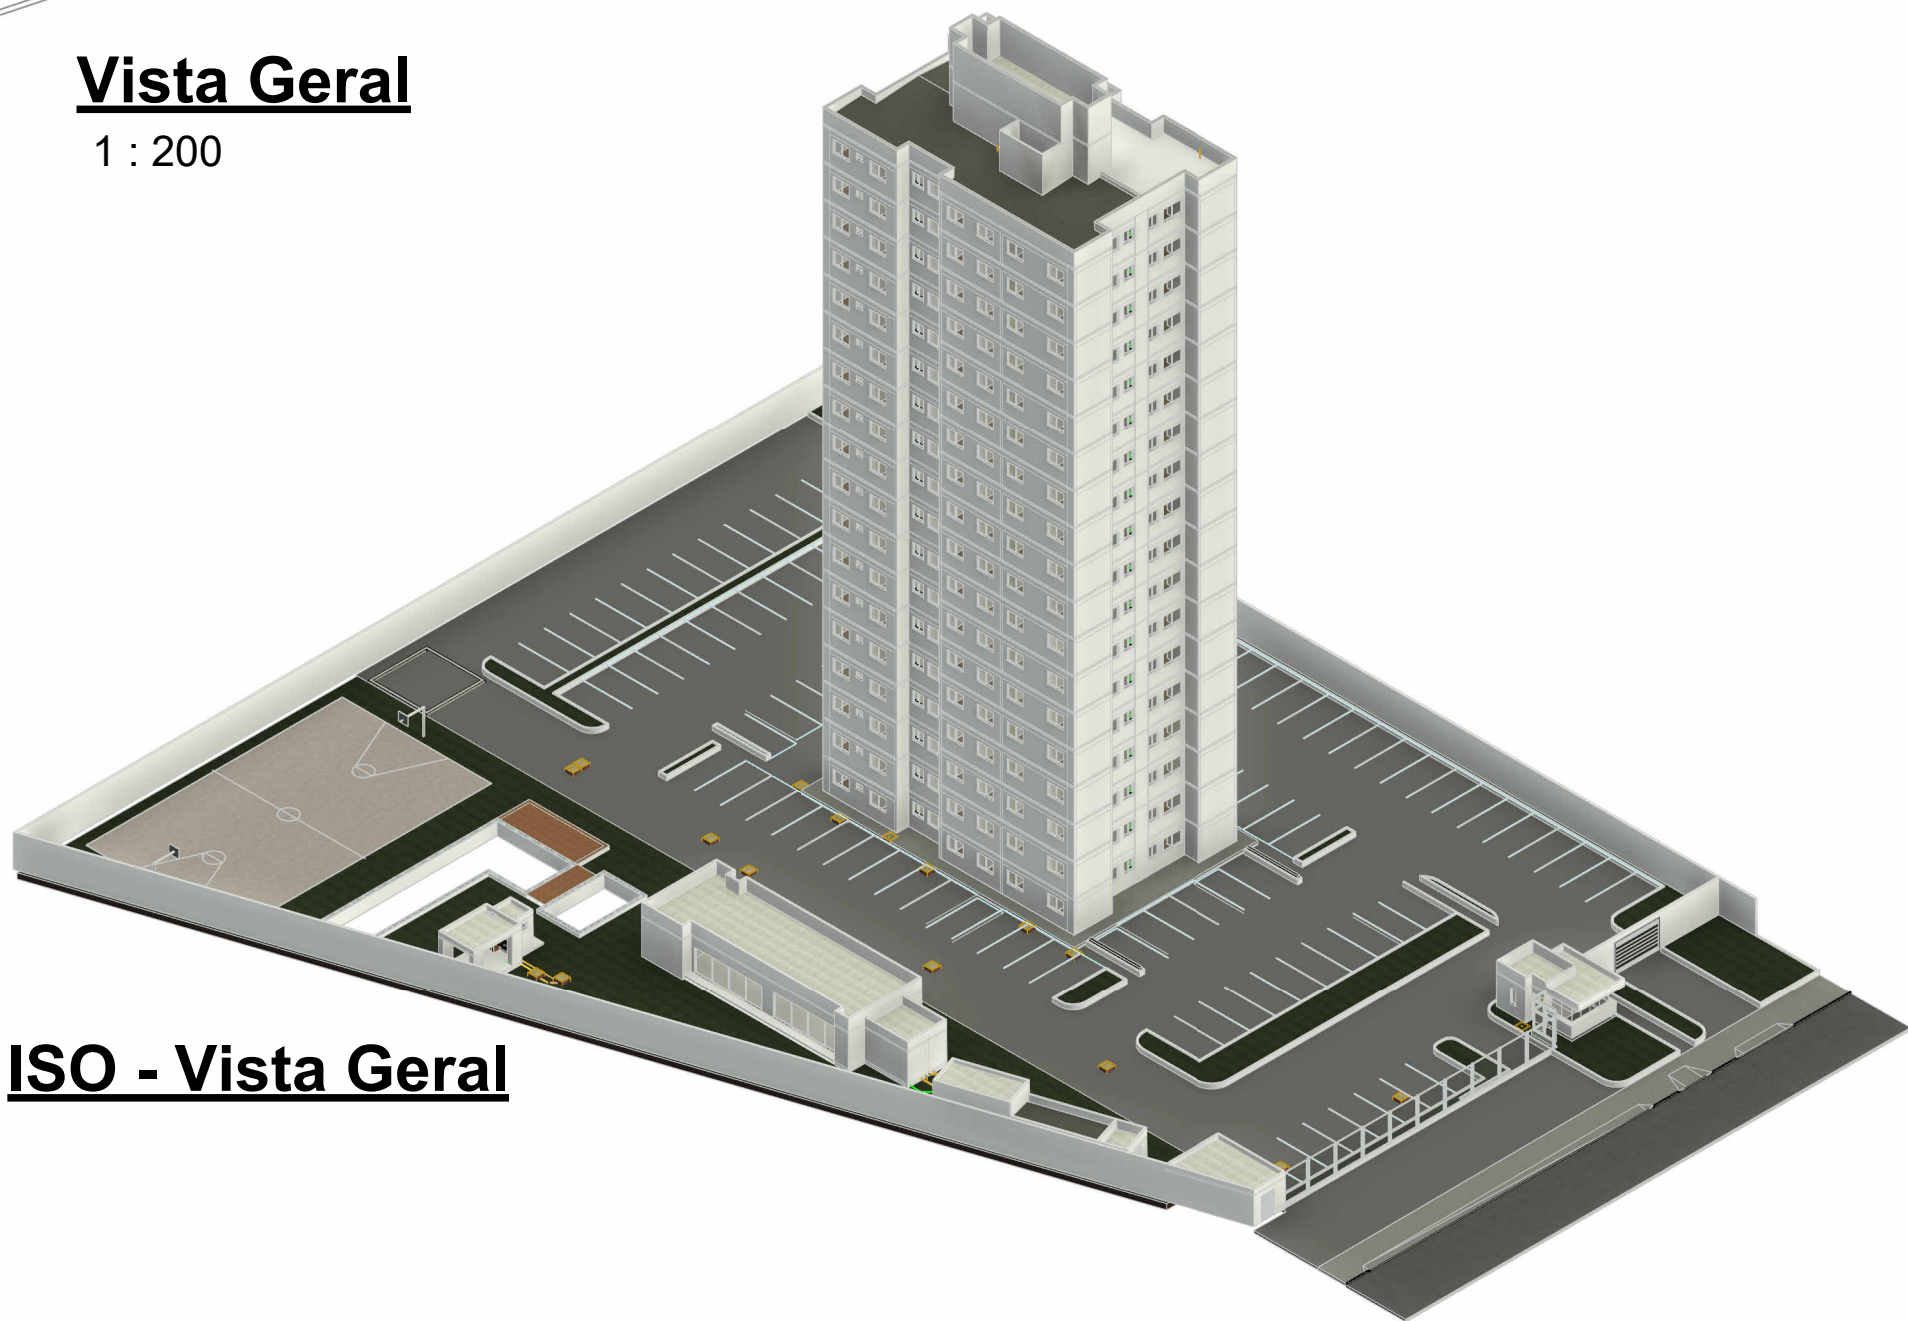

ISO - Vista Geral

LEGENDA:

- TUBULAÇÃO PVC BRANCO SN - ESGOTO PRIMÁRIO
- TUBULAÇÃO PVC BRANCO SN - ESGOTO SECUNDÁRIO
- TUBULAÇÃO PVC BRANCO SN - VENTILAÇÃO ESGOTO
- TUBULAÇÃO PVC BRANCO SN - ESGOTO COM GORDURA
- TUBO DE QUEDA DE ESGOTO PRIMÁRIO
- COLUNA DE VENTILAÇÃO
- TUBO DE QUEDA DE GORDURA
- POSIÇÃO DO ITEM NA LISTA DE MATERIAIS

ABREVIACOES:

- BS - BACIA SANITÁRIA
- LV - LAVATÓRIO
- CH - CHUVEIRO
- TN - TANQUE
- MLR - MÁQUINA DE LAVAR ROUPAS
- MLL - MÁQUINA DE LAVAR LOUÇAS
- DU - DUCHA HIGIÊNICA
- CS - CAIXA SIFONADA
- RS - RALO SECO
- CGP - CAIXA DE GORDURA PEQUENA
- CI - CAIXA DE INSPEÇÃO

NOTAS:


- DIMENSÕES E DIÂMETROS EM MILÍMETROS, EXCETO ONDE INDICADO CONTRÁRIO.
- NOS TRECHOS HORIZONTAIS DAS TUBULAÇÕES DE ESGOTO SANITÁRIO RECOMENDAM-SE AS SEGUINTE DECLIVIDADES MÍNIMAS:
 - 2% PARA TUBULAÇÕES COM DIÂMETRO NOMINAL IGUAL OU INFERIOR A 75mm;
 - 1% PARA TUBULAÇÕES COM DIÂMETRO NOMINAL IGUAL OU SUPERIOR A 100mm.
- UTILIZAR ANÉIS DE BORRACHA NAS CONEXÕES DE ESGOTO.
- PROIBIDO UTILIZAR FOGO NAS TUBULAÇÕES.
- OS TERMINAIS DE VENTILAÇÃO DOS TUBOS DE VENTILAÇÃO DEVERÃO PASSAR 30CM ACIMA DO TELHADO.
- UTILIZAR DISPOSITIVO ANTI-ESPUMA NA CAIXA SIFONADA DA ÁREA DE SERVIÇO.
- TODAS AS TUBULAÇÕES EXPOSTAS DEVERÃO SER FIXADAS COM BRAÇADEIRA

Lista de Materiais - Conexões e Acessórios	
Descrição do Material	Quantidade
	de
	1702
Adaptador para Saída de Vaso Sanitário, DN100mm, de PVC Rígido Branco Série Normal, conforme NBR 5688	146
Anel de Borracha, DN50mm, para linha de PVC Rígido Branco Série Normal, conforme NBR 5688	3613
Anel de Borracha, DN75mm, para linha de PVC Rígido Branco Série Normal, conforme NBR 5688	265
Anel de Borracha, DN100mm, para linha de PVC Rígido Branco Série Normal, conforme NBR 5688	1358
Anel de Borracha, DN150mm, para linha de PVC Rígido Branco Série Normal, conforme NBR 5688	5
Antespuma para instalação em Caixa Sifonada DN100mm, Esgoto	107
Bucha de Redução, DN50x40mm, de PVC Rígido Branco Série Normal para Esgoto e Água Pluvial, conforme NBR 5688	214
Caixa de inspeção em alvenaria com tampa de concreto, 60x60cm	27
Caixa Sifonada Girafácil Montada com Greiha e Porta Greiha Quadrados Brancos 100x140x50mm, 5 Entradas, Esgoto	219
INEXISTENTE	5
Joelho 45°, DN40mm, de PVC Rígido Branco Série Normal, conforme NBR 5688	294
Joelho 45°, DN50mm, de PVC Rígido Branco Série Normal, conforme NBR 5688	361
Joelho 45°, DN75mm, de PVC Rígido Branco Série Normal, conforme NBR 5688	11
Joelho 45°, DN100mm, de PVC Rígido Branco Série Normal, conforme NBR 5688	115
Joelho 90° com anel, DN40mm, de PVC Rígido Branco Série Normal, conforme NBR 5688	221
Joelho 90°, DN40mm, de PVC Rígido Branco Série Normal, conforme NBR 5688	221
Joelho 90°, DN50mm, de PVC Rígido Branco Série Normal, conforme NBR 5688	652
Joelho 90°, DN75mm, de PVC Rígido Branco Série Normal, conforme NBR 5688	4
Joelho 90°, DN100mm, de PVC Rígido Branco Série Normal, conforme NBR 5688	133
Junção 45° de Redução, DN75x50mm, de PVC Rígido Branco Série Normal, conforme NBR 5688	102
Junção 45° de Redução, DN100x50mm, de PVC Rígido Branco Série Normal, conforme NBR 5688	111
Junção 45°, DN40x40mm, de PVC Rígido Branco Série Normal, conforme NBR 5688	2
Junção 45°, DN50x50mm, de PVC Rígido Branco Série Normal, conforme NBR 5688	179
Junção 45°, DN75x75mm, de PVC Rígido Branco Série Normal, conforme NBR 5688	1374
Luva Simples, DN50mm, de PVC Rígido Branco Série Normal, conforme NBR 5688	1374
Luva Simples, DN75mm, de PVC Rígido Branco Série Normal, conforme NBR 5688	130
Luva Simples, DN100mm, de PVC Rígido Branco Série Normal, conforme NBR 5688	578
Luva Simples, DN150mm, de PVC Rígido Branco Série Normal, conforme NBR 5688	5
Ralo Seco Montado com Greiha e Porta Greiha Quadrados 100x100x40mm, Esgoto	109
Redução Excêntrica, DN75x50mm, de PVC Rígido Branco Série Normal para Esgoto e Água Pluvial, conforme NBR 5688	4
Redução Excêntrica, DN100x50mm, de PVC Rígido Branco Série Normal para Esgoto e Água Pluvial, conforme NBR 5688	8
Redução Excêntrica, DN100x75mm, de PVC Rígido Branco Série Normal para Esgoto e Água Pluvial, conforme NBR 5688	6
Redução Excêntrica, DN150x100mm, de PVC Rígido Branco Série Normal para Esgoto e Água Pluvial, conforme NBR 5688	5
Terminal de Ventilação, DN50mm, de PVC Rígido Branco Série Normal, conforme NBR 5688	4
Terminal de Ventilação, DN75mm, de PVC Rígido Branco Série Normal, conforme NBR 5688	6
Tê 90° de Redução, DN100x50mm, de PVC Rígido Branco Série Normal, conforme NBR 5688	202
Tê 90°, DN50x50mm, de PVC Rígido Branco Série Normal, conforme NBR 5688	111
Tê 90°, DN100x100mm, de PVC Rígido Branco Série Normal, conforme NBR 5688	107
Esgoto Sanitário	
Anel de Borracha, DN100mm, para linha de PVC Rígido Branco Série Normal, conforme NBR 5688	18
Luva Simples, DN100mm, de PVC Rígido Branco Série Normal, conforme NBR 5688	6
Tê 90°, DN100x100mm, de PVC Rígido Branco Série Normal, conforme NBR 5688	6


Lista de Materiais - Tubos		
Descrição do Material	Diâmetro Nominal (mm)	Comprimento (m)
Tubo de PVC Rígido Branco, conforme NBR5688, Linha Série Normal	Ø150	192,15
Tubo de PVC Rígido Branco, conforme NBR5688, Linha Série Normal	Ø100	1312,88
Tubo de PVC Rígido Branco, conforme NBR5688, Linha Série Normal	Ø75	350,21
Tubo de PVC Rígido Branco, conforme NBR5688, Linha Série Normal	Ø50	1321,86
Tubo de PVC Rígido Branco, conforme NBR5688, Linha Série Normal	Ø40	471,46



PENN & WIZE
INSTALAÇÕES PREDIAIS
<https://pennwize.github.io/>

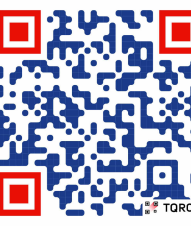


PROJETO:	Edifício Derry and George	FOLHA:	E00
LOCAL:	Rua dos bobos, nº 0. Natal/RN - Brasil	REV.:	
ASSUNTO:	Geral	ESCALA:	Como indicada
AUTORES DO PROJETO:	Amanda João Pedro Melo e Letícia Tórres	DATA:	12/02/2026

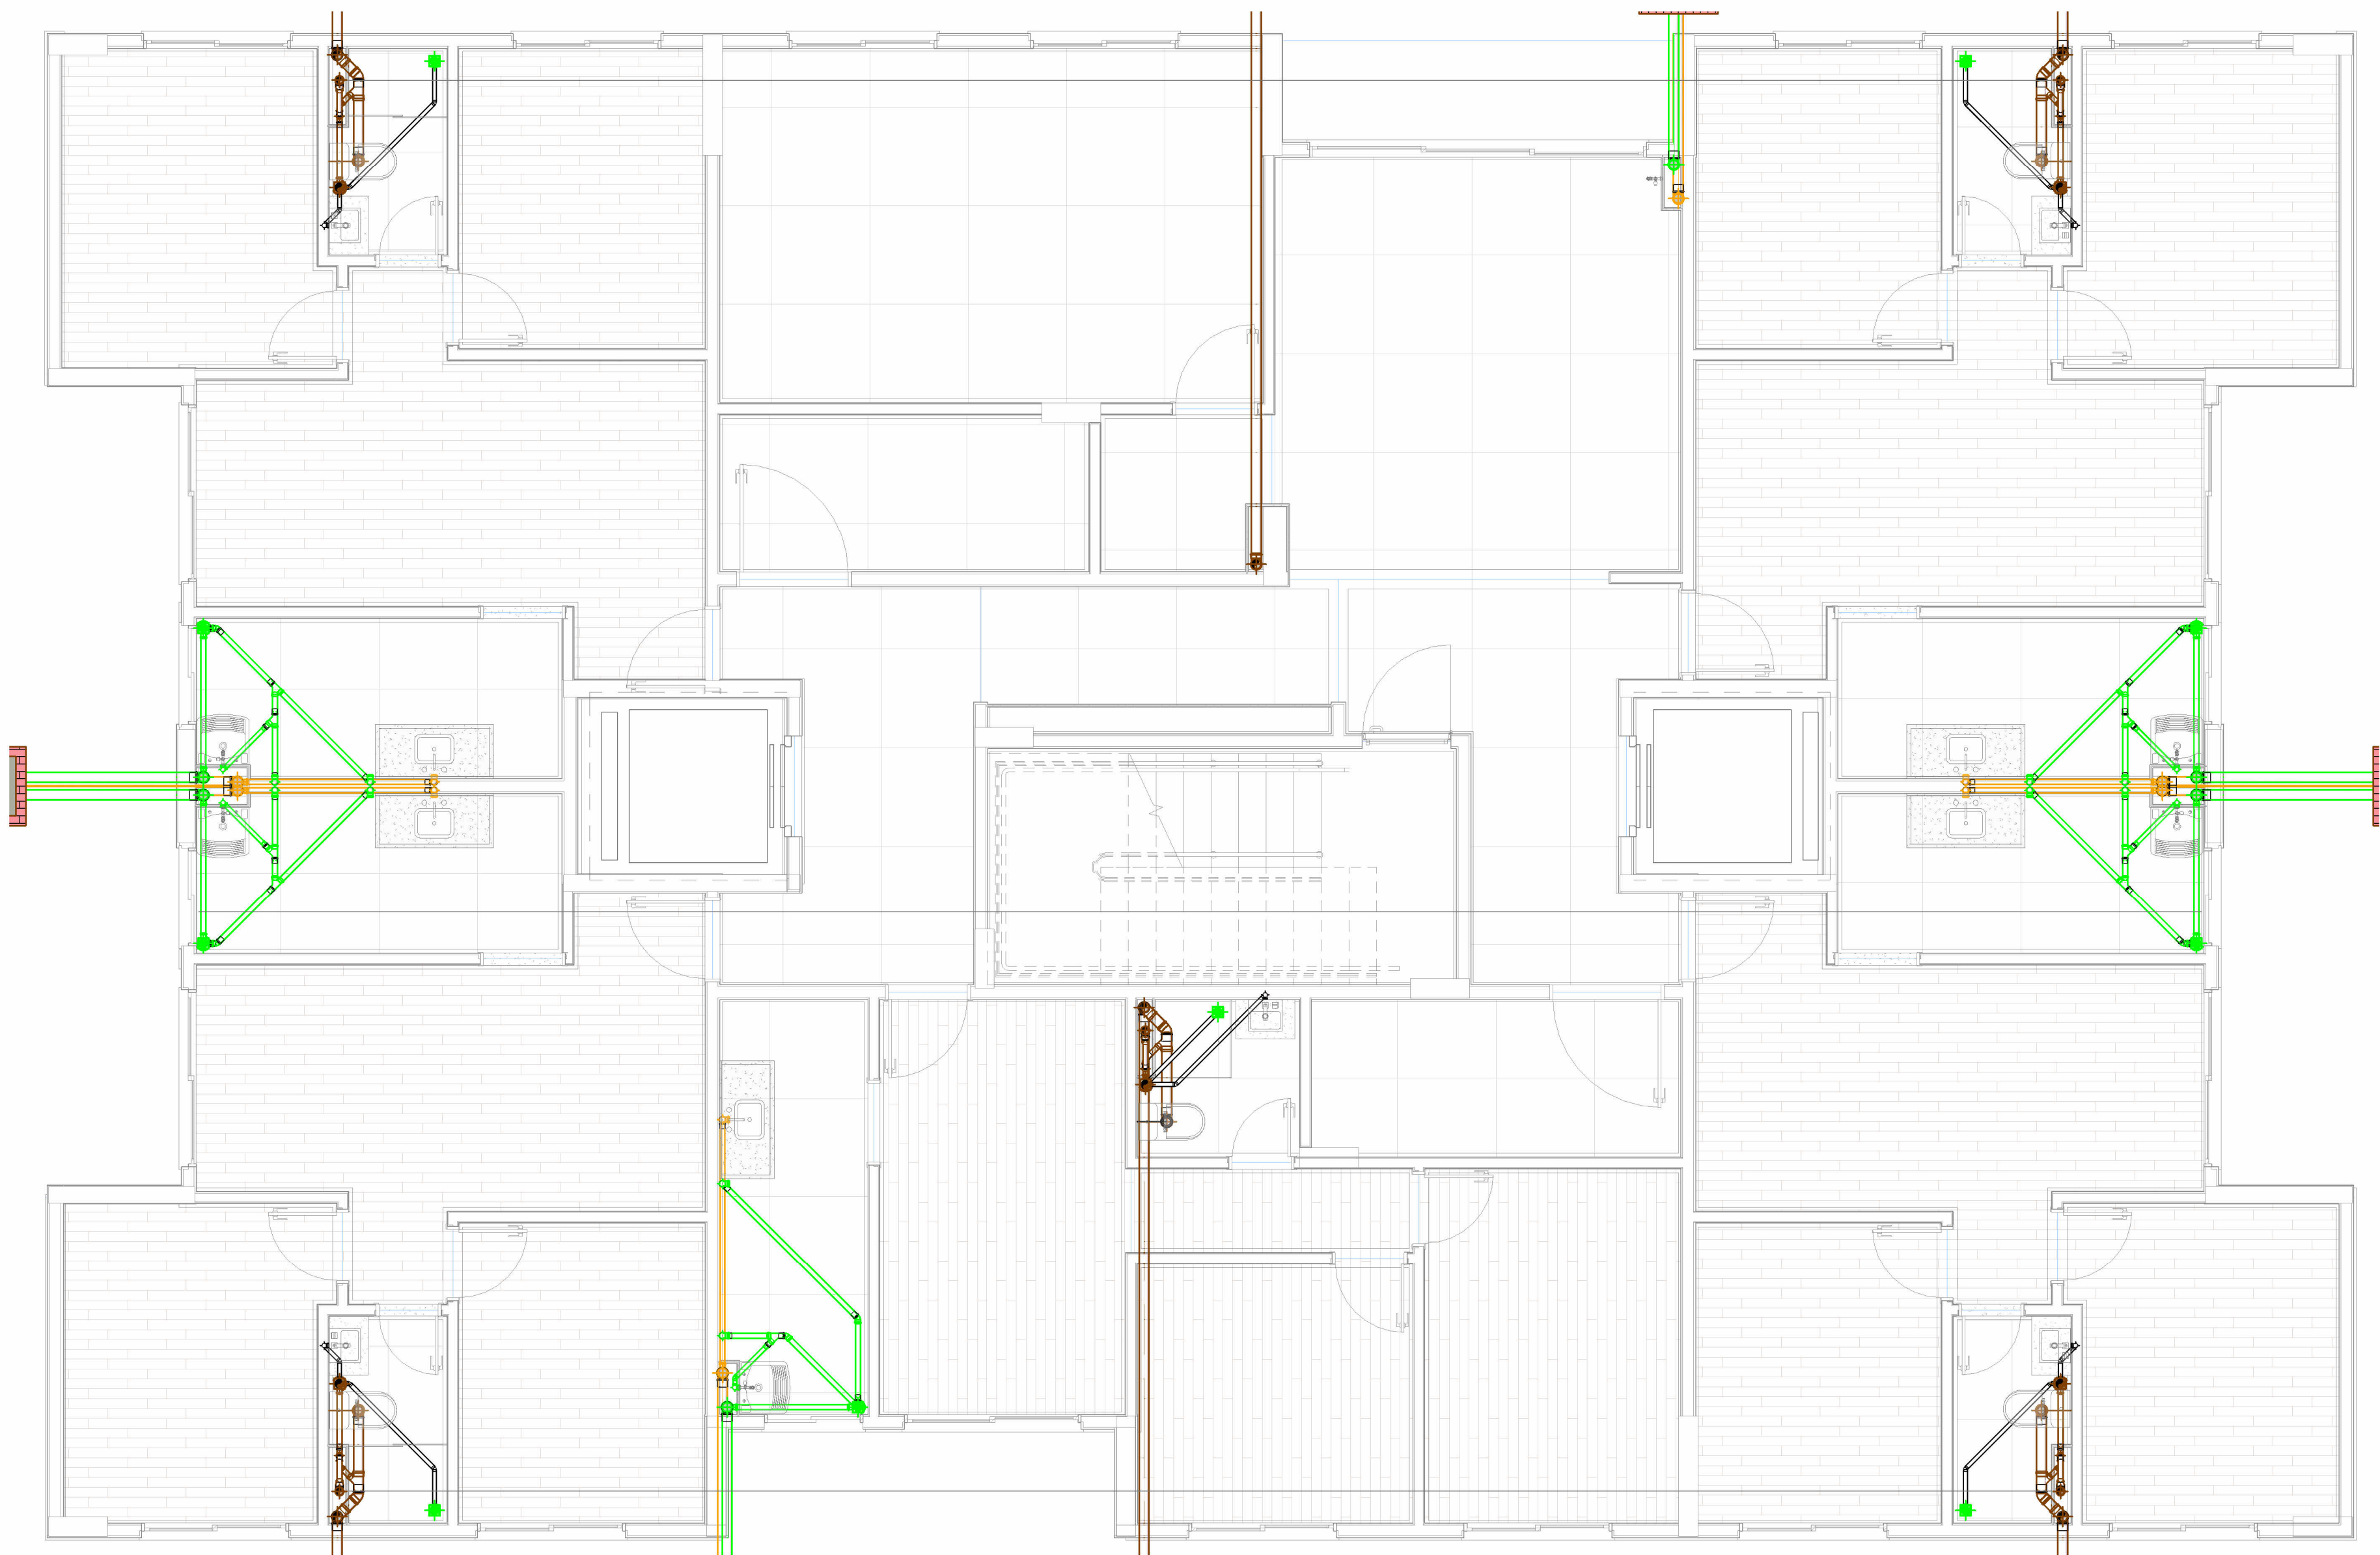

Pavimento Tipo 1

1 : 50

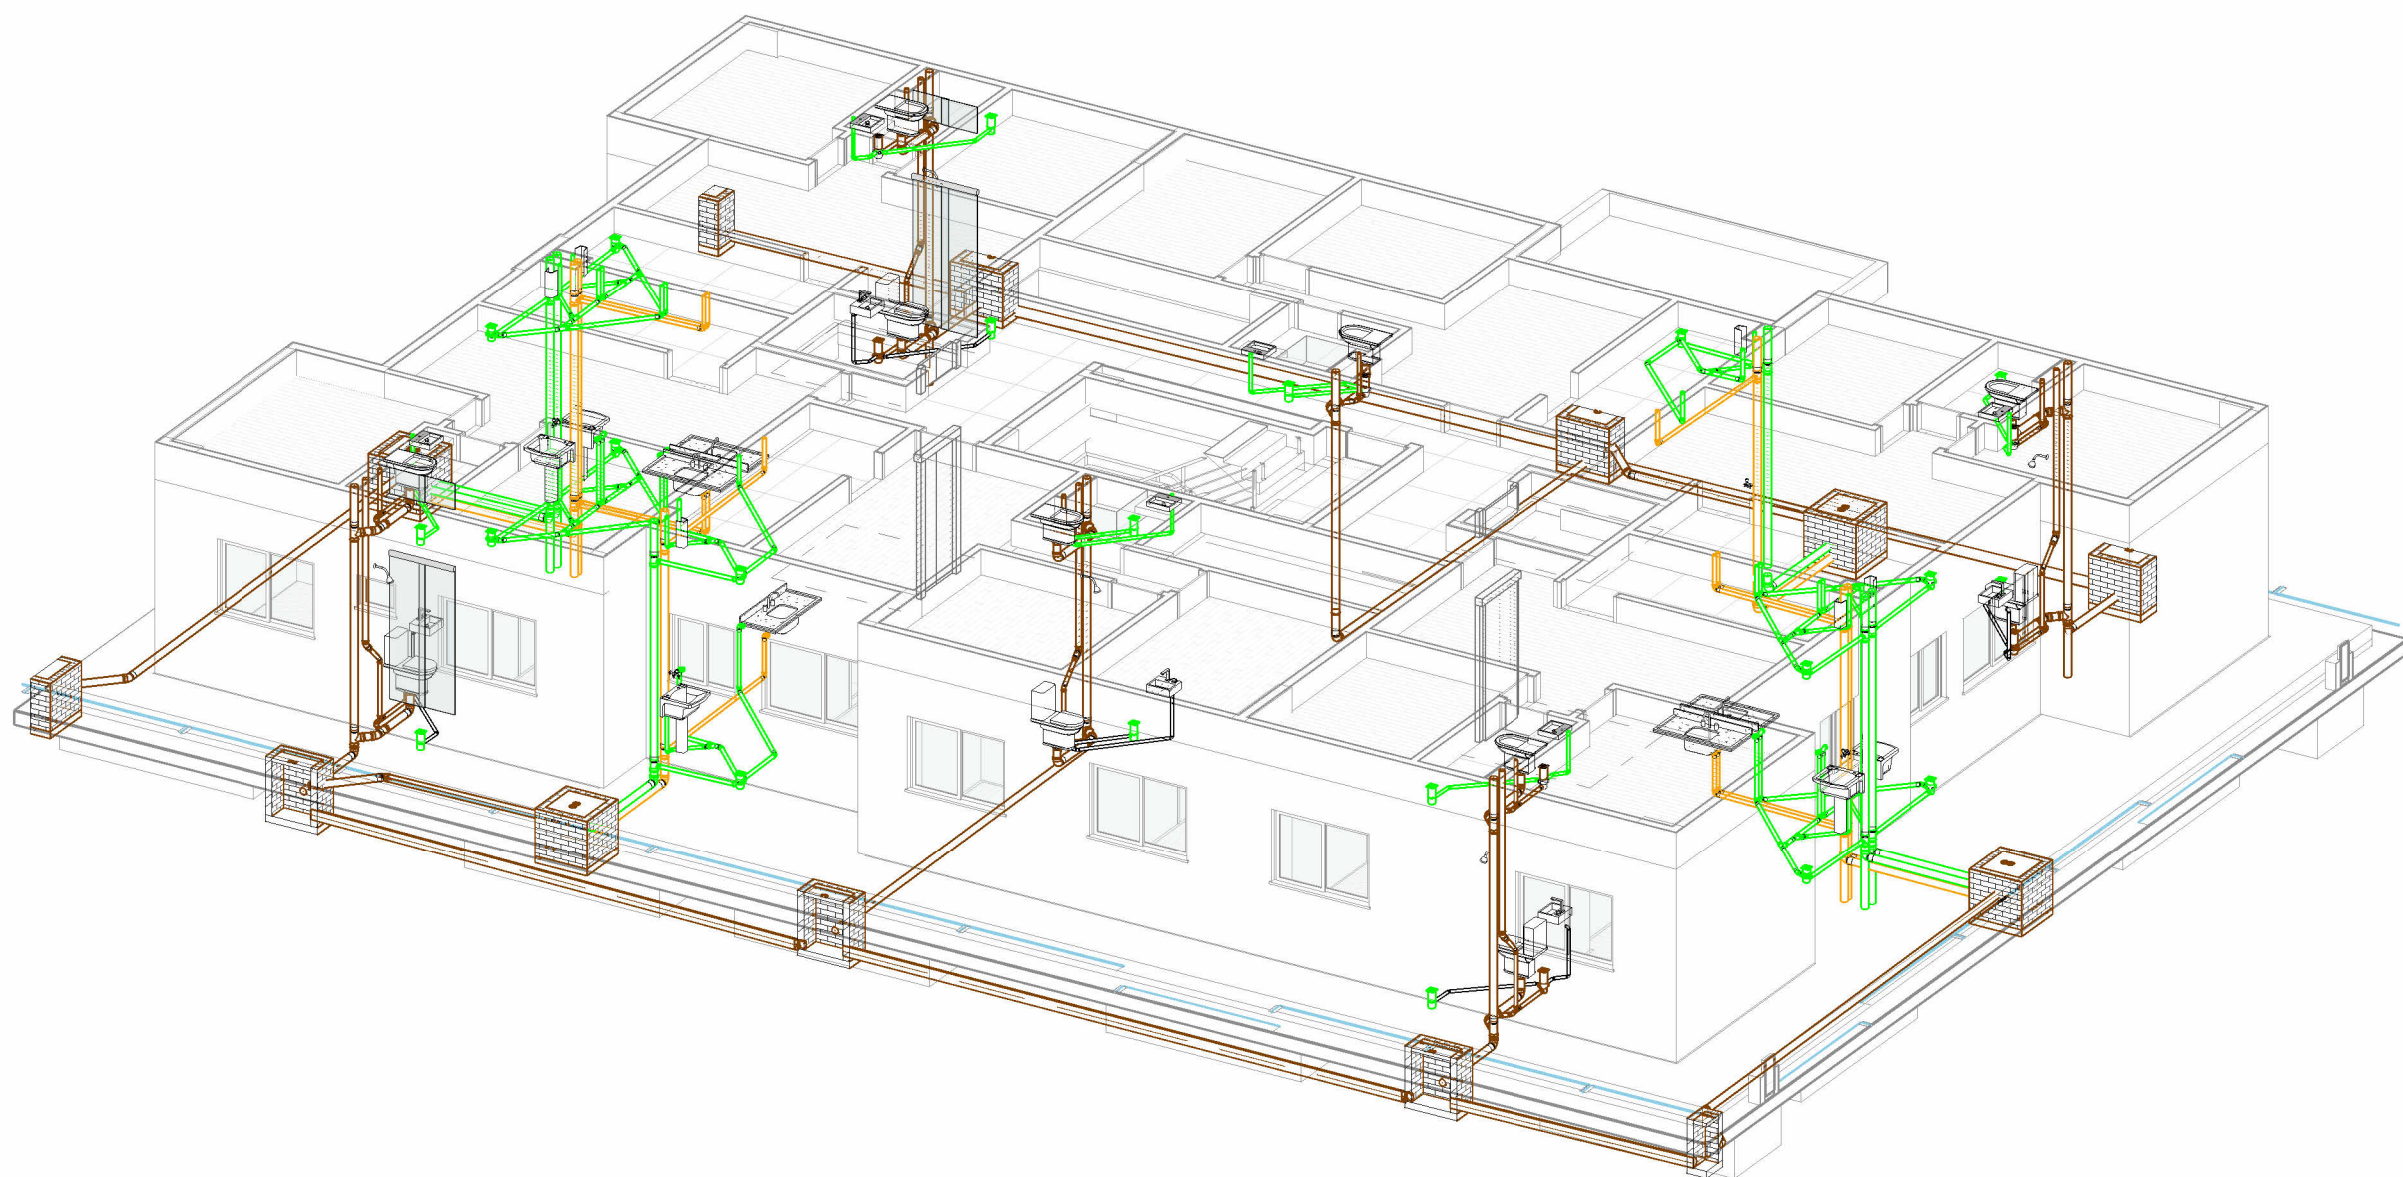

ISO - Pavimento Tipo 1

LEGENDA:

- TUBULAÇÃO PVC BRANCO SN - ESGOTO PRIMÁRIO
- TUBULAÇÃO PVC BRANCO SN - ESGOTO SECUNDÁRIO
- TUBULAÇÃO PVC BRANCO SN - VENTILAÇÃO ESGOTO
- TUBULAÇÃO PVC BRANCO SN - ESGOTO COM GORDURA

- TUBO DE QUEDA DE ESGOTO PRIMÁRIO
nn: número da coluna
xx: diâmetro nominal da coluna
- COLUNA DE VENTILAÇÃO
nn: número da coluna
xx: diâmetro nominal da coluna
- TUBO DE QUEDA DE GORDURA
nn: número da coluna
xx: diâmetro nominal da coluna
- POSIÇÃO DO ITEM NA LISTA DE MATERIAIS

ABREVIações:

- BS - BACIA SANITÁRIA
- LV - LAVATÓRIO
- CH - CHUVEIRO
- TN - TANQUE
- MLR - MÁQUINA DE LAVAR ROUPAS
- MLL - MÁQUINA DE LAVAR LOUÇAS
- DU - DUCHA HIGIÊNICA
- CS - CAIXA SIFONADA
- RS - RALO SECO
- CGP - CAIXA DE GORDURA PEQUENA
- CI - CAIXA DE INSPEÇÃO

NOTAS:

- DIMENSÕES E DIÂMETROS EM MILÍMETROS, EXCETO ONDE INDICADO CONTRÁRIO.
- NOS TRECHOS HORIZONTAIS DAS TUBULAÇÕES DE ESGOTO SANITÁRIO RECOMENDAM-SE AS SEGUINTE DECLIVIDADES MÍNIMAS:
 - 2% PARA TUBULAÇÕES COM DIÂMETRO NOMINAL IGUAL OU INFERIOR A 75mm;
 - 1% PARA TUBULAÇÕES COM DIÂMETRO NOMINAL IGUAL OU SUPERIOR A 100mm.
- UTILIZAR ANÉIS DE BORRACHA NAS CONEXÕES DE ESGOTO.
- PROIBIDO UTILIZAR FOGO NAS TUBULAÇÕES.
- OS TERMINAIS DE VENTILAÇÃO DOS TUBOS DE VENTILAÇÃO DEVERÃO PASSAR 30CM ACIMA DO TELHADO.
- UTILIZAR DISPOSITIVO ANTI-ESPUMA NA CAIXA SIFONADA DA ÁREA DE SERVIÇO.
- TODAS AS TUBULAÇÕES EXPOSTAS DEVERÃO SER FIXADAS COM BRAÇADEIRA

Lista de Materiais - Conexões e Acessórios	
Descrição do Material	Quantidade
	de
	1413
Adaptador para Saída de Vaso Sanitário, DN100mm, de PVC Rígido Branco Série Normal, conforme NBR 5688	14
Anel de Borracha, DN50mm, para linha de PVC Rígido Branco Série Normal, conforme NBR 5688	309
Anel de Borracha, DN75mm, para linha de PVC Rígido Branco Série Normal, conforme NBR 5688	11
Anel de Borracha, DN100mm, para linha de PVC Rígido Branco Série Normal, conforme NBR 5688	161
Anel de Borracha, DN150mm, para linha de PVC Rígido Branco Série Normal, conforme NBR 5688	2
Antesepuma para instalação em Caixa Sifonada DN100mm, Esgoto	11
Bucha de Redução, DN50x40mm, de PVC Rígido Branco Série Normal para Esgoto e Água Pluvial, conforme NBR 5688	22
Caixa de inspeção em alvenaria com tampa de concreto, 60x60cm	13
Caixa Sifonada Girafácil Montada com Greiha e Porta Greiha Quadrados Brancos 100x140x50mm, 5 Entradas, Esgoto	22
INEXISTENTE	5
Joelho 45°, DN40mm, de PVC Rígido Branco Série Normal, conforme NBR 5688	30
Joelho 45°, DN50mm, de PVC Rígido Branco Série Normal, conforme NBR 5688	30
Joelho 45°, DN75mm, de PVC Rígido Branco Série Normal, conforme NBR 5688	5
Joelho 45°, DN100mm, de PVC Rígido Branco Série Normal, conforme NBR 5688	15
Joelho 90° com anel, DN40mm, de PVC Rígido Branco Série Normal, conforme NBR 5688	10
Joelho 90°, DN40mm, de PVC Rígido Branco Série Normal, conforme NBR 5688	22
Joelho 90°, DN50mm, de PVC Rígido Branco Série Normal, conforme NBR 5688	48
Joelho 90°, DN100mm, de PVC Rígido Branco Série Normal, conforme NBR 5688	29
Junção 45° de Redução, DN100x50mm, de PVC Rígido Branco Série Normal, conforme NBR 5688	11
Junção 45°, DN50x50mm, de PVC Rígido Branco Série Normal, conforme NBR 5688	19
Luva Simples, DN50mm, de PVC Rígido Branco Série Normal, conforme NBR 5688	116
Luva Simples, DN75mm, de PVC Rígido Branco Série Normal, conforme NBR 5688	6
Luva Simples, DN100mm, de PVC Rígido Branco Série Normal, conforme NBR 5688	80
Luva Simples, DN150mm, de PVC Rígido Branco Série Normal, conforme NBR 5688	2
Ralo Seco Montado com Greiha e Porta Greiha Quadrados 100x100x40mm, Esgoto	11
Redução Excêntrica, DN150x100mm, de PVC Rígido Branco Série Normal para Esgoto e Água Pluvial, conforme NBR 5688	2
Tê 90° de Redução, DN100x50mm, de PVC Rígido Branco Série Normal, conforme NBR 5688	22
Tê 90°, DN50x50mm, de PVC Rígido Branco Série Normal, conforme NBR 5688	11
Tê 90°, DN100x100mm, de PVC Rígido Branco Série Normal, conforme NBR 5688	11
Esgoto Sanitário	
Anel de Borracha, DN100mm, para linha de PVC Rígido Branco Série Normal, conforme NBR 5688	12
Luva Simples, DN100mm, de PVC Rígido Branco Série Normal, conforme NBR 5688	4
Tê 90°, DN100x100mm, de PVC Rígido Branco Série Normal, conforme NBR 5688	4

Lista de Materiais - Tubos		
Descrição do Material	Diâmetro Nominal (mm)	Comprimento (m)
Tubo de PVC Rígido Branco, conforme NBR5688, Linha Série Normal	Ø150	43,88
Tubo de PVC Rígido Branco, conforme NBR5688, Linha Série Normal	Ø100	240,71
Tubo de PVC Rígido Branco, conforme NBR5688, Linha Série Normal	Ø75	16,00
Tubo de PVC Rígido Branco, conforme NBR5688, Linha Série Normal	Ø50	129,83
Tubo de PVC Rígido Branco, conforme NBR5688, Linha Série Normal	Ø40	46,58




PENN & WIZE
INSTALAÇÕES PREDIAIS
<https://pennwize.github.io/>



PROJETO: Edifício Derry and George
LOCAL: Rua dos bobos, n° 0. Natal/RN - Brasil
ASSUNTO: Pavimento Tipo 1
AUTORES DO PROJETO: Amanda João Pedro Melo e Letícia Tórres

FOLHA: E01
REV.:
ESCALA: 1 : 50
DATA: 12/02/2026

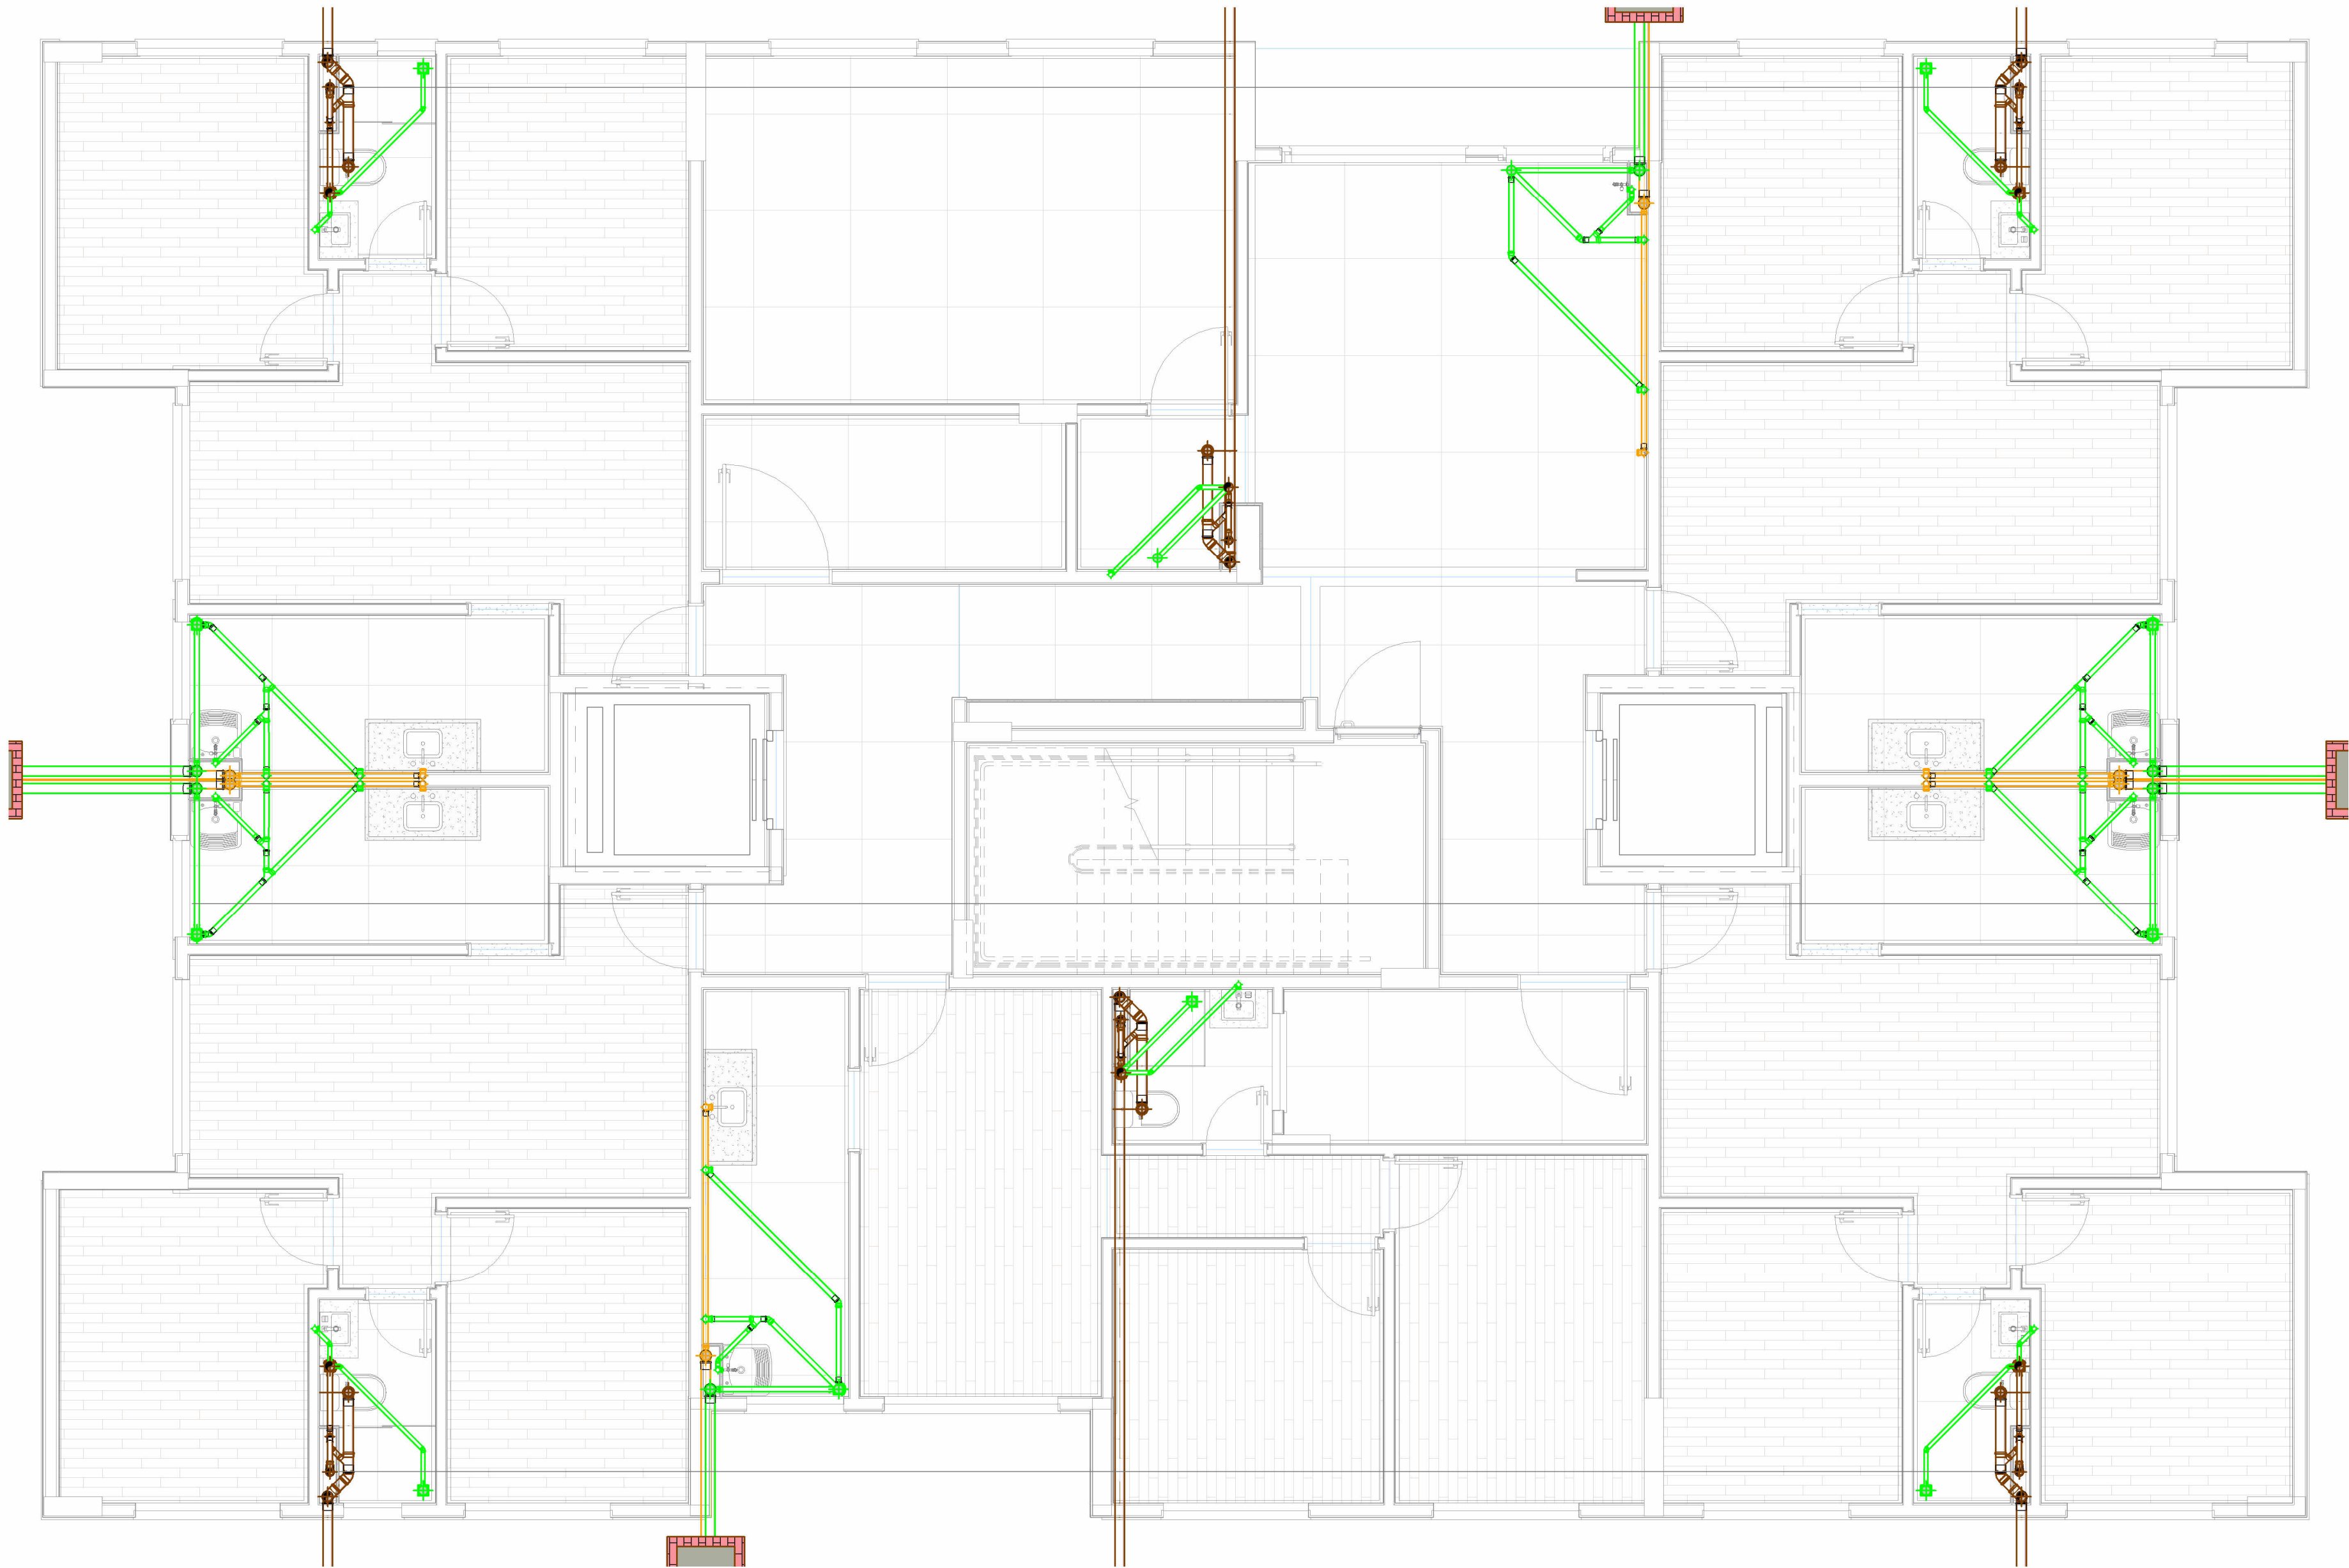

Pavimento Tipo 2

1 : 50



ISO - Pavimento Tipo 2

LEGENDA:

- TUBULAÇÃO PVC BRANCO SN - ESGOTO PRIMÁRIO
- TUBULAÇÃO PVC BRANCO SN - ESGOTO SECUNDÁRIO
- TUBULAÇÃO PVC BRANCO SN - VENTILAÇÃO ESGOTO
- TUBULAÇÃO PVC BRANCO SN - ESGOTO COM GORDURA

- TUBO DE QUEDA DE ESGOTO PRIMÁRIO
nn: numero da coluna
xx: diâmetro nominal da coluna
- COLUNA DE VENTILAÇÃO
nn: numero da coluna
xx: diâmetro nominal da coluna
- TUBO DE QUEDA DE GORDURA
nn: numero da coluna
xx: diâmetro nominal da coluna
- POSIÇÃO DO ITEM NA LISTA DE MATERIAIS

ABREVIações:

- BS - BACIA SANITÁRIA
- LV - LAVATÓRIO
- CH - CHUVEIRO
- TN - TANQUE
- MLR - MÁQUINA DE LAVAR ROUPAS
- MLL - MÁQUINA DE LAVAR LOUÇAS
- DU - DUCHA HIGIÊNICA
- CS - CAIXA SIFONADA
- RS - RALO SECO
- CGP - CAIXA DE GORDURA PEQUENA
- CI - CAIXA DE INSPEÇÃO

NOTAS:


- DIMENSÕES E DIÂMETROS EM MILÍMETROS, EXCETO ONDE INDICADO CONTRÁRIO.
- NOS TRECHOS HORIZONTAIS DAS TUBULAÇÕES DE ESGOTO SANITÁRIO RECOMENDAM-SE AS SEGUINTE DECLIVIDADES MÍNIMAS:
 - 2% PARA TUBULAÇÕES COM DIÂMETRO NOMINAL IGUAL OU INFERIOR A 75mm;
 - 1% PARA TUBULAÇÕES COM DIÂMETRO NOMINAL IGUAL OU SUPERIOR A 100mm.
- UTILIZAR ANÉIS DE BORRACHA NAS CONEXÕES DE ESGOTO.
- PROIBIDO UTILIZAR FOGO NAS TUBULAÇÕES.
- OS TERMINAIS DE VENTILAÇÃO DOS TUBOS DE VENTILAÇÃO DEVERÃO PASSAR 30CM ACIMA DO TELHADO.
- UTILIZAR DISPOSITIVO ANTI-ESPUMA NA CAIXA SIFONADA DA ÁREA DE SERVIÇO.
- TODAS AS TUBULAÇÕES EXPOSTAS DEVERÃO SER FIXADAS COM BRAÇADEIRA

Lista de Materiais - Conexões e Acessórios	
Descrição do Material	Quantidade
	de
	1428
Adaptador para Saída de Vaso Sanitário, DN100mm, de PVC Rígido Branco Série Normal, conforme NBR 5688	22
Anel de Borracha, DN50mm, para linha de PVC Rígido Branco Série Normal, conforme NBR 5688	563
Anel de Borracha, DN75mm, para linha de PVC Rígido Branco Série Normal, conforme NBR 5688	29
Anel de Borracha, DN100mm, para linha de PVC Rígido Branco Série Normal, conforme NBR 5688	243
Antespuma para instalação em Caixa Sifonada DN100mm, Esgoto	11
Bucha de Redução, DN50x40mm, de PVC Rígido Branco Série Normal para Esgoto e Água Pluvial, conforme NBR 5688	34
Caixa de inspeção em alvenaria com tampa de concreto, 60x60cm	4
Caixa Sifonada Girafácil Montada com Grelha e Porta Grelha Quadrados Brancos 100x140x50mm, 5 Entradas, Esgoto	22
INEXISTENTE	5
Joelho 45°, DN40mm, de PVC Rígido Branco Série Normal, conforme NBR 5688	46
Joelho 45°, DN50mm, de PVC Rígido Branco Série Normal, conforme NBR 5688	56
Joelho 45°, DN75mm, de PVC Rígido Branco Série Normal, conforme NBR 5688	5
Joelho 45°, DN100mm, de PVC Rígido Branco Série Normal, conforme NBR 5688	17
Joelho 90° com anel, DN40mm, de PVC Rígido Branco Série Normal, conforme NBR 5688	34
Joelho 90°, DN40mm, de PVC Rígido Branco Série Normal, conforme NBR 5688	34
Joelho 90°, DN50mm, de PVC Rígido Branco Série Normal, conforme NBR 5688	102
Joelho 90°, DN100mm, de PVC Rígido Branco Série Normal, conforme NBR 5688	35
Junção 45° de Redução, DN75x50mm, de PVC Rígido Branco Série Normal, conforme NBR 5688	12
Junção 45° de Redução, DN100x50mm, de PVC Rígido Branco Série Normal, conforme NBR 5688	17
Junção 45°, DN50x50mm, de PVC Rígido Branco Série Normal, conforme NBR 5688	29
Luva Simples, DN50mm, de PVC Rígido Branco Série Normal, conforme NBR 5688	216
Luva Simples, DN75mm, de PVC Rígido Branco Série Normal, conforme NBR 5688	12
Luva Simples, DN100mm, de PVC Rígido Branco Série Normal, conforme NBR 5688	106
Ralo Seco Montado com Grelha e Porta Grelha Quadrados 100x100x40mm, Esgoto	11
Tê 90° de Redução, DN100x50mm, de PVC Rígido Branco Série Normal, conforme NBR 5688	34
Tê 90°, DN50x50mm, de PVC Rígido Branco Série Normal, conforme NBR 5688	17
Tê 90°, DN100x100mm, de PVC Rígido Branco Série Normal, conforme NBR 5688	17


Lista de Materiais - Tubos		
Descrição do Material	Diâmetro Nominal (mm)	Comprimento (m)
Tubo de PVC Rígido Branco, conforme NBR5688, Linha Série Normal	Ø100	279,85
Tubo de PVC Rígido Branco, conforme NBR5688, Linha Série Normal	Ø75	34,86
Tubo de PVC Rígido Branco, conforme NBR5688, Linha Série Normal	Ø50	203,92
Tubo de PVC Rígido Branco, conforme NBR5688, Linha Série Normal	Ø40	72,13



PENN & WIZE
INSTALAÇÕES PREDIAIS
<https://pennwize.github.io/>

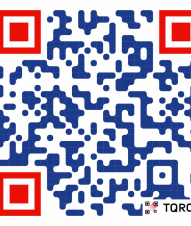

PROJETO:	Edifício Derry and Georgie	FOLHA:	E02
LOCAL:	Rua dos bobos, nº 0. Natal/RN - Brasil	REV.:	
ASSUNTO:	Pavimento Tipo 2	ESCALA:	1 : 50
AUTORES DO PROJETO:	Amanda João Pedro Melo e Leticia Tórres	DATA:	12/02/2026

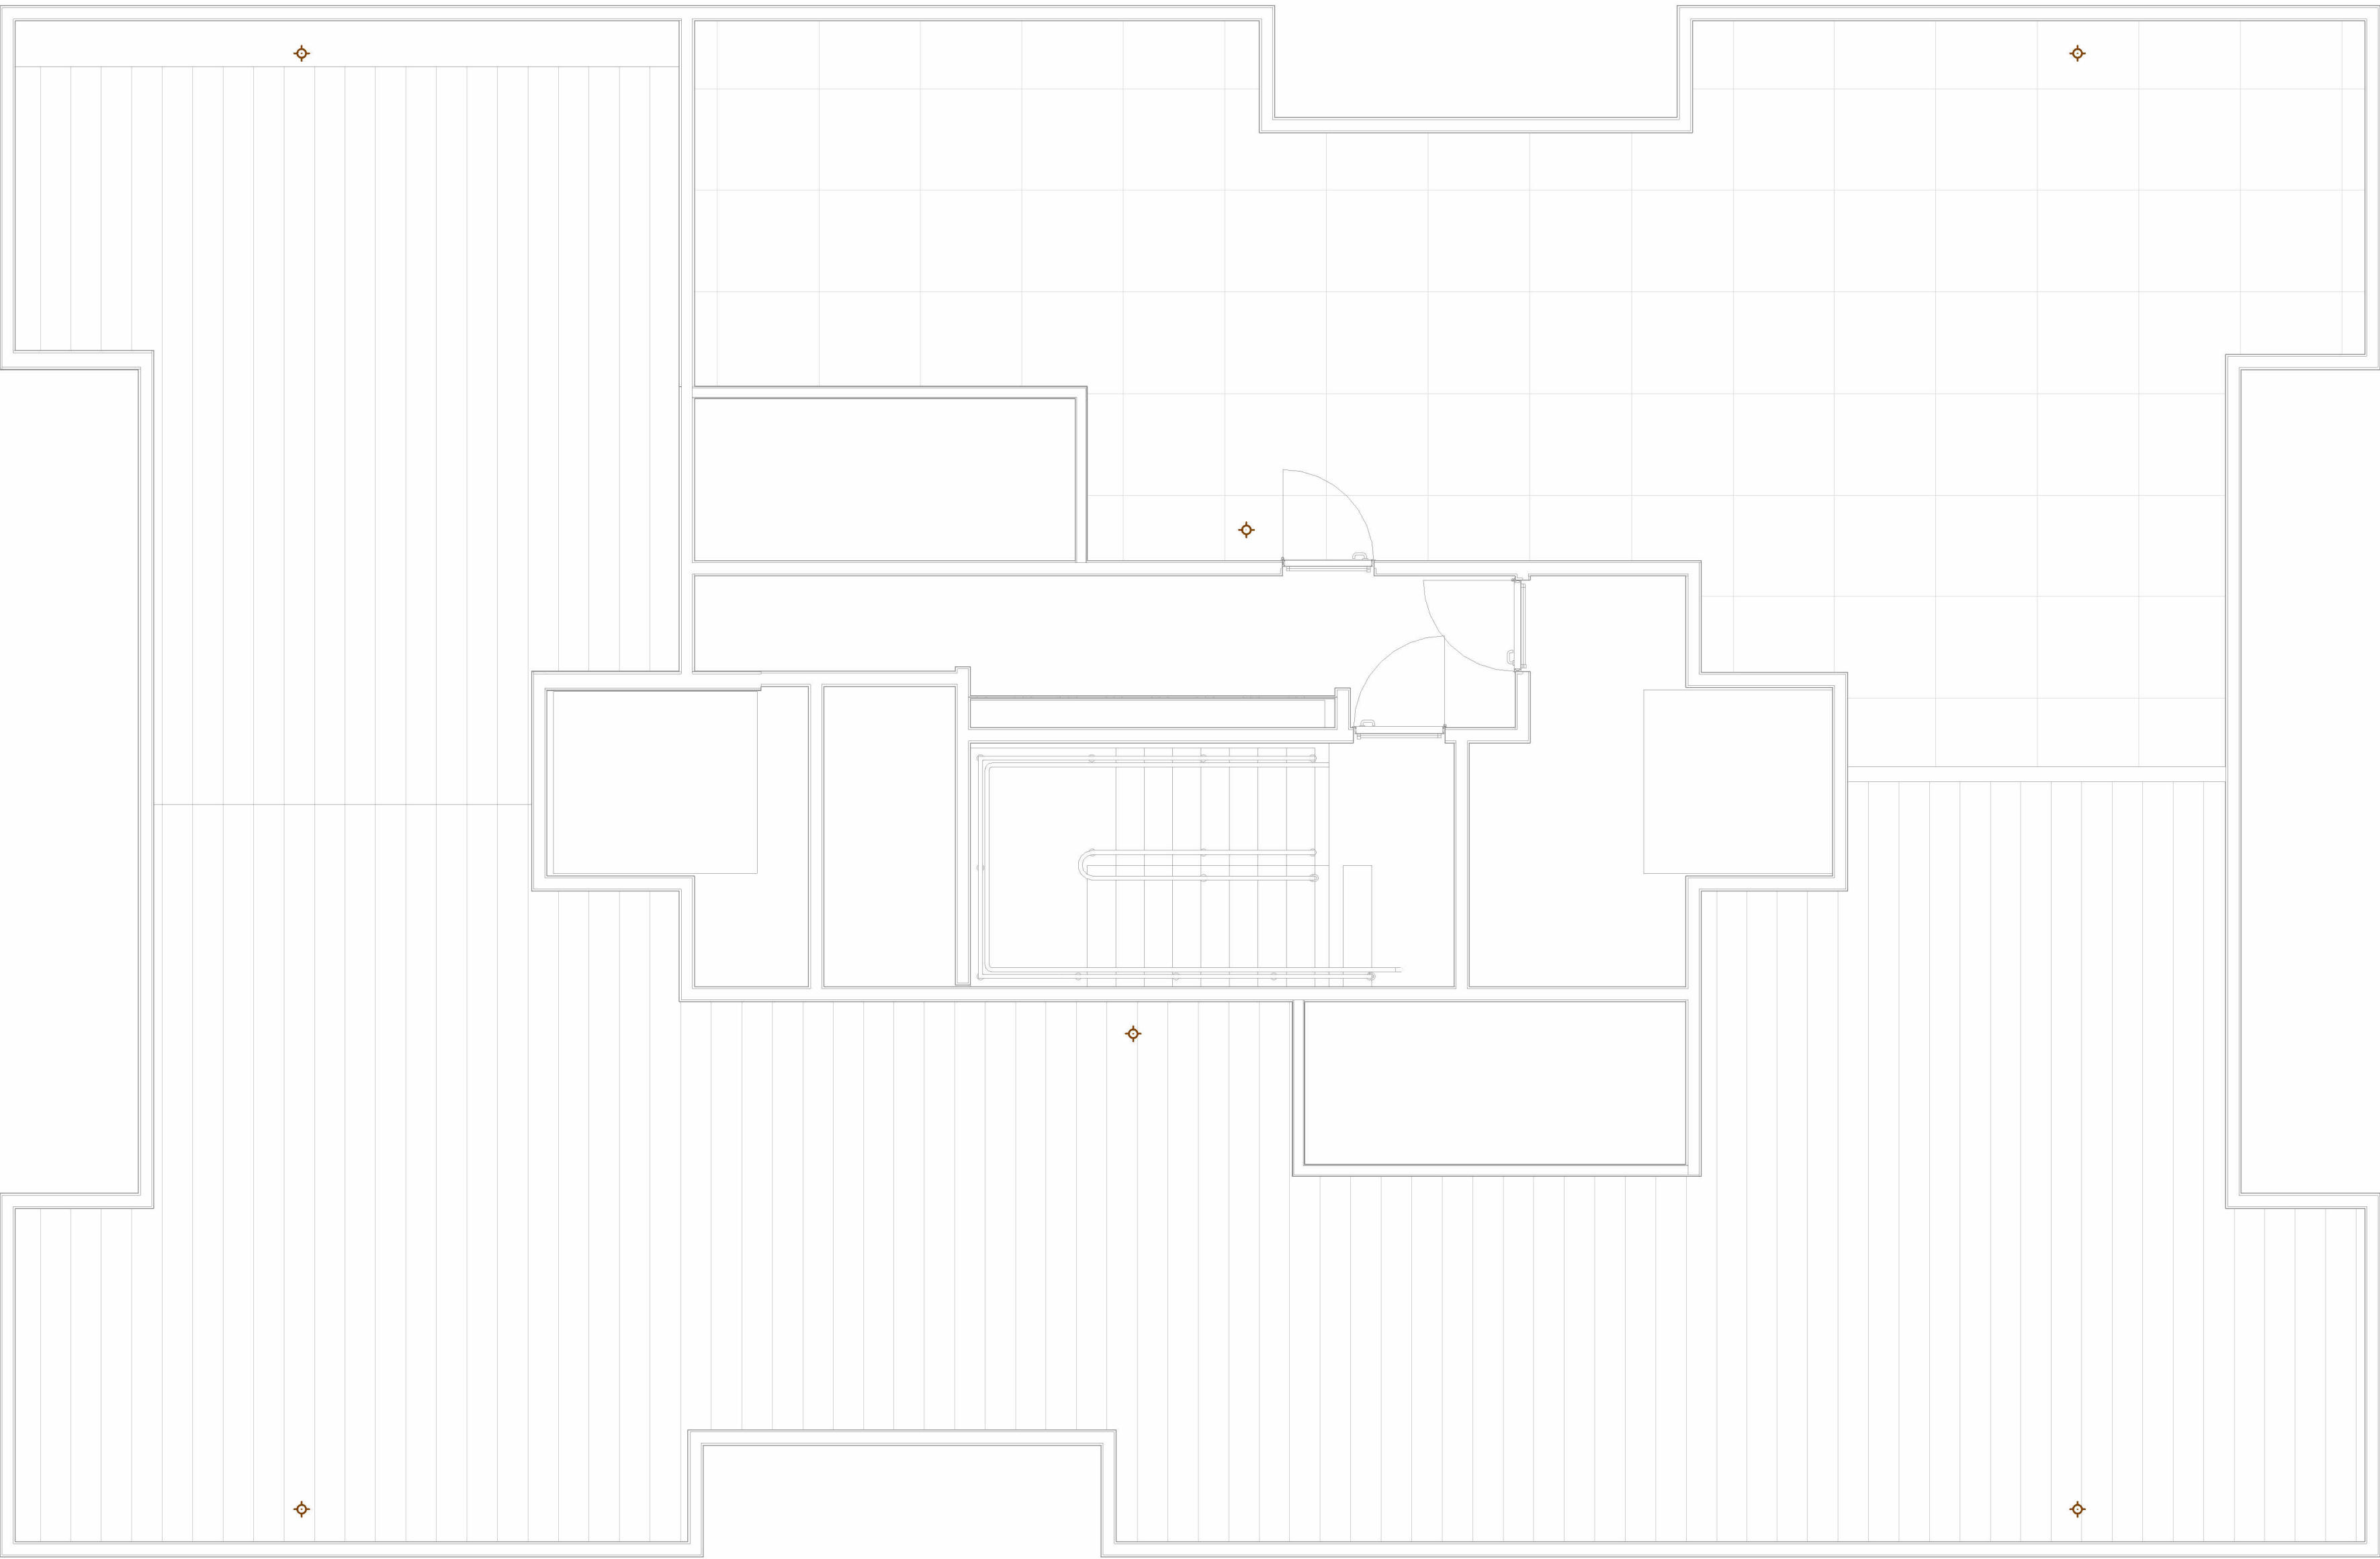

LEGENDA:

- TUBULAÇÃO PVC BRANCO SN - ESGOTO PRIMÁRIO
- TUBULAÇÃO PVC BRANCO SN - ESGOTO SECUNDÁRIO
- TUBULAÇÃO PVC BRANCO SN - VENTILAÇÃO ESGOTO
- TUBULAÇÃO PVC BRANCO SN - ESGOTO COM GORDURA

TG-nh
Øxx

-TUBO DE QUEDA DE ESGOTO PRIMÁRIO
nh: numero da coluna
xx: diâmetro nominal da coluna

CV-nh
Øxx

-COLUNA DE VENTILAÇÃO
nh: numero da coluna
xx: diâmetro nominal da coluna

TG-nh
Øxx

-TUBO DE QUEDA DE GORDURA
nh: numero da coluna
xx: diâmetro nominal da coluna

xx

-POSIÇÃO DO ITEM NA LISTA DE MATERIAIS

ABREVIações:

- BS - BACIA SANITÁRIA
- LV - LAVATÓRIO
- CH - CHUVEIRO
- TN - TANQUE
- MLR - MÁQUINA DE LAVAR ROUPAS
- MLL - MÁQUINA DE LAVAR LOUÇAS
- DU - DUCHA HIGIÊNICA
- CS - CAIXA SIFONADA
- RS - RALO SECO
- GCP - CAIXA DE GORDURA PEQUENA
- CI - CAIXA DE INSPEÇÃO


NOTAS:

- DIMENSÕES E DIÂMETROS EM MILÍMETROS, EXCETO ONDE INDICADO CONTRÁRIO.
- NOS TRECHOS HORIZONTAIS DAS TUBULAÇÕES DE ESGOTO SANITÁRIO RECOMENDAM-SE AS SEGUINTES DECLIVIDADES MÍNIMAS:
 - 2% PARA TUBULAÇÕES COM DIÂMETRO NOMINAL IGUAL OU INFERIOR A 75mm;
 - 1% PARA TUBULAÇÕES COM DIÂMETRO NOMINAL IGUAL OU SUPERIOR A 100mm.
- UTILIZAR ANÉIS DE BORRACHA NAS CONEXÕES DE ESGOTO.
- PROIBIDO UTILIZAR FOGO NAS TUBULAÇÕES.
- OS TERMINAIS DE VENTILAÇÃO DOS TUBOS DE VENTILAÇÃO DEVERÃO PASSAR 30CM ACIMA DO TELHADO.
- UTILIZAR DISPOSITIVO ANTI-ESPUMA NA CAIXA SIFONADA DA ÁREA DE SERVIÇO.
- TODAS AS TUBULAÇÕES EXPOSTAS DEVERÃO SER FIXADAS COM BRAÇADEIRA

Lista de Materiais - Conexões e Acessórios	
Descrição do Material	Quantidade
	1392
Terminal de Ventilação, DN75mm, de PVC Rígido Branco Série Normal, conforme NBR 5688	6

Cobertura

1 : 50

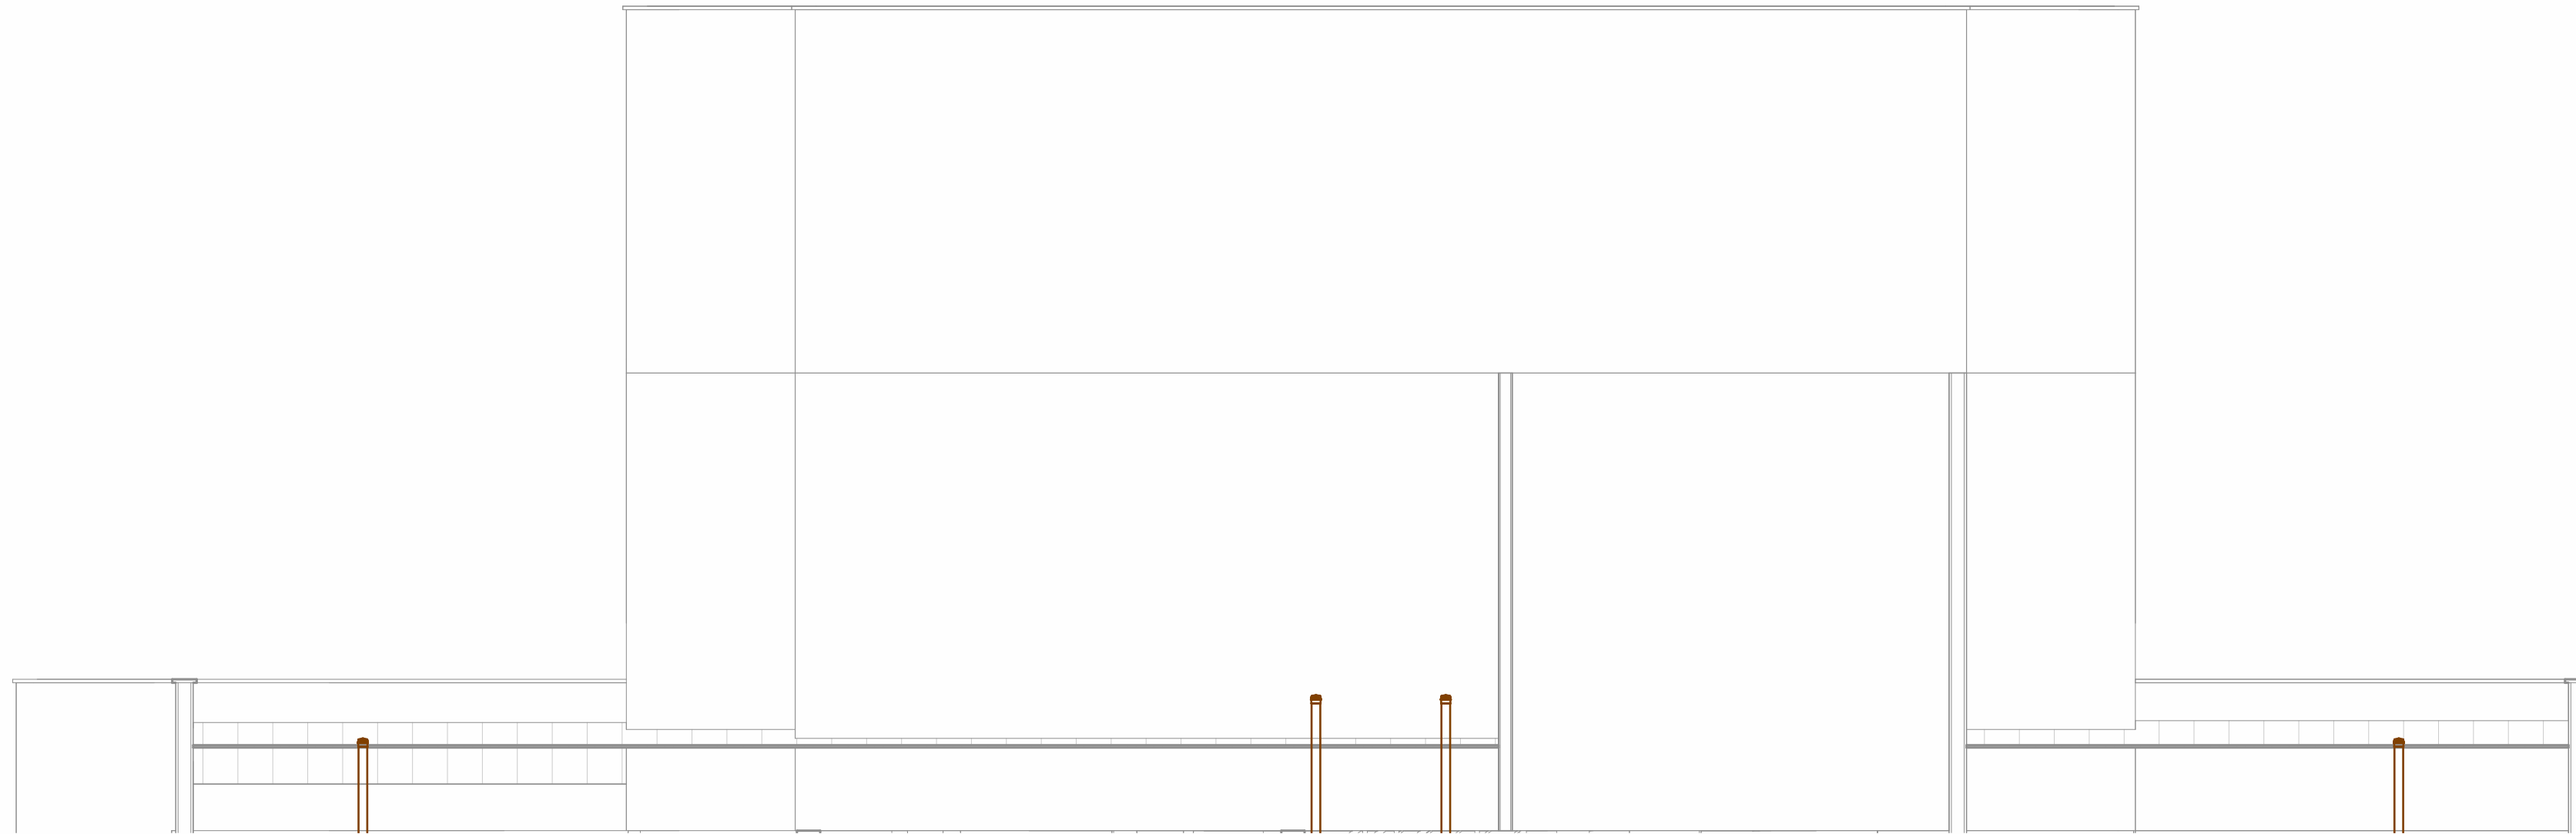

Cobertura prolongamento

1 : 50



Lista de Materiais - Tubos			
Descrição do Material	Diâmetro Nominal (mm)	Comprimento (m)	
Tubo de PVC Rígido Branco, conforme NBR5688, Linha Série Normal	Ø75	15,28	



PENN & WIZE
INSTALAÇÕES PREDIAIS
<https://pennwize.github.io/>





PROJETO:	Edifício Derry and Georgie	FOLHA:	E03
LOCAL:	Rua dos bobos, nº 0. Natal/RN - Brasil	REV.:	
ASSUNTO:	Prolongamentos Cobertura	ESCALA:	1 : 50
AUTORES DO PROJETO:	Amanda João Pedro Melo e Letícia Tórres	DATA:	12/02/2026

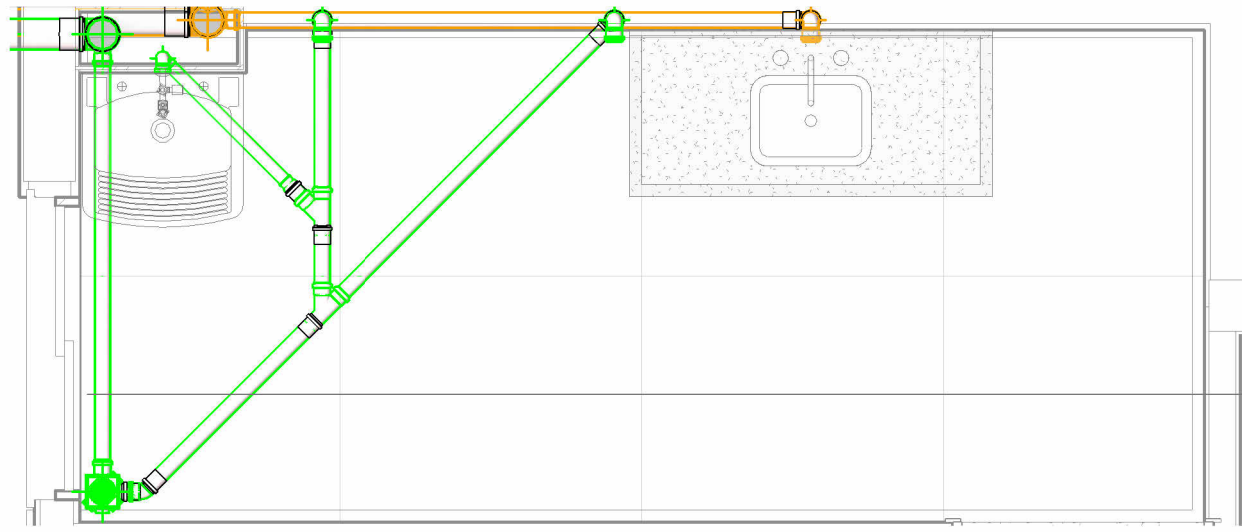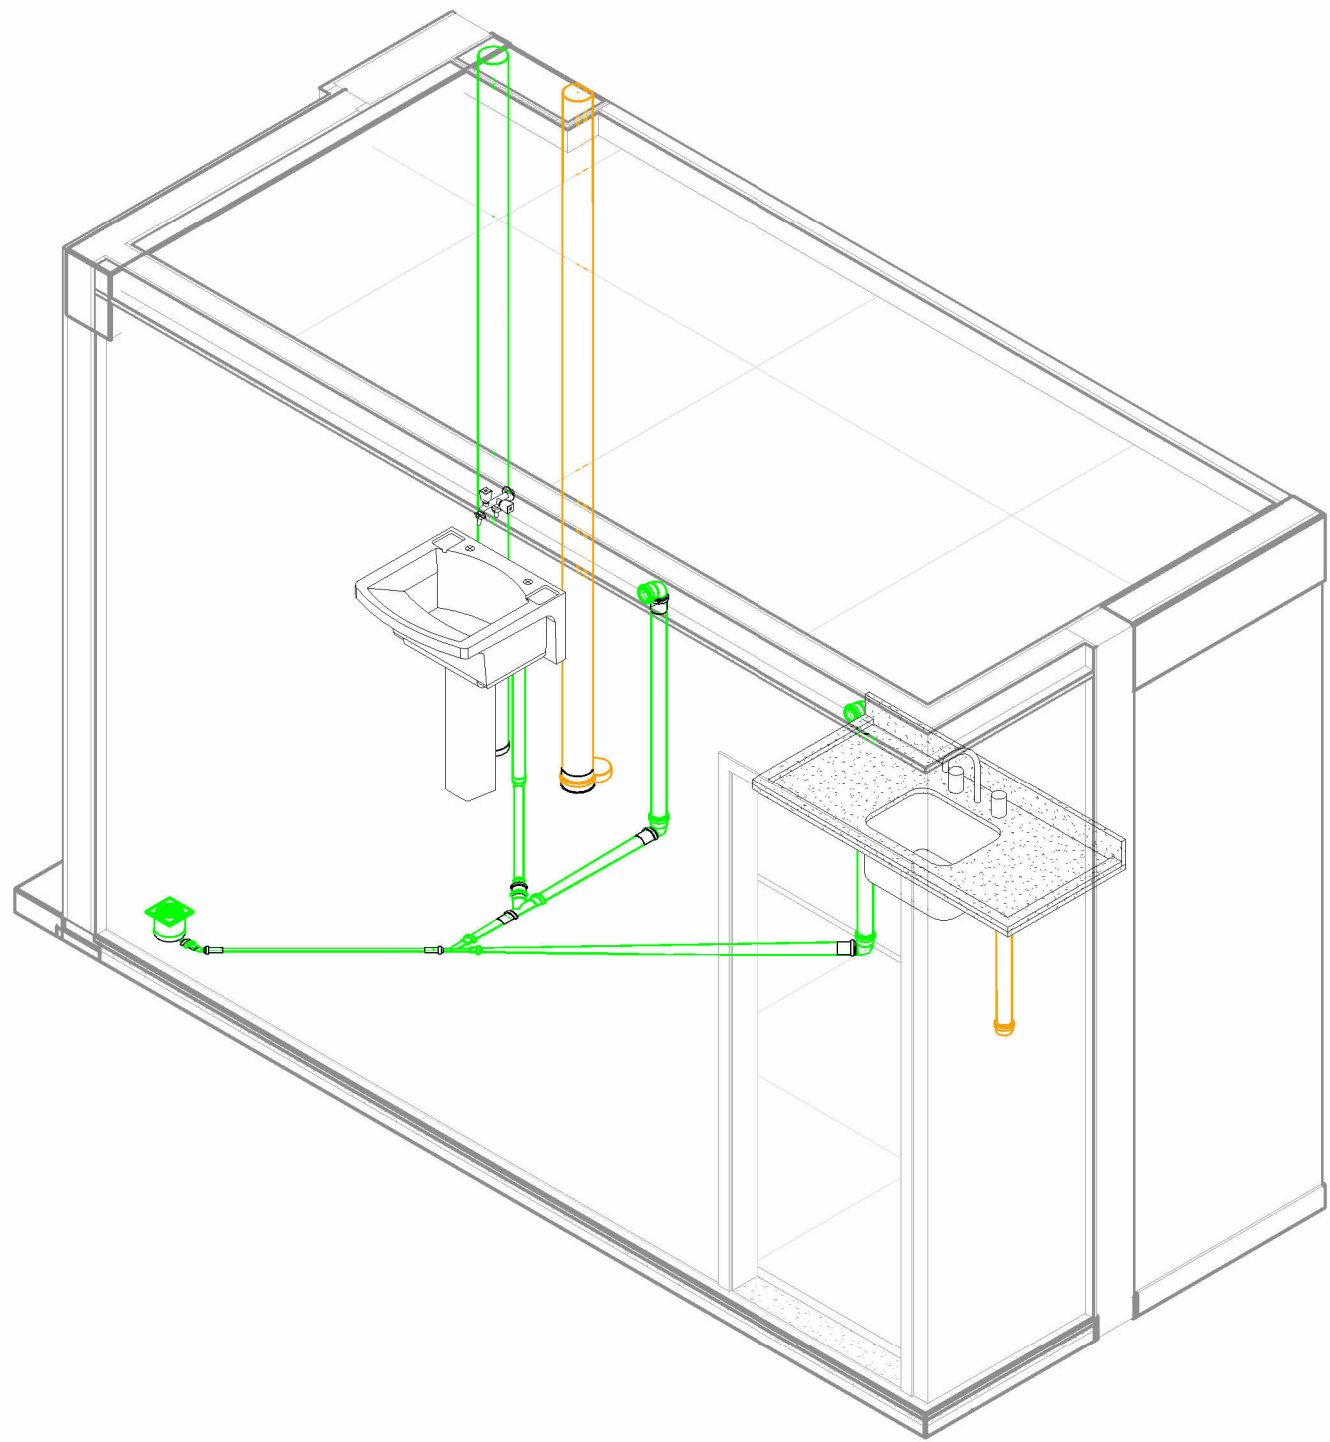

Cozinha 1
1 : 25

ISO - Cozinha 1

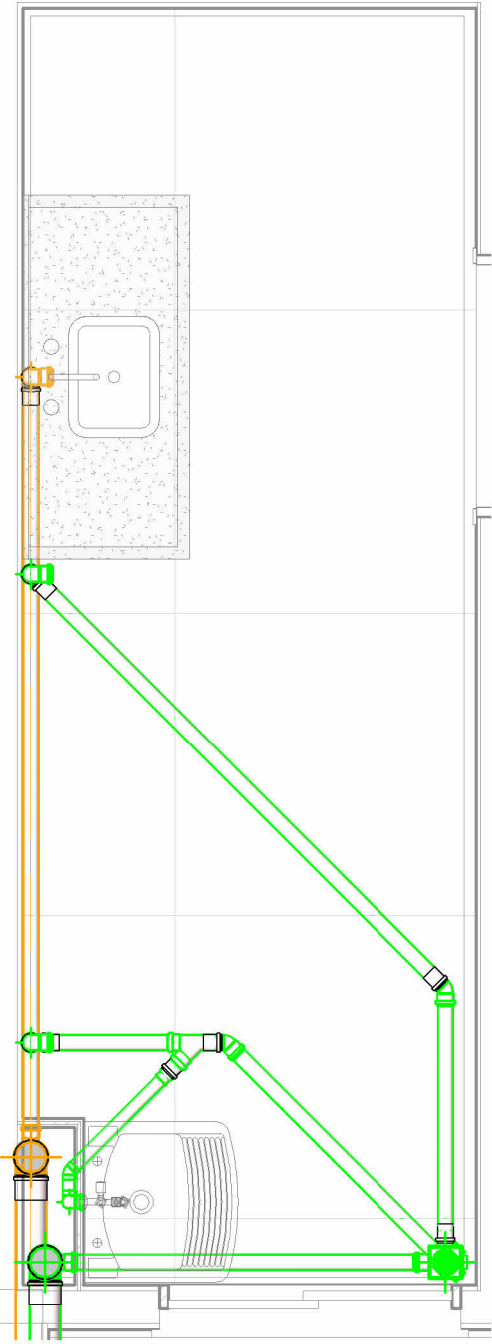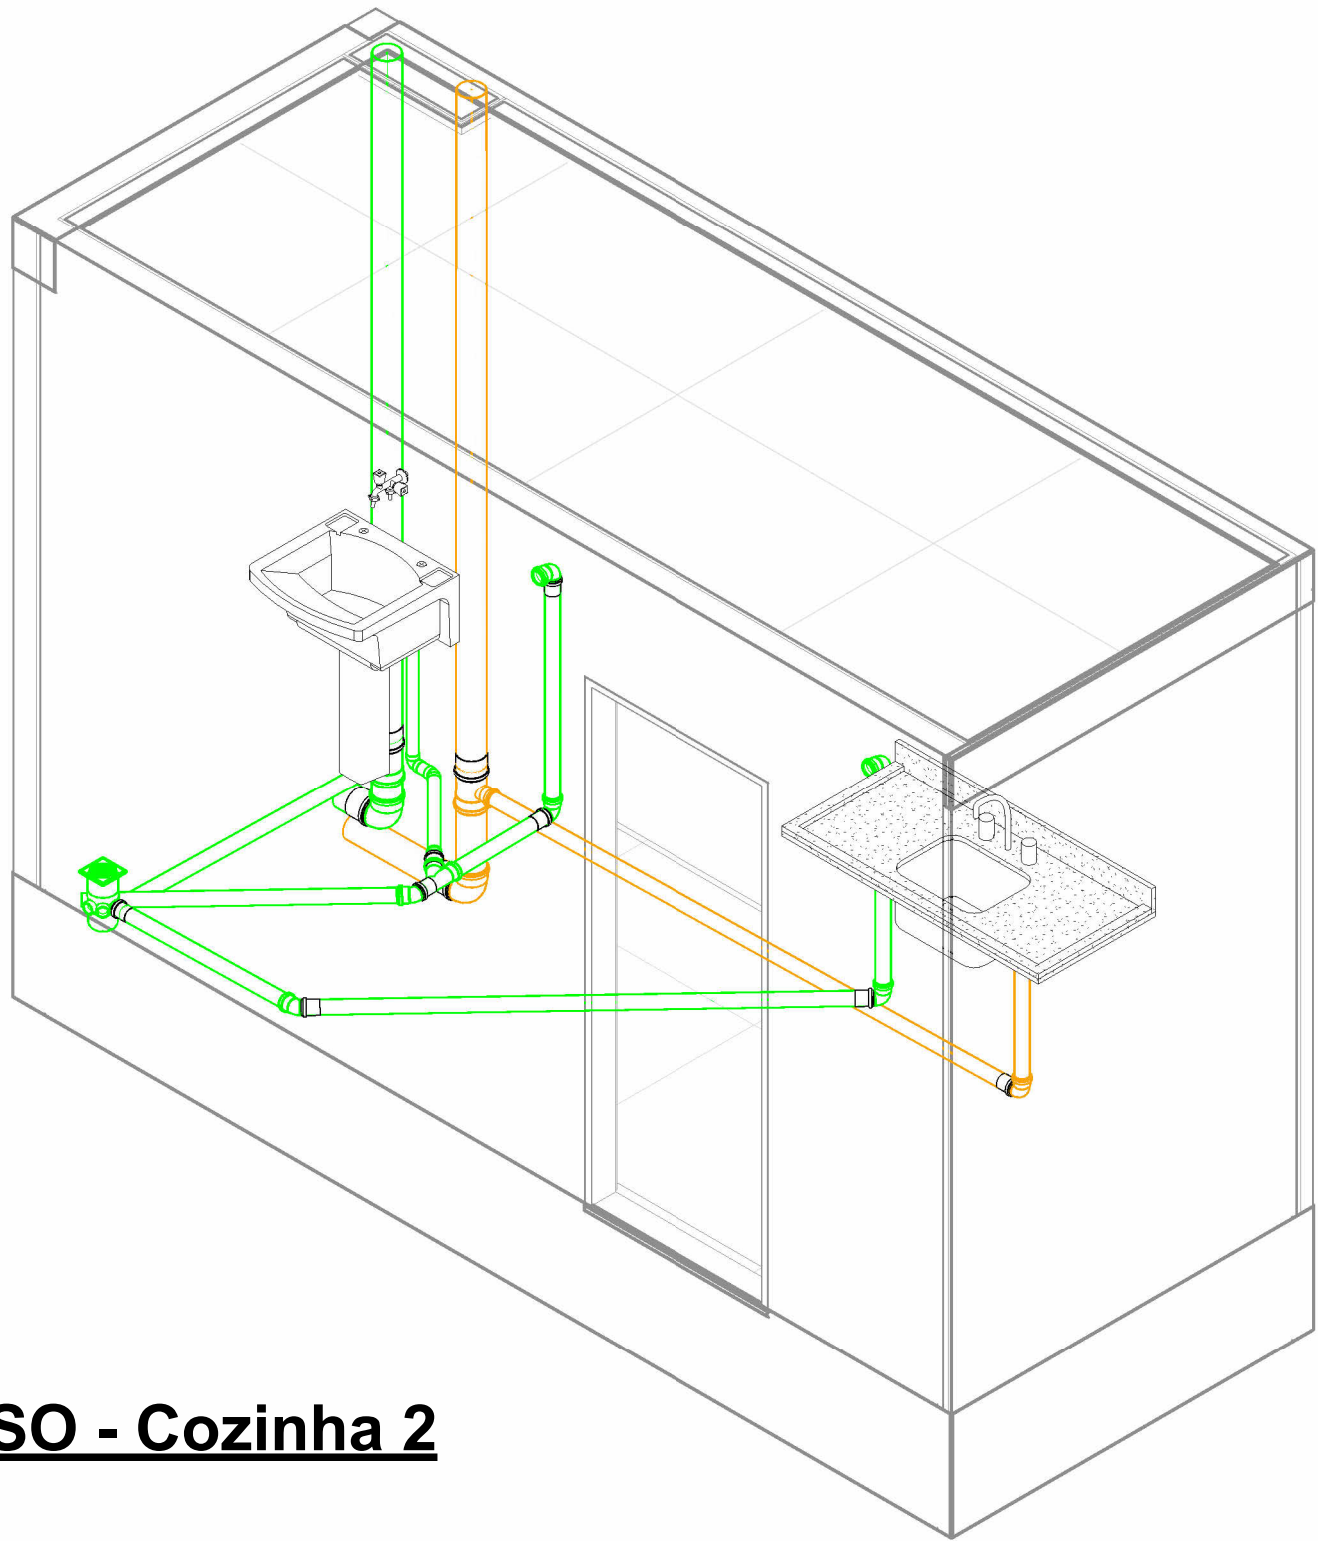

Cozinha 2
1 : 25

LEGENDA:

- TUBULAÇÃO PVC BRANCO SN - ESGOTO PRIMÁRIO
- TUBULAÇÃO PVC BRANCO SN - ESGOTO SECUNDÁRIO
- TUBULAÇÃO PVC BRANCO SN - VENTILAÇÃO ESGOTO
- TUBULAÇÃO PVC BRANCO SN - ESGOTO COM GORDURA

- TUBO DE QUEDA DE ESGOTO PRIMÁRIO
nn: número da coluna
xx: diâmetro nominal da coluna
- COLUNA DE VENTILAÇÃO
nn: número da coluna
xx: diâmetro nominal da coluna
- TUBO DE QUEDA DE GORDURA
nn: número da coluna
xx: diâmetro nominal da coluna
- POSIÇÃO DO ITEM NA LISTA DE MATERIAIS

ABREVIações:

- BS - BACIA SANITÁRIA
- LV - LAVATÓRIO
- CH - CHUVEIRO
- TN - TANQUE
- MLR - MÁQUINA DE LAVAR ROUPAS
- MLL - MÁQUINA DE LAVAR LOUÇAS
- DU - DUCHA HIGIÊNICA
- CS - CAIXA SIFONADA
- RS - RALO SECO
- CGP - CAIXA DE GORDURA PEQUENA
- CI - CAIXA DE INSPEÇÃO

NOTAS:


- 1 - DIMENSÕES E DIÂMETROS EM MILÍMETROS, EXCETO ONDE INDICADO CONTRÁRIO.
- 2 - NOS TRECHOS HORIZONTAIS DAS TUBULAÇÕES DE ESGOTO SANITÁRIO RECOMENDAM-SE AS SEGUINTES DECLIVIDADES MÍNIMAS:
 - 2% PARA TUBULAÇÕES COM DIÂMETRO NOMINAL IGUAL OU INFERIOR A 75mm;
 - 1% PARA TUBULAÇÕES COM DIÂMETRO NOMINAL IGUAL OU SUPERIOR A 100mm.
- 3 - UTILIZAR ANÉIS DE BORRACHA NAS CONEXÕES DE ESGOTO.
- 4 - PROIBIDO UTILIZAR FOGO NAS TUBULAÇÕES.
- 5 - OS TERMINAIS DE VENTILAÇÃO DOS TUBOS DE VENTILAÇÃO DEVERÃO PASSAR 30CM ACIMA DO TELHADO.
- 6 - UTILIZAR DISPOSITIVO ANTI-ESPUMA NA CAIXA SIFONADA DA ÁREA DE SERVIÇO.
- 7 - TODAS AS TUBULAÇÕES EXPOSTAS DEVERÃO SER FIXADAS COM BRAÇADEIRA

Lista de Materiais - Conexões e Acessórios	
Descrição do Material	Quantidade
	218
Anel de Borracha, DN50mm, para linha de PVC Rígido Branco Série Normal, conforme NBR 5688	48
Anel de Borracha, DN100mm, para linha de PVC Rígido Branco Série Normal, conforme NBR 5688	17
Antespuma para instalação em Caixa Sifonada DN100mm, Esgoto	2
Bucha de Redução, DN50x40mm, de PVC Rígido Branco Série Normal para Esgoto e Água Pluvial, conforme NBR 5688	4
Caixa Sifonada Girafácil Montada com Grelha e Porta Grelha Quadrados Brancos 100x140x50mm, 5 Entradas, Esgoto	2
Joelho 45°, DN40mm, de PVC Rígido Branco Série Normal, conforme NBR 5688	1
Joelho 45°, DN50mm, de PVC Rígido Branco Série Normal, conforme NBR 5688	3
Joelho 90° com anel, DN40mm, de PVC Rígido Branco Série Normal, conforme NBR 5688	2
Joelho 90°, DN40mm, de PVC Rígido Branco Série Normal, conforme NBR 5688	2
Joelho 90°, DN50mm, de PVC Rígido Branco Série Normal, conforme NBR 5688	15
Joelho 90°, DN100mm, de PVC Rígido Branco Série Normal, conforme NBR 5688	5
Junção 45°, DN50x50mm, de PVC Rígido Branco Série Normal, conforme NBR 5688	3
Luva Simples, DN50mm, de PVC Rígido Branco Série Normal, conforme NBR 5688	21
Luva Simples, DN100mm, de PVC Rígido Branco Série Normal, conforme NBR 5688	12
Tê 90° de Redução, DN100x50mm, de PVC Rígido Branco Série Normal, conforme NBR 5688	5


Lista de Materiais - Tubos		
Descrição do Material	Diâmetro Nominal (mm)	Comprimento (m)
Tubo de PVC Rígido Branco, conforme NBR5688, Linha Série Normal	Ø100	44,28
Tubo de PVC Rígido Branco, conforme NBR5688, Linha Série Normal	Ø50	20,66
Tubo de PVC Rígido Branco, conforme NBR5688, Linha Série Normal	Ø40	2,37




PENN & WIZE
INSTALAÇÕES PREDIAIS
<https://pennwize.github.io/>

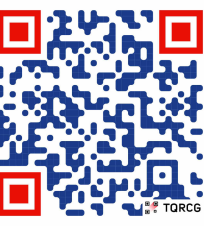


PROJETO:	Edifício Derry and Georgie	FOLHA:	E04
LOCAL:	Rua dos bobos, nº 0. Natal/RN - Brasil	REV.:	
ASSUNTO:	Cozinhas Tipo	ESCALA:	Como indicada
AUTORES DO PROJETO:	Amanda João Pedro Melo e Letícia Tórres	DATA:	12/02/2026

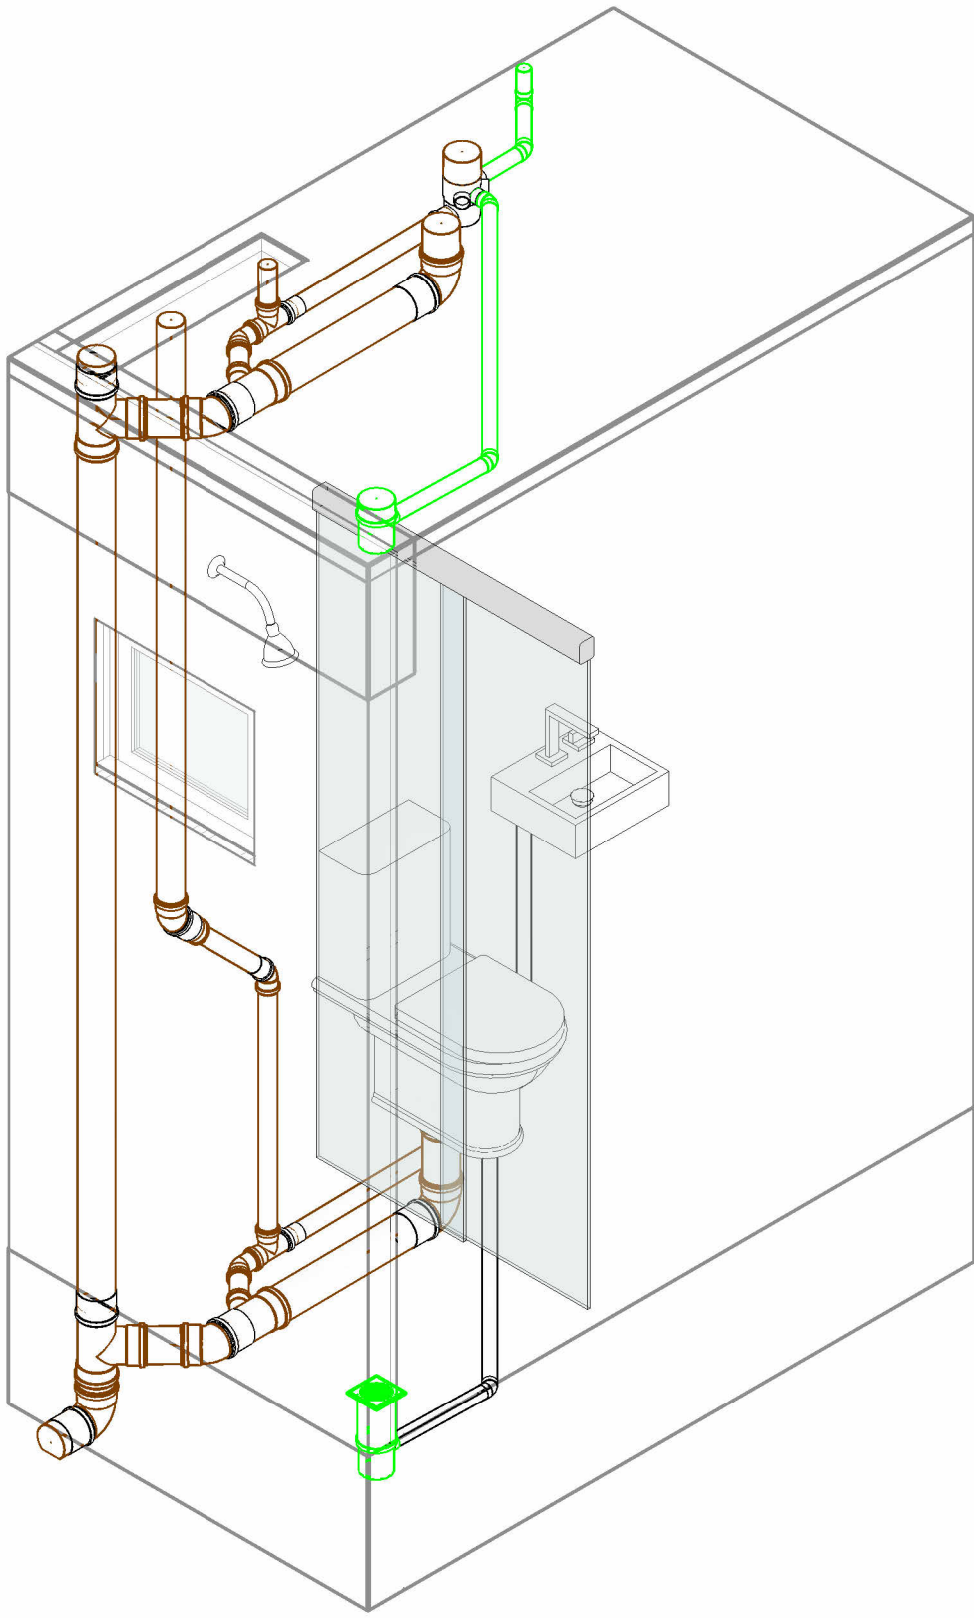

ISO - Banheiro 1

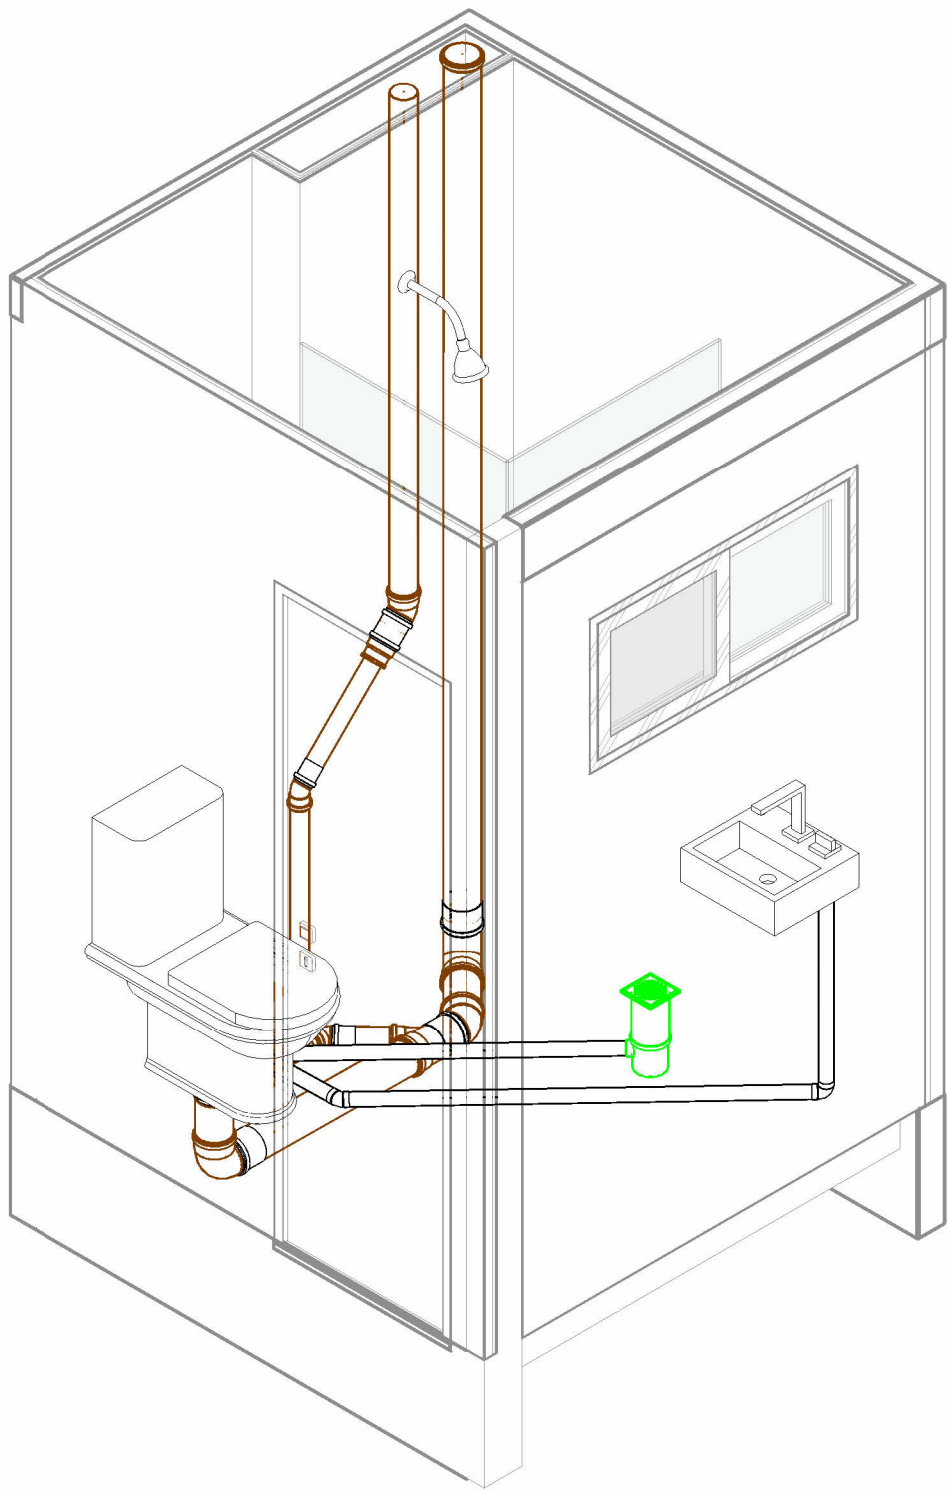


ISO - Banheiro 2

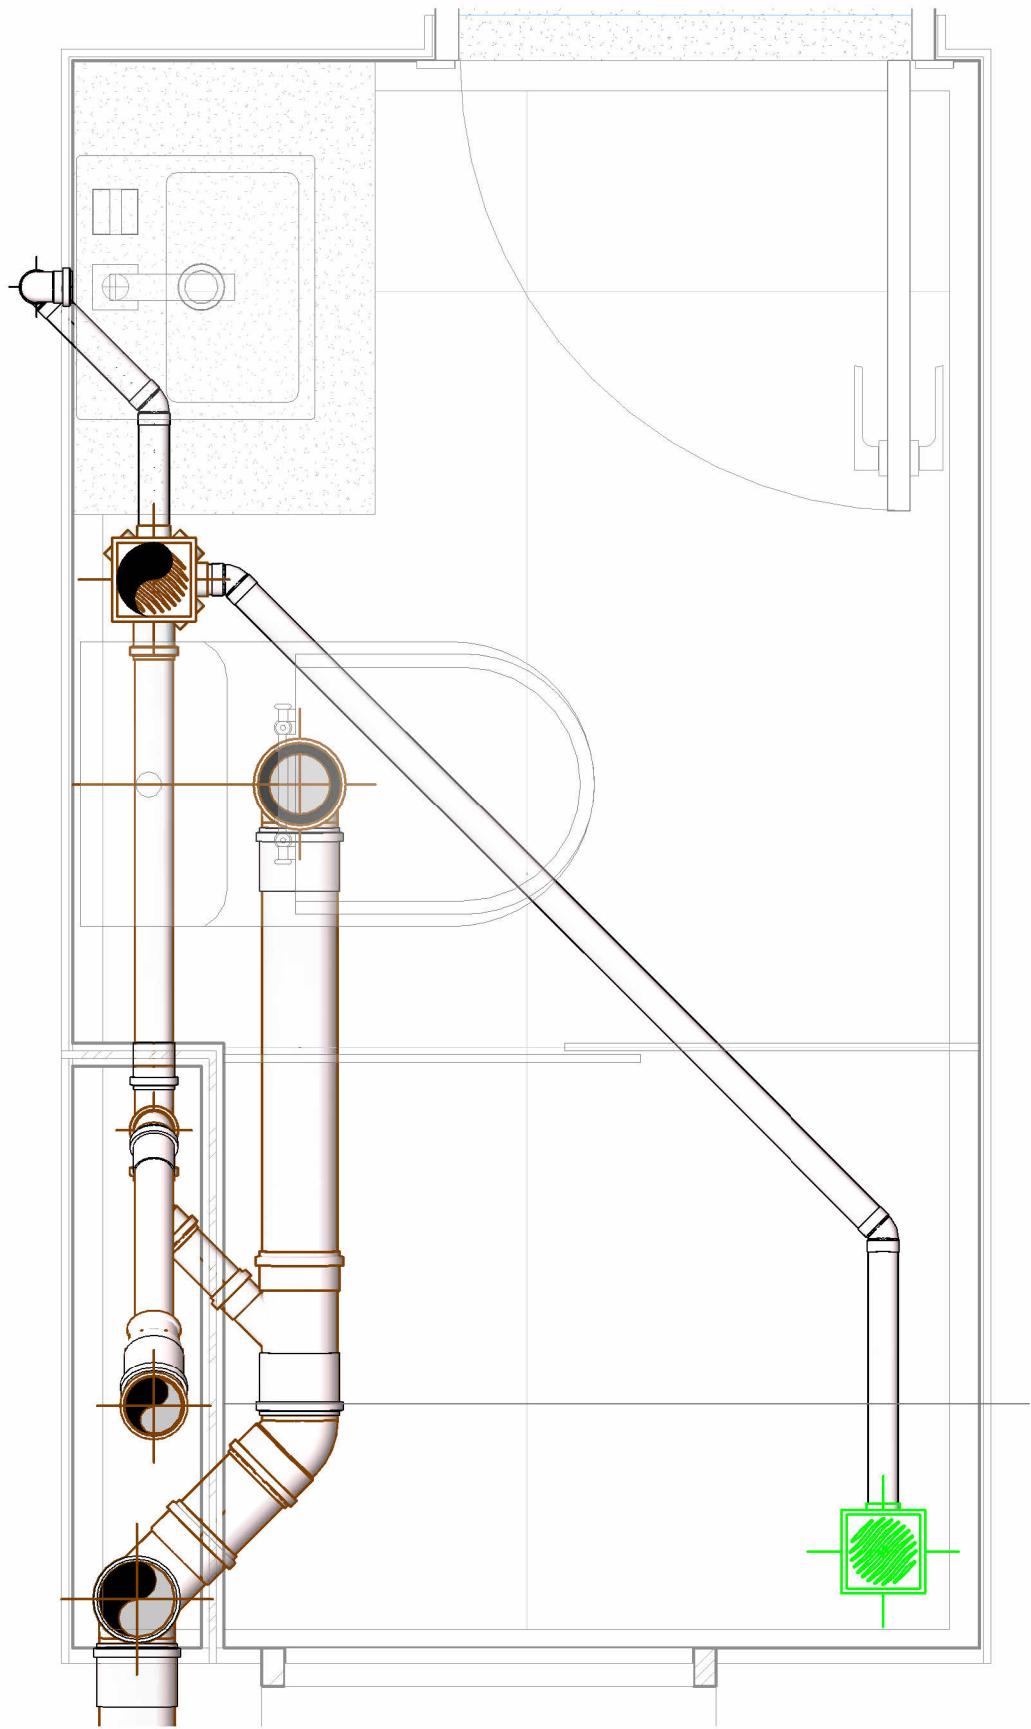

Banheiro 1

1 : 10

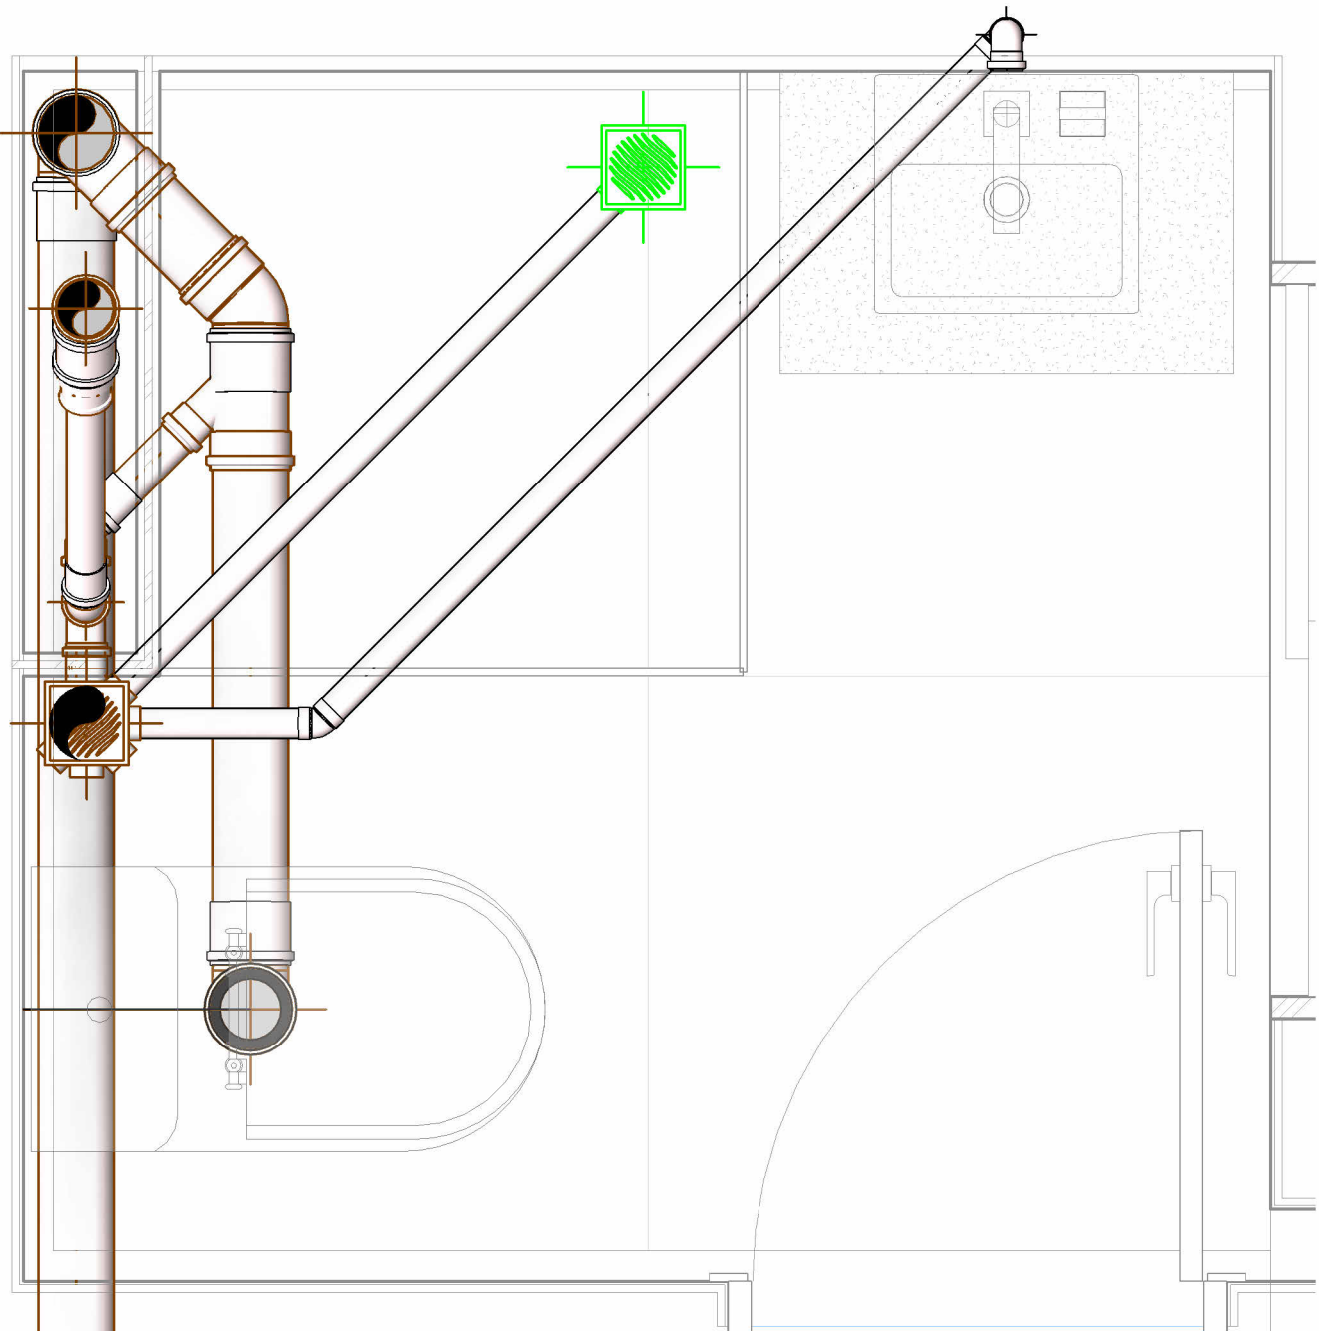

Banheiro 2

1 : 10

LEGENDA:

- TUBULAÇÃO PVC BRANCO SN - ESGOTO PRIMÁRIO
- TUBULAÇÃO PVC BRANCO SN - ESGOTO SECUNDÁRIO
- TUBULAÇÃO PVC BRANCO SN - VENTILAÇÃO ESGOTO
- TUBULAÇÃO PVC BRANCO SN - ESGOTO COM GORDURA

- TUBO DE QUEDA DE ESGOTO PRIMÁRIO
nn: numero da coluna
xx: diâmetro nominal da coluna
- COLUNA DE VENTILAÇÃO
nn: numero da coluna
xx: diâmetro nominal da coluna
- TUBO DE QUEDA DE GORDURA
nn: numero da coluna
xx: diâmetro nominal da coluna
- POSIÇÃO DO ITEM NA LISTA DE MATERIAIS

ABREVIações:

- BS - BACIA SANITÁRIA
- LV - LAVATÓRIO
- CH - CHUVEIRO
- TN - TANQUE
- MLR - MÁQUINA DE LAVAR ROUPAS
- MLL - MÁQUINA DE LAVAR LOUÇAS
- DU - DUCHA HIGIÊNICA
- CS - CAIXA SIFONADA
- RS - RALO SECO
- CGP - CAIXA DE GORDURA PEQUENA
- CI - CAIXA DE INSPEÇÃO

NOTAS:


- DIMENSÕES E DIÂMETROS EM MILÍMETROS, EXCETO ONDE INDICADO CONTRÁRIO.
- NOS TRECHOS HORIZONTAIS DAS TUBULAÇÕES DE ESGOTO SANITÁRIO RECOMENDAM-SE AS SEGUINTE DECLIVIDADES MÍNIMAS:
 - 2% PARA TUBULAÇÕES COM DIÂMETRO NOMINAL IGUAL OU INFERIOR A 75mm;
 - 1% PARA TUBULAÇÕES COM DIÂMETRO NOMINAL IGUAL OU SUPERIOR A 100mm.
- UTILIZAR ANÉIS DE BORRACHA NAS CONEXÕES DE ESGOTO.
- PROIBIDO UTILIZAR FOGO NAS TUBULAÇÕES.
- OS TERMINAIS DE VENTILAÇÃO DOS TUBOS DE VENTILAÇÃO DEVERÃO PASSAR 30CM ACIMA DO TELHADO.
- UTILIZAR DISPOSITIVO ANTI-ESPUMA NA CAIXA SIFONADA DA ÁREA DE SERVIÇO.
- TODAS AS TUBULAÇÕES EXPOSTAS DEVERÃO SER FIXADAS COM BRAÇADEIRA

Lista de Materiais - Conexões e Acessórios	
Descrição do Material	Quantidade
	de
	257
Adaptador para Saída de Vaso Sanitário, DN100mm, de PVC Rígido Branco Série Normal, conforme NBR 5688	3
Anel de Borracha, DN50mm, para linha de PVC Rígido Branco Série Normal, conforme NBR 5688	22
Anel de Borracha, DN75mm, para linha de PVC Rígido Branco Série Normal, conforme NBR 5688	5
Anel de Borracha, DN100mm, para linha de PVC Rígido Branco Série Normal, conforme NBR 5688	28
Caixa Sifonada Girafácil Montada com Grelha e Porta Grelha Quadrados Brancos 100x140x50mm, 5 Entradas, Esgoto	3
INEXISTENTE	2
Joelho 45°, DN40mm, de PVC Rígido Branco Série Normal, conforme NBR 5688	7
Joelho 45°, DN50mm, de PVC Rígido Branco Série Normal, conforme NBR 5688	5
Joelho 45°, DN75mm, de PVC Rígido Branco Série Normal, conforme NBR 5688	2
Joelho 45°, DN100mm, de PVC Rígido Branco Série Normal, conforme NBR 5688	3
Joelho 90° com anel, DN40mm, de PVC Rígido Branco Série Normal, conforme NBR 5688	2
Joelho 90°, DN40mm, de PVC Rígido Branco Série Normal, conforme NBR 5688	3
Joelho 90°, DN100mm, de PVC Rígido Branco Série Normal, conforme NBR 5688	5
Junção 45° de Redução, DN100x50mm, de PVC Rígido Branco Série Normal, conforme NBR 5688	3
Luva Simples, DN50mm, de PVC Rígido Branco Série Normal, conforme NBR 5688	5
Luva Simples, DN75mm, de PVC Rígido Branco Série Normal, conforme NBR 5688	3
Luva Simples, DN100mm, de PVC Rígido Branco Série Normal, conforme NBR 5688	11
Raio Seco Montado com Grelha e Porta Grelha Quadrados 100x100x40mm, Esgoto	3
Tê 90°, DN50x50mm, de PVC Rígido Branco Série Normal, conforme NBR 5688	3
Tê 90°, DN100x100mm, de PVC Rígido Branco Série Normal, conforme NBR 5688	4


Lista de Materiais - Tubos		
Descrição do Material	Diâmetro Nominal (mm)	Comprimento (m)
Tubo de PVC Rígido Branco, conforme NBR5688, Linha Série Normal	Ø100	22,52
Tubo de PVC Rígido Branco, conforme NBR5688, Linha Série Normal	Ø75	6,41
Tubo de PVC Rígido Branco, conforme NBR5688, Linha Série Normal	Ø50	5,57
Tubo de PVC Rígido Branco, conforme NBR5688, Linha Série Normal	Ø40	9,17



PENN & WIZE
INSTALAÇÕES PREDIAIS
<https://pennwize.github.io/>

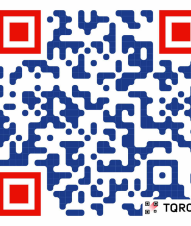


PROJETO:	Edifício Derry and Georgie	FOLHA:	E05
LOCAL:	Rua dos bobos, nº 0. Natal/RN - Brasil	REV.:	
ASSUNTO:	Banheiros Tipo	ESCALA:	Como indicada
AUTORES DO PROJETO:	Amanda João Pedro Melo e Letícia Tórres	DATA:	12/02/2026

 


Terminal de Ventilação Banheiro Salão de Festas

1 : 10

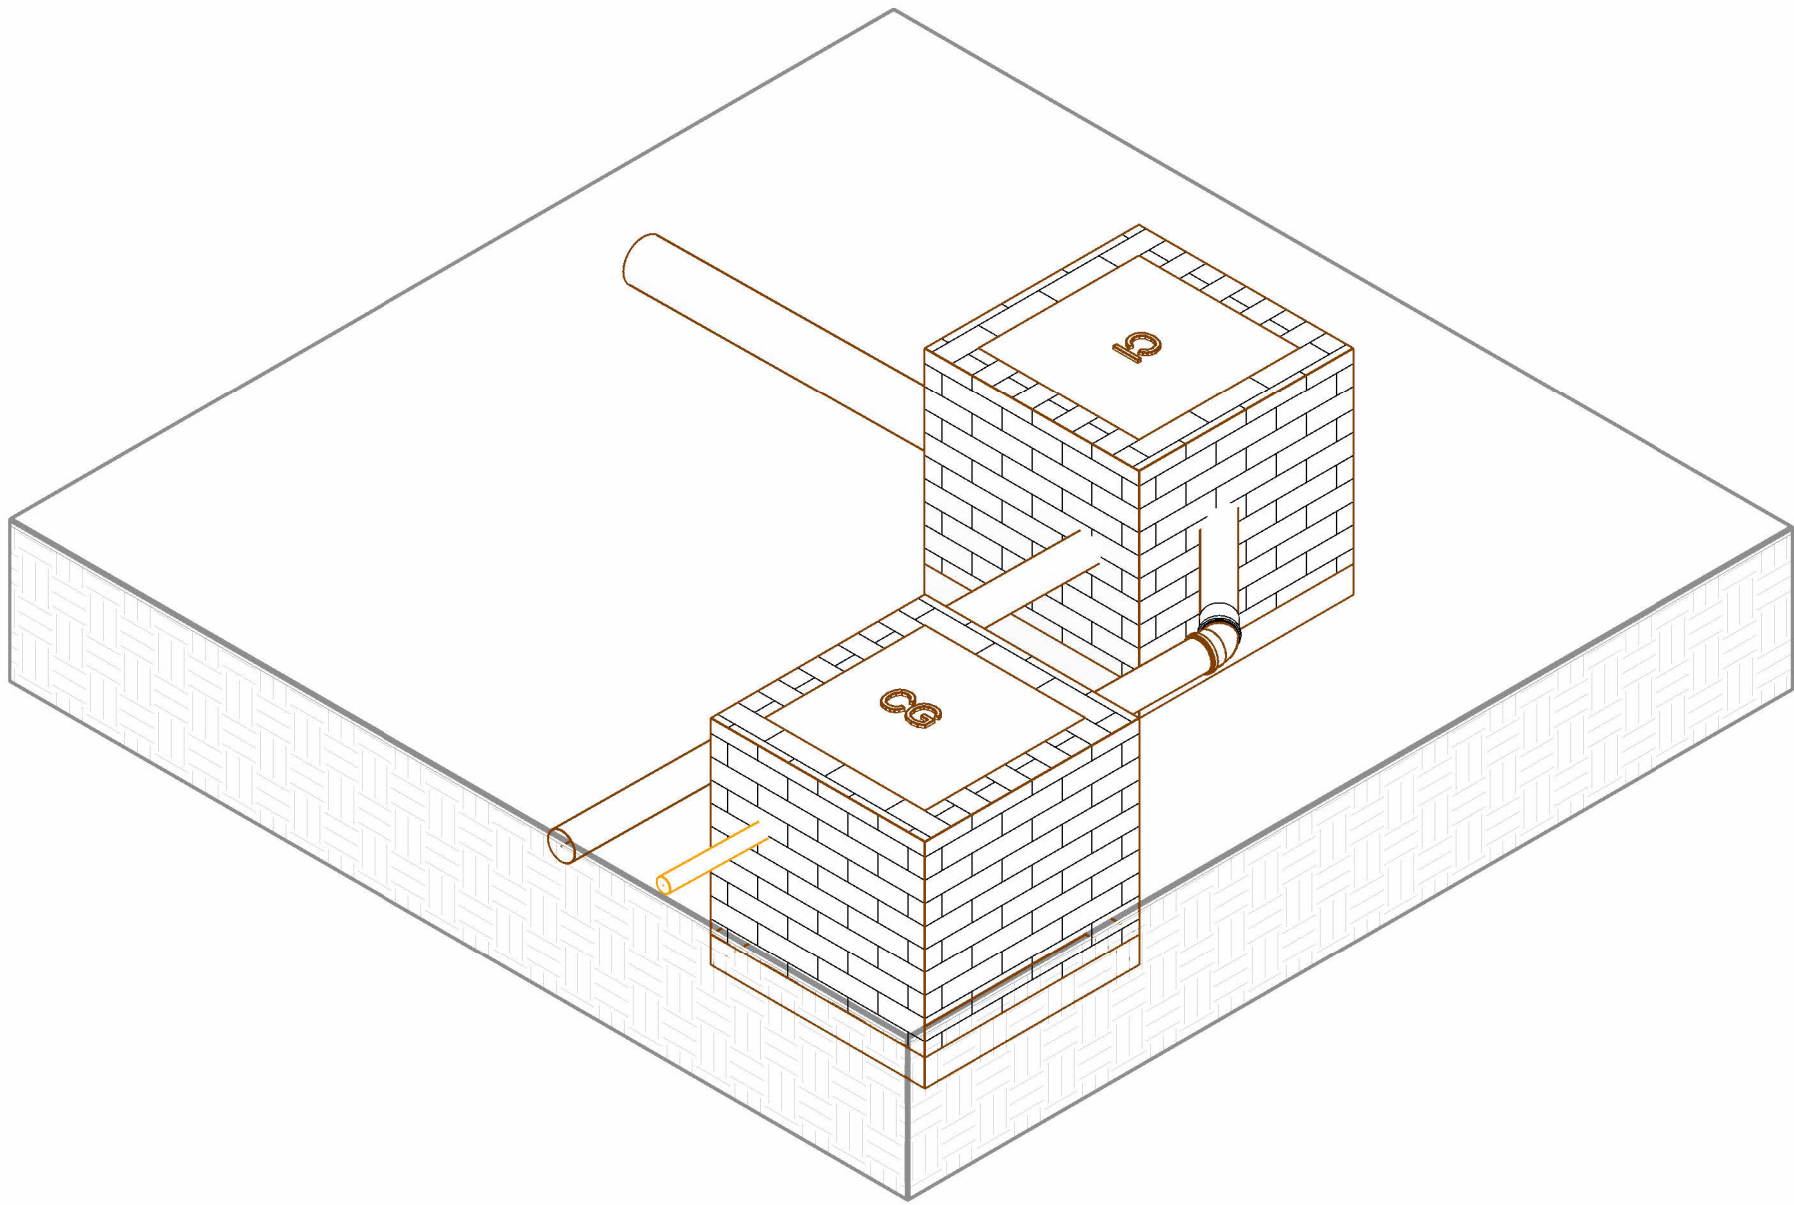

ISO - Caixa de Gordura e Inspeção

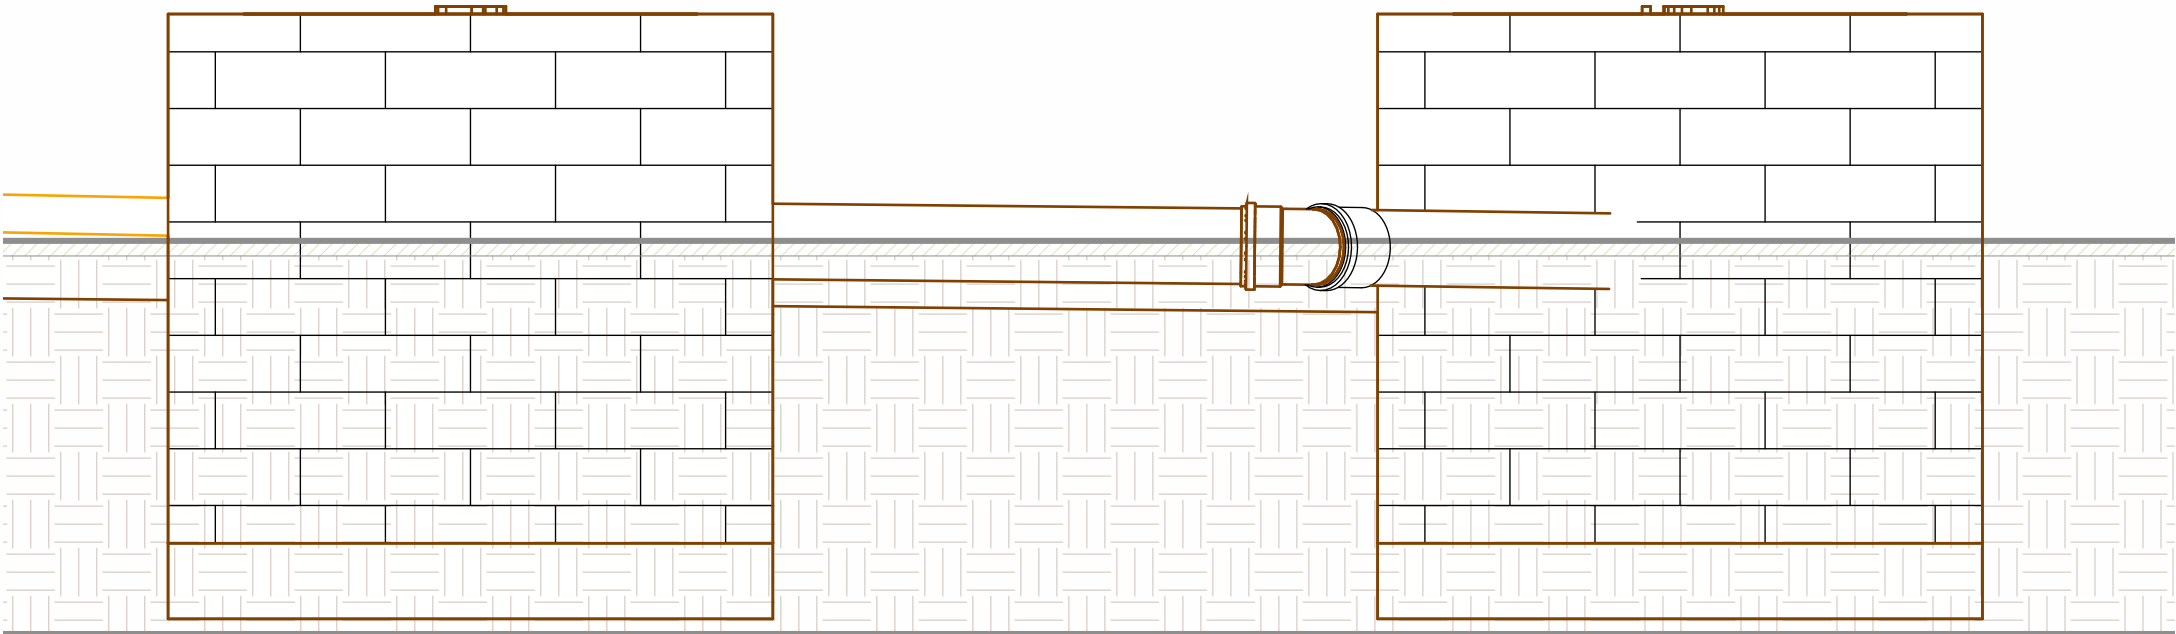

Caixa de Gordura e Inspeção

1 : 10

LEGENDA:

- TUBULAÇÃO PVC BRANCO SN - ESGOTO PRIMÁRIO
- TUBULAÇÃO PVC BRANCO SN - ESGOTO SECUNDÁRIO
- TUBULAÇÃO PVC BRANCO SN - VENTILAÇÃO ESGOTO
- TUBULAÇÃO PVC BRANCO SN - ESGOTO COM GORDURA

- TUBO DE QUEDA DE ESGOTO PRIMÁRIO
- COLUNA DE VENTILAÇÃO
- TUBO DE QUEDA DE GORDURA
- POSIÇÃO DO ITEM NA LISTA DE MATERIAIS

ABREVIACOES:

- BS - BACIA SANITARIA
- LV - LAVATORIO
- CH - CHUVEIRO
- TN - TANQUE
- MLR - MAQUINA DE LAVAR ROUPAS
- MLL - MAQUINA DE LAVAR LOUCAS
- DU - DUCHA HIGIENICA
- CS - CAIXA SIFONADA
- RS - RALO SECO
- CGP - CAIXA DE GORDURA PEQUENA
- CI - CAIXA DE INSPECÃO

NOTAS:


- 1 - DIMENSÖES E DIÁMETROS EM MILIMETROS, EXCETO ONDE INDICADO CONTRÁRIO.
- 2 - NOS TRECHOS HORIZONTAIS DAS TUBULAÇÕES DE ESGOTO SANITÁRIO RECOMENDAM-SE AS SEGUINTES DECLIVIDADES MINIMAS:
 - 2% PARA TUBULAÇÕES COM DIÁMETRO NOMINAL IGUAL OU INFERIOR A 75mm;
 - 1% PARA TUBULAÇÕES COM DIÁMETRO NOMINAL IGUAL OU SUPERIOR A 100mm.
- 3 - UTILIZAR ANEIS DE BORRACHA NAS CONEXÖES DE ESGOTO.
- 4 - PROIBIDO UTILIZAR FOGO NAS TUBULAÇÕES.
- 5 - OS TERMINAIS DE VENTILAÇÃO DOS TUBOS DE VENTILAÇÃO DEVERÃO PASSAR 30CM ACIMA DO TELHADO.
- 6 - UTILIZAR DISPOSITIVO ANTI-ESPUMA NA CAIXA SIFONADA DA ÁREA DE SERVIÇO.
- 7 - TODAS AS TUBULAÇÕES EXPOSTAS DEVERÃO SER FIXADAS COM BRAÇADEIRA

Lista de Materiais - Conexões e Acessórios	
Descrição do Material	Quantidade
	7
Anel de Borracha, DN100mm, para linha de PVC Rígido Branco Série Normal, conforme NBR 5688	2
Caixa de inspeção em alvenaria com tampa de concreto, 60x60cm	2
Joelho 45°, DN100mm, de PVC Rígido Branco Série Normal, conforme NBR 5688	1
Luva Simples, DN100mm, de PVC Rígido Branco Série Normal, conforme NBR 5688	1
Terminal de Ventilação, DN50mm, de PVC Rígido Branco Série Normal, conforme NBR 5688	2
Esgoto Sanitário	
Anel de Borracha, DN100mm, para linha de PVC Rígido Branco Série Normal, conforme NBR 5688	3
Luva Simples, DN100mm, de PVC Rígido Branco Série Normal, conforme NBR 5688	1
Tê 90°, DN100x100mm, de PVC Rígido Branco Série Normal, conforme NBR 5688	1


Lista de Materiais - Tubos		
Descrição do Material	Diâmetro Nominal (mm)	Comprimento (m)
Tubo de PVC Rígido Branco, conforme NBR5688, Linha Série Normal	Ø150	18,54
Tubo de PVC Rígido Branco, conforme NBR5688, Linha Série Normal	Ø100	5,17
Tubo de PVC Rígido Branco, conforme NBR5688, Linha Série Normal	Ø50	9,52



PENN & WIZE
INSTALAÇÕES PREDIAIS
<https://pennwize.github.io/>

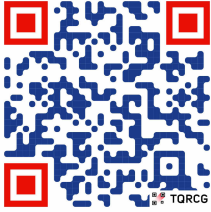


PROJETO:	Edifício Derry and Georgeie	FOLHA:	E06
LOCAL:	Rua dos bobos, nº 0. Natal/RN - Brasil	REV.:	
ASSUNTO:	Terminal de Ventilação, Caixa de Inspeção e Gordura	ESCALA:	Como indicada
AUTORES DO PROJETO:	Amanda João Pedro Melo e Letícia Tórres	DATA:	12/02/2026

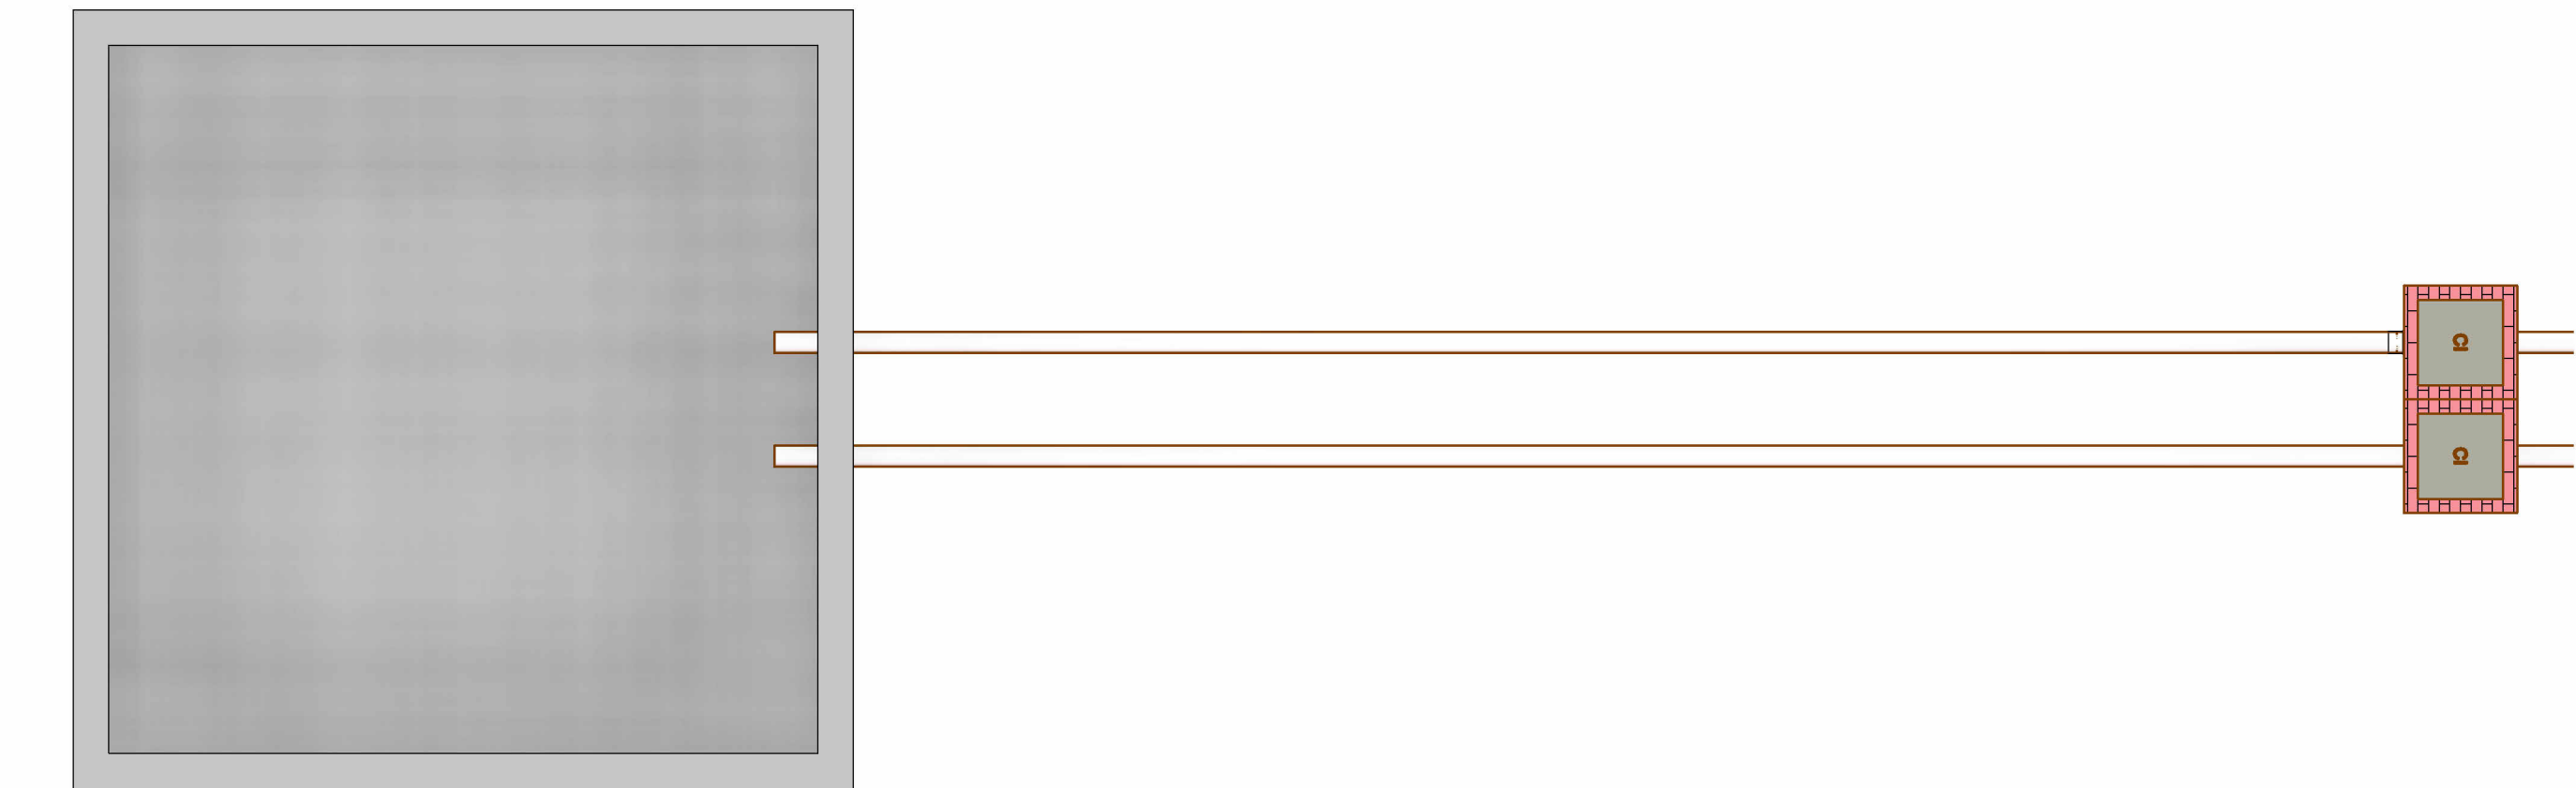

Espaço destinado à implantação de Estação de Tratamento de Esgoto

1 : 50

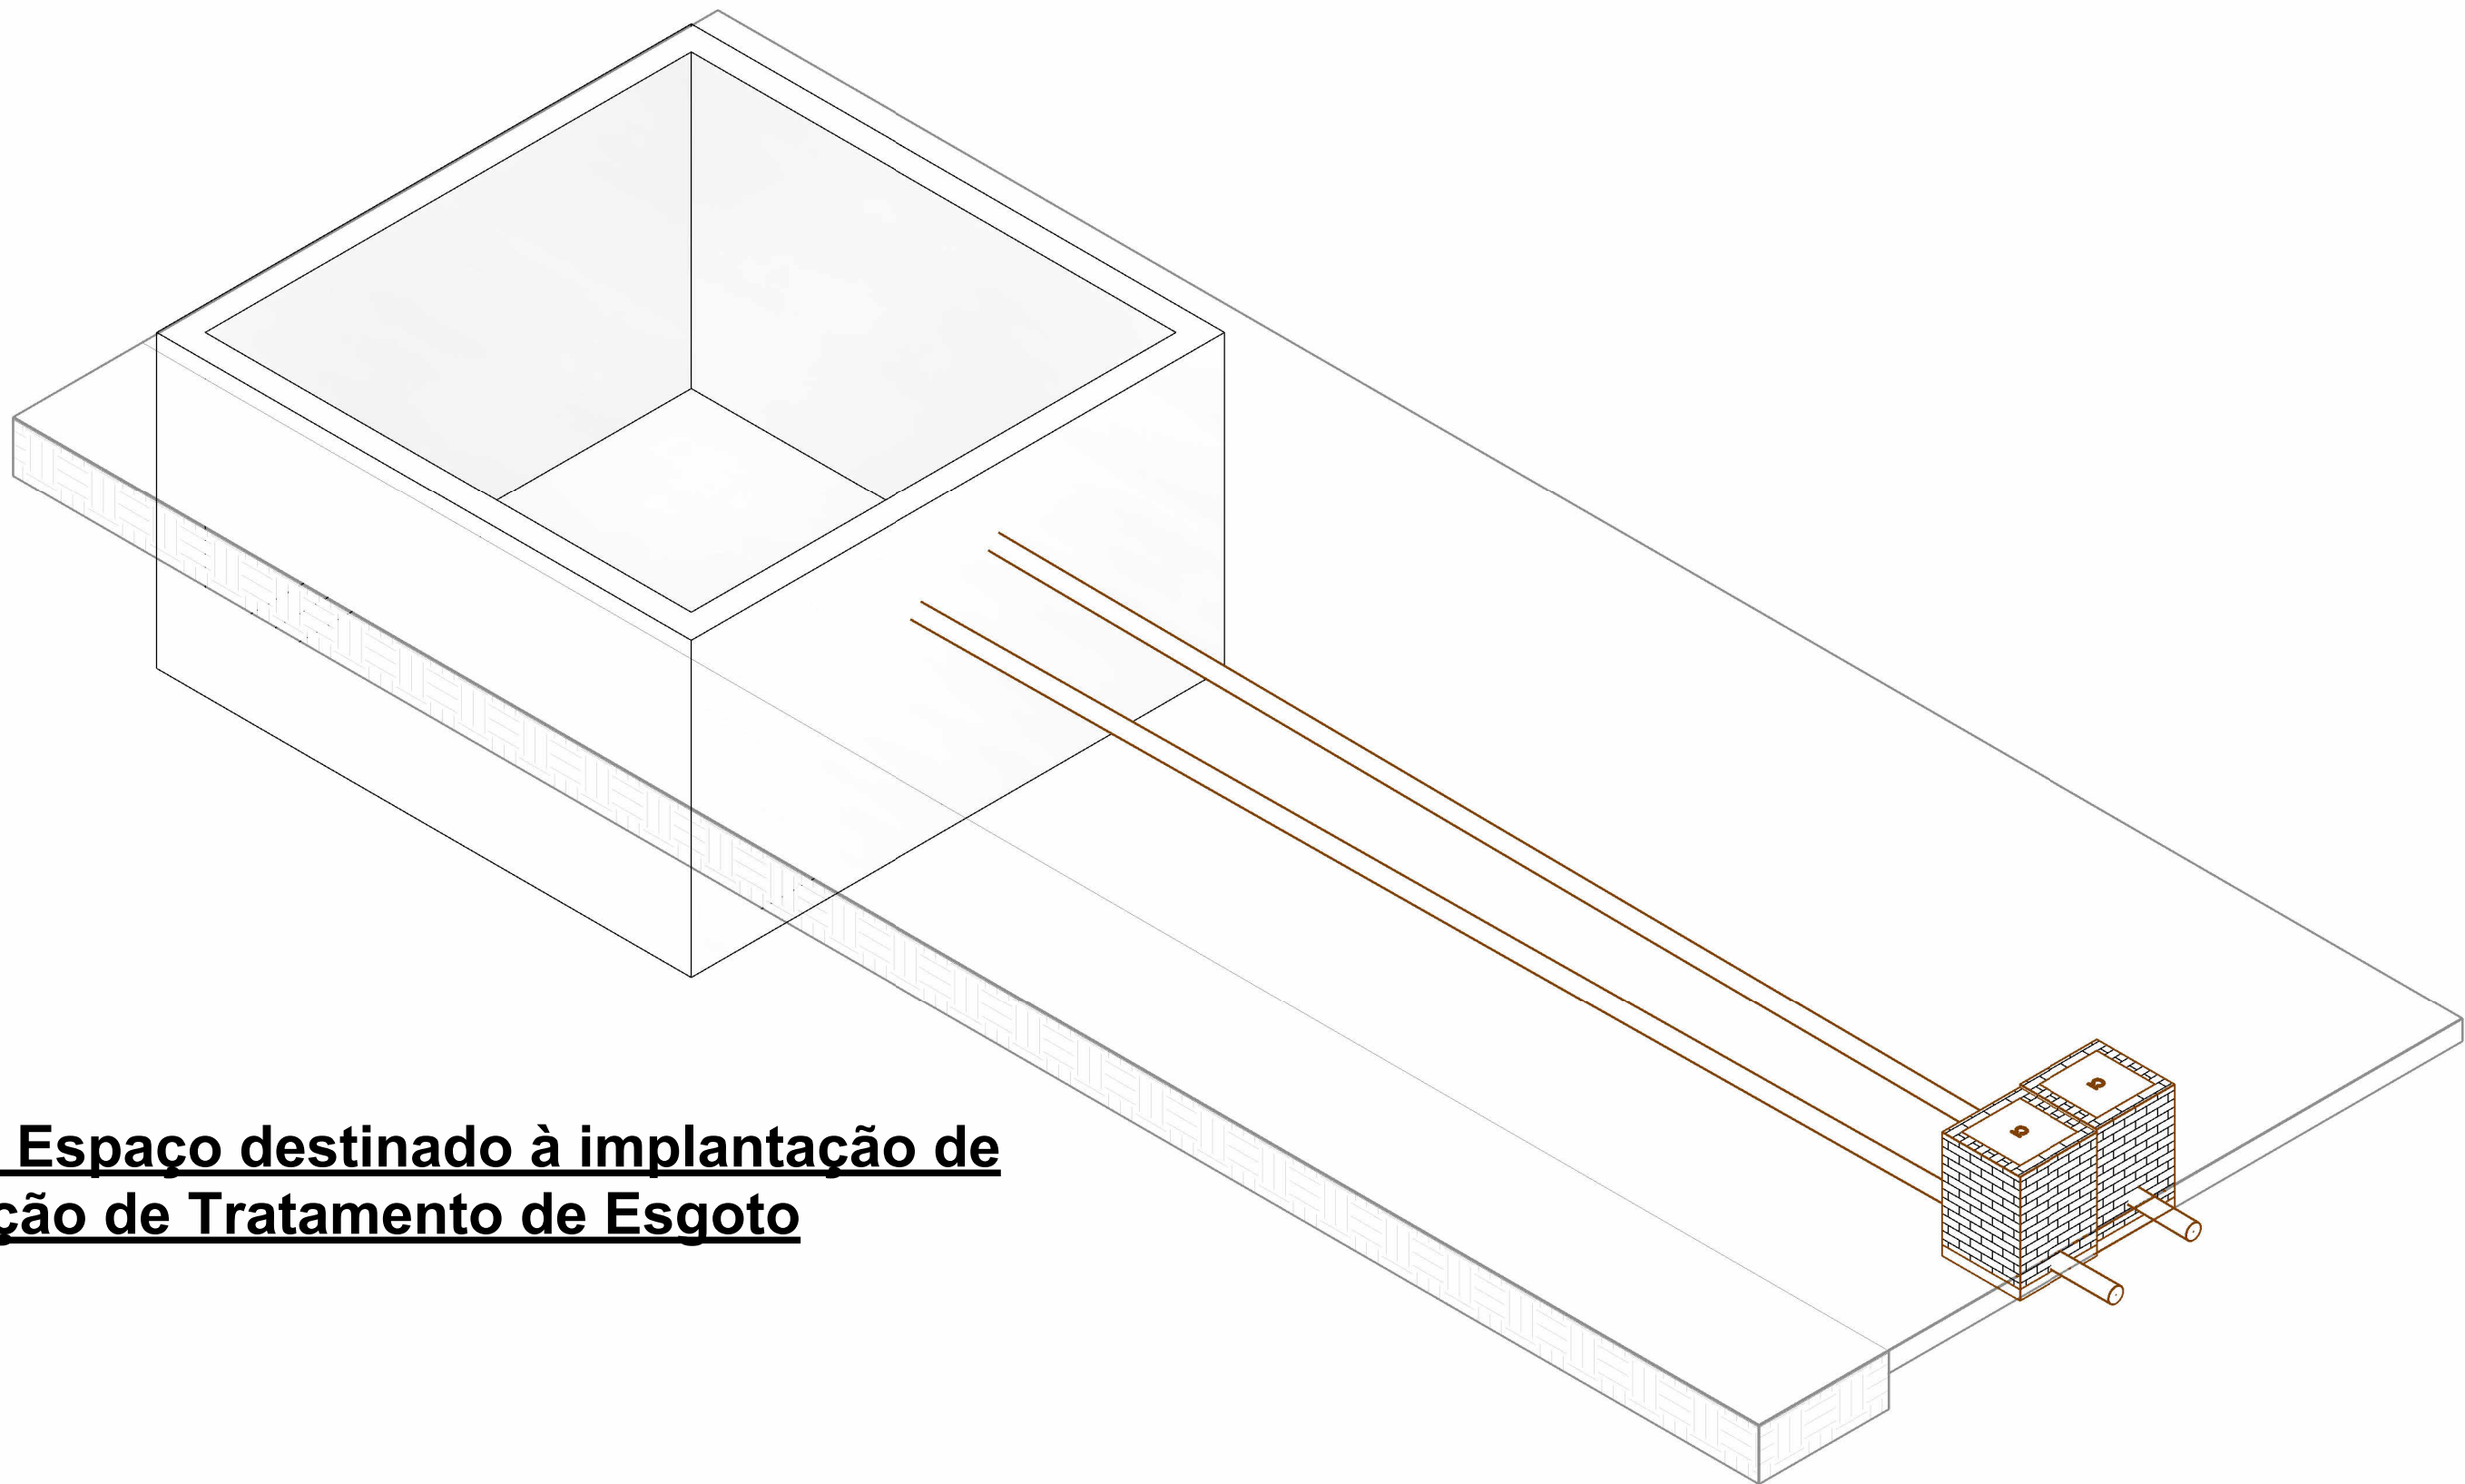

ISO - Espaço destinado à implantação de Estação de Tratamento de Esgoto

LEGENDA:

- TUBULAÇÃO PVC BRANCO SN - ESGOTO PRIMÁRIO
- TUBULAÇÃO PVC BRANCO SN - ESGOTO SECUNDÁRIO
- TUBULAÇÃO PVC BRANCO SN - VENTILAÇÃO ESGOTO
- TUBULAÇÃO PVC BRANCO SN - ESGOTO COM GORDURA

TG-nh
Øxx

-TUBO DE QUEDA DE ESGOTO PRIMÁRIO
nn: numero da coluna
xx: diâmetro nominal da coluna

CV-nh
Øxx

-COLUNA DE VENTILAÇÃO
nn: numero da coluna
xx: diâmetro nominal da coluna

TG-nh
Øxx

-TUBO DE QUEDA DE GORDURA
nn: numero da coluna
xx: diâmetro nominal da coluna

xx

-POSIÇÃO DO ITEM NA LISTA DE MATERIAIS

ABREVIações:

- BS - BACIA SANITÁRIA
- LV - LAVATÓRIO
- CH - CHUVEIRO
- TN - TANQUE
- MLR - MÁQUINA DE LAVAR ROUPAS
- MLL - MÁQUINA DE LAVAR LOUÇAS
- DU - DUCHA HIGIÊNICA
- CS - CAIXA SIFONADA
- RS - RALO SECO
- GCP - CAIXA DE GORDURA PEQUENA
- CI - CAIXA DE INSPEÇÃO

NOTAS:

- 1 - DIMENSÕES E DIÂMETROS EM MILÍMETROS, EXCETO ONDE INDICADO CONTRÁRIO.
- 2 - NOS TRECHOS HORIZONTAIS DAS TUBULAÇÕES DE ESGOTO SANITÁRIO RECOMENDAM-SE AS SEGUINTES DECLIVIDADES MÍNIMAS:
 - 2% PARA TUBULAÇÕES COM DIÂMETRO NOMINAL IGUAL OU INFERIOR A 75mm;
 - 1% PARA TUBULAÇÕES COM DIÂMETRO NOMINAL IGUAL OU SUPERIOR A 100mm.
- 3 - UTILIZAR ANÉIS DE BORRACHA NAS CONEXÕES DE ESGOTO.
- 4 - PROIBIDO UTILIZAR FOGO NAS TUBULAÇÕES.
- 5 - OS TERMINAIS DE VENTILAÇÃO DOS TUBOS DE VENTILAÇÃO DEVERÃO PASSAR 30CM ACIMA DO TELHADO.
- 6 - UTILIZAR DISPOSITIVO ANTI-ESPUMA NA CAIXA SIFONADA DA ÁREA DE SERVIÇO.
- 7 - TODAS AS TUBULAÇÕES EXPOSTAS DEVERÃO SER FIXADAS COM BRAÇADEIRA

Lista de Materiais - Conexões e Acessórios	
Descrição do Material	Quantidade
	de
	5
Anel de Borracha, DN100mm, para linha de PVC Rígido Branco Série Normal, conforme NBR 5688	1
Anel de Borracha, DN150mm, para linha de PVC Rígido Branco Série Normal, conforme NBR 5688	1
Caixa de inspeção em alvenaria com tampa de concreto, 60x60cm	2
Luva Simples, DN150mm, de PVC Rígido Branco Série Normal, conforme NBR 5688	1
Redução Excêntrica, DN150x100mm, de PVC Rígido Branco Série Normal para Esgoto e Água Pluvial, conforme NBR 5688	1


Lista de Materiais - Tubos		
Descrição do Material	Diâmetro Nominal (mm)	Comprimento (m)
Tubo de PVC Rígido Branco, conforme NBR5688, Linha Série Normal	Ø150	55,05




PENN & WIZE
INSTALAÇÕES PREDIAIS
<https://pennwize.github.io/>




PROJETO:	Edifício Derry and Georgie	FOLHA:	E07
LOCAL:	Rua dos bobos, nº 0. Natal/RN - Brasil	REV.:	
ASSUNTO:	Espaço destinado à implantação de Estação de Tratamento de Esgoto	ESCALA:	1 : 50
AUTORES DO PROJETO:	Amanda João Pedro Melo e Letícia Tórres	DATA:	12/02/2026

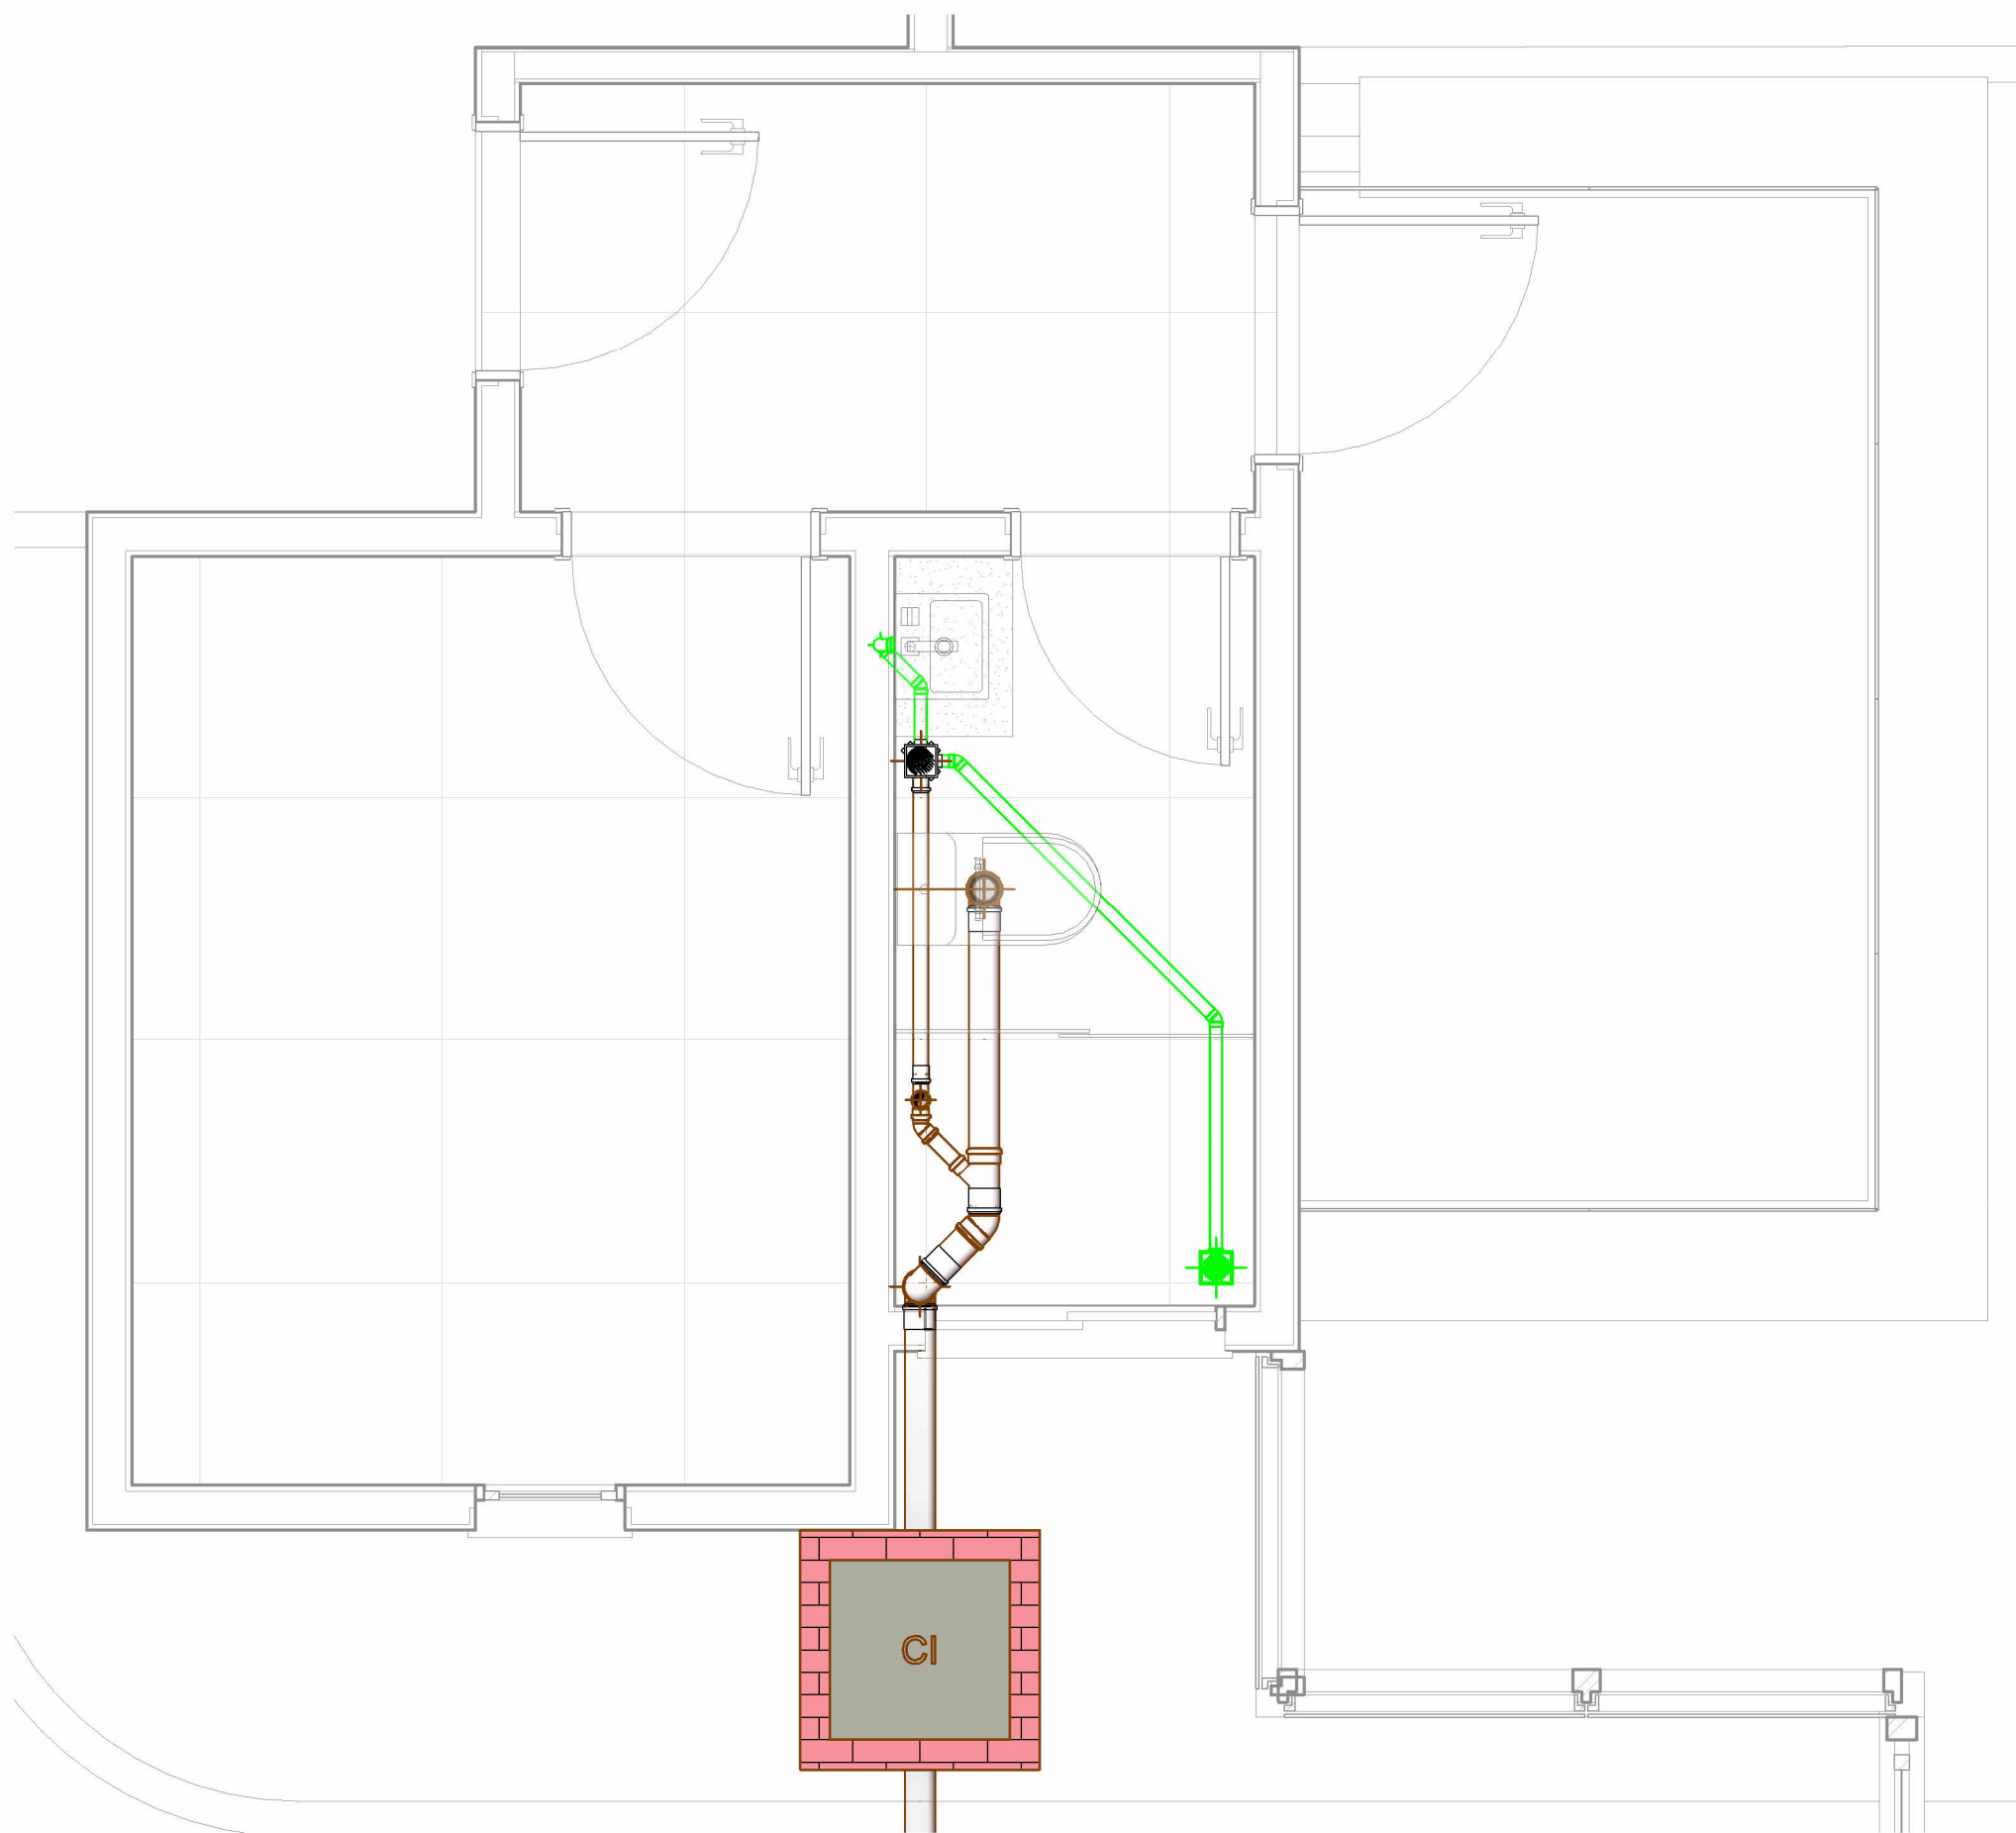

Guarita
1 : 25

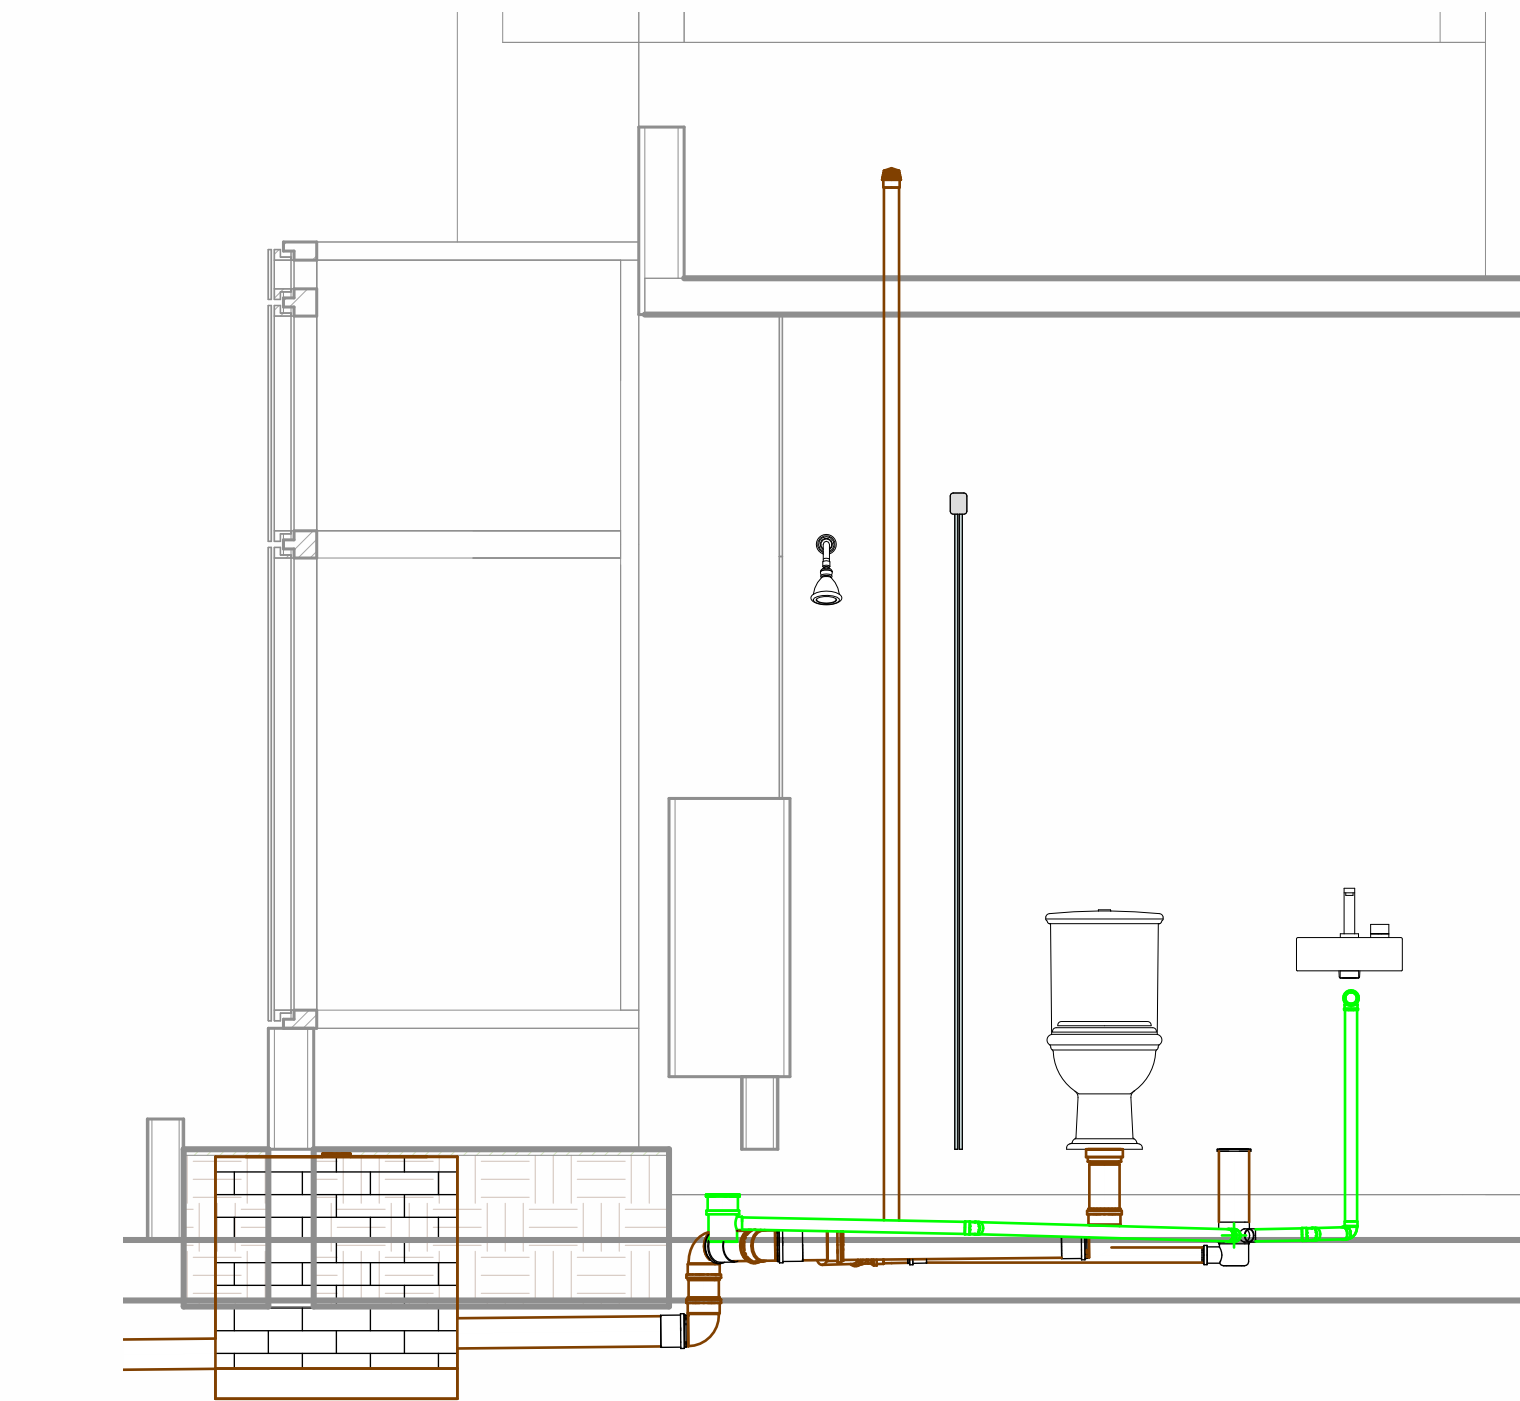

Guarita
1 : 25

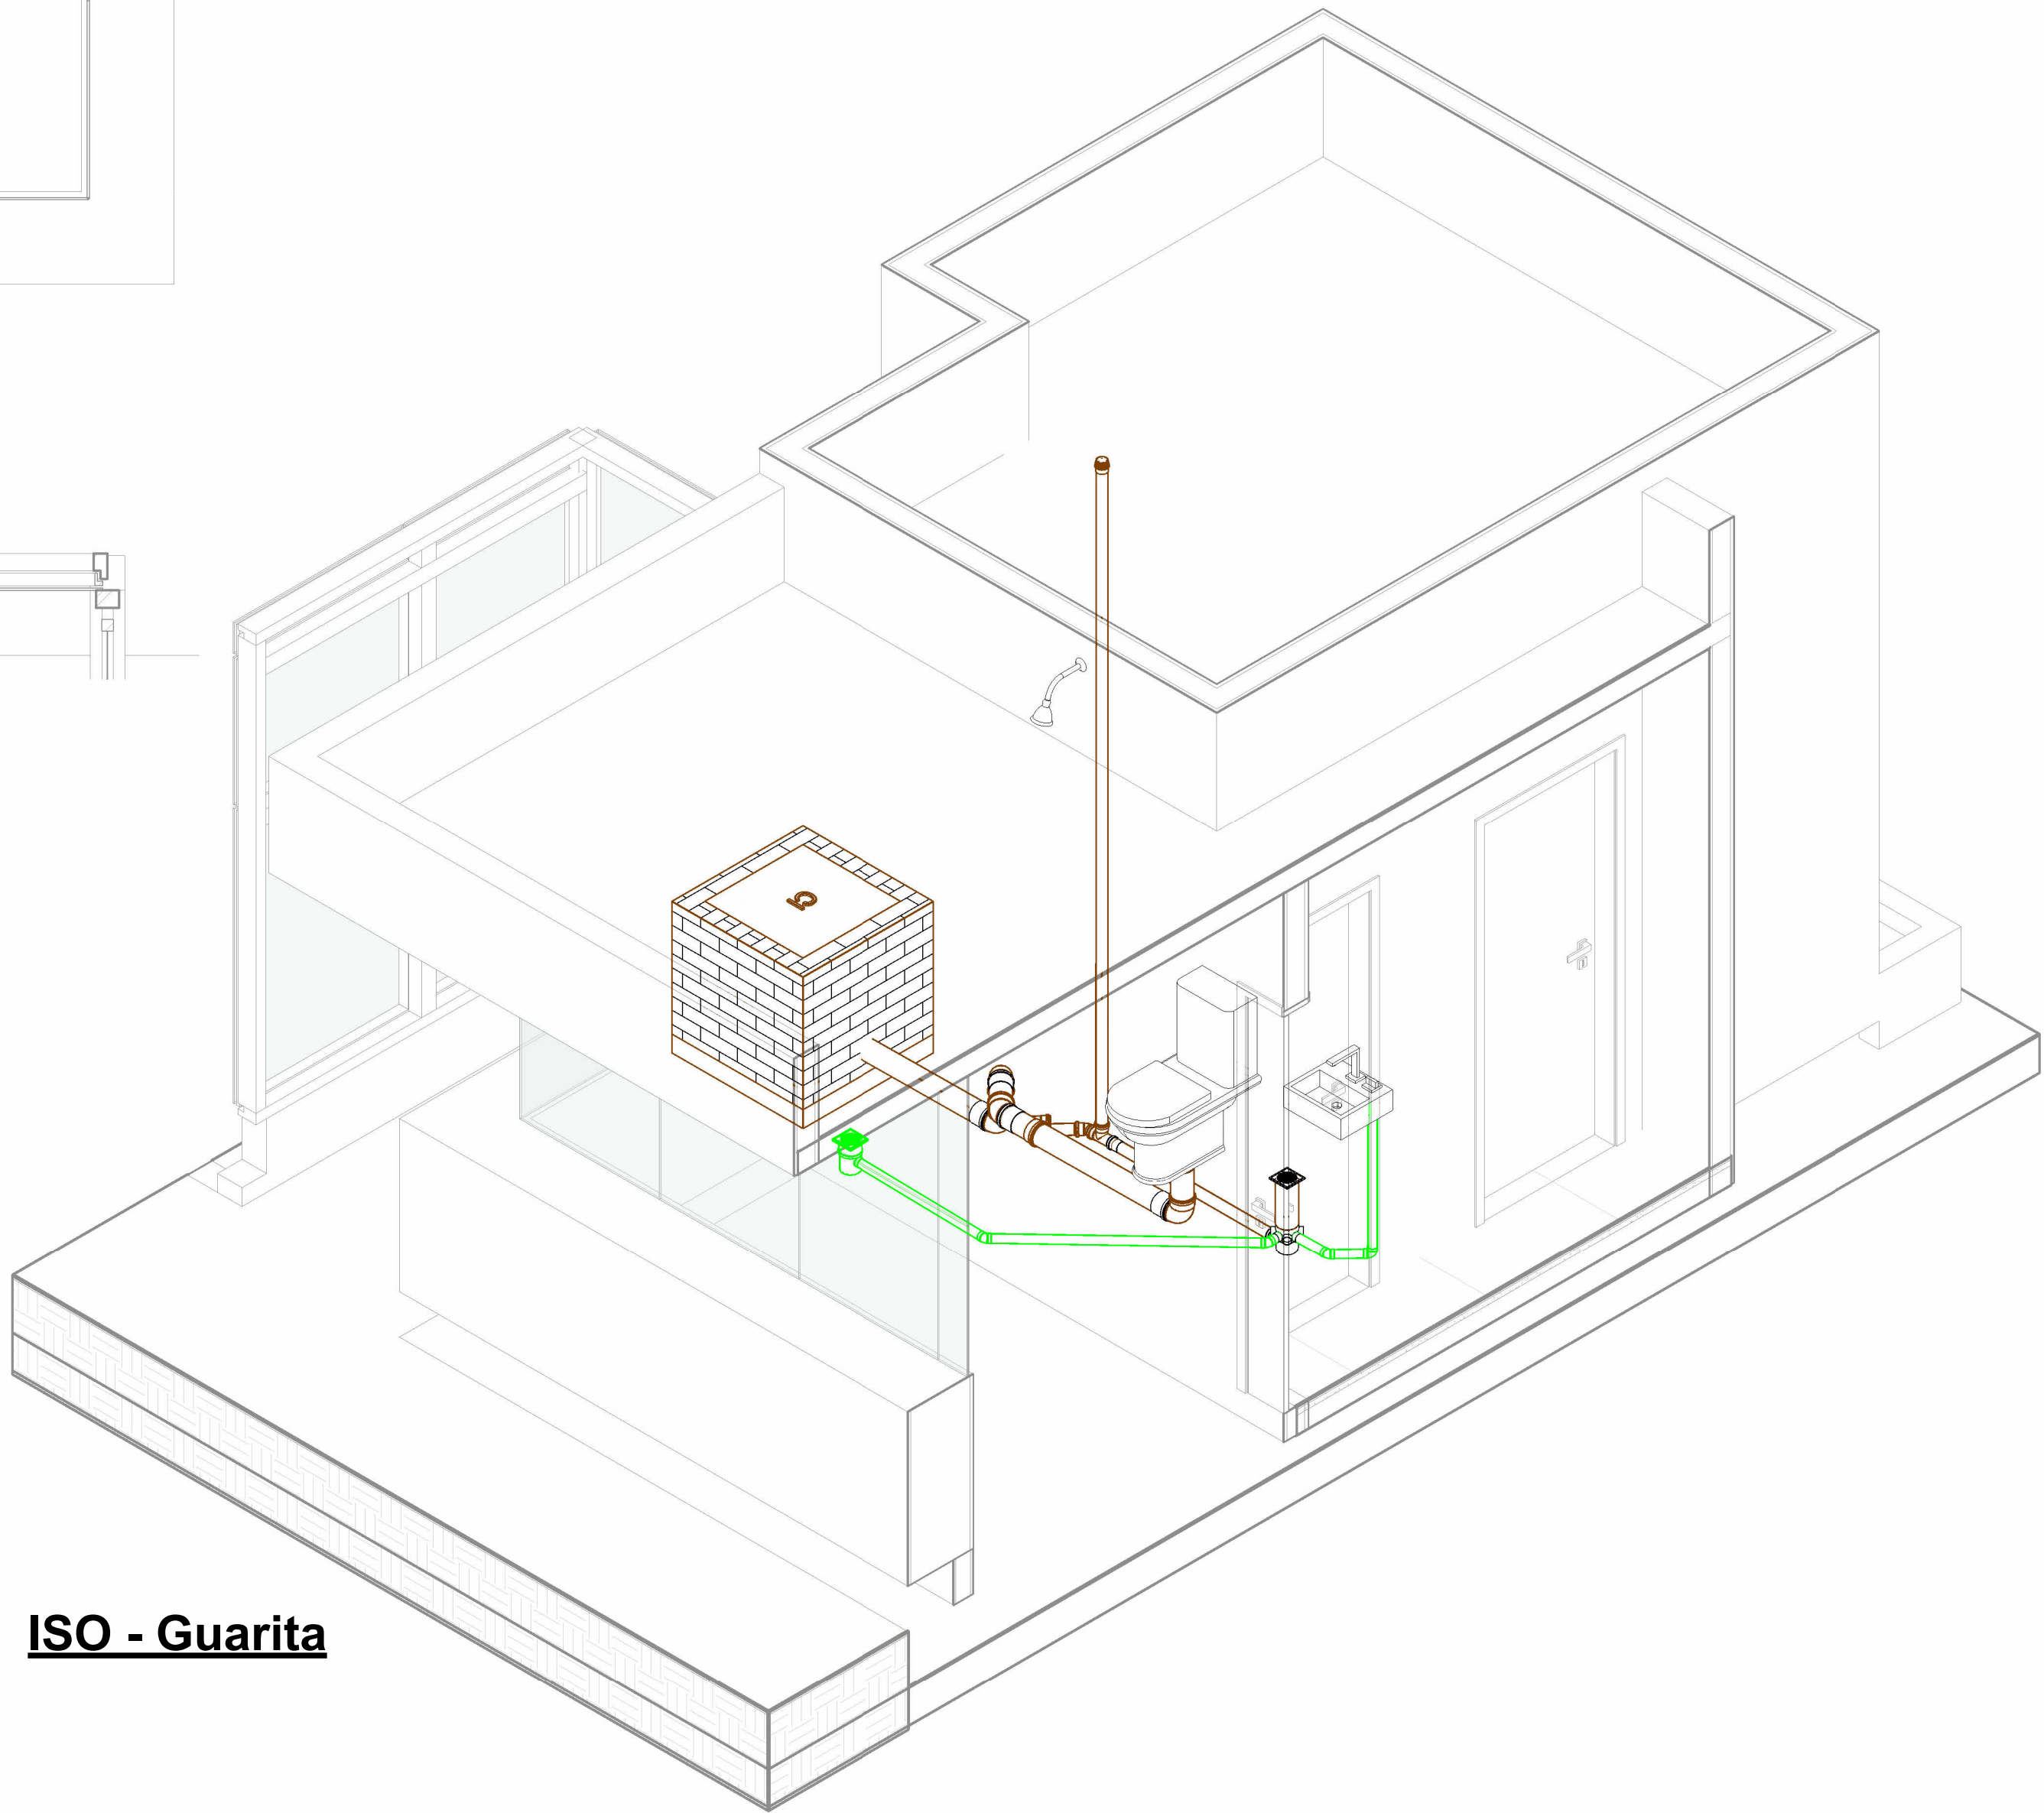

ISO - Guarita

LEGENDA:

- TUBULAÇÃO PVC BRANCO SN - ESGOTO PRIMÁRIO
- TUBULAÇÃO PVC BRANCO SN - ESGOTO SECUNDÁRIO
- TUBULAÇÃO PVC BRANCO SN - VENTILAÇÃO ESGOTO
- TUBULAÇÃO PVC BRANCO SN - ESGOTO COM GORDURA

TG-nh
Øxx
-TUBO DE QUEDA DE ESGOTO PRIMÁRIO
nh: número da coluna
xx: diâmetro nominal da coluna

CV-nh
Øxx
-COLUNA DE VENTILAÇÃO
nh: número da coluna
xx: diâmetro nominal da coluna

TG-nh
Øxx
-TUBO DE QUEDA DE GORDURA
nh: número da coluna
xx: diâmetro nominal da coluna

XX
-POSIÇÃO DO ITEM NA LISTA DE MATERIAIS

ABREVIações:

- BS - BACIA SANITÁRIA
- LV - LAVATÓRIO
- CH - CHUVEIRO
- TN - TANQUE
- MLR - MÁQUINA DE LAVAR ROUPAS
- MLL - MÁQUINA DE LAVAR LOUÇAS
- DU - DUCHA HIGIÊNICA
- CS - CAIXA SIFONADA
- RS - RALO SECO
- CGP - CAIXA DE GORDURA PEQUENA
- CI - CAIXA DE INSPEÇÃO

NOTAS:

- 1 - DIMENSÕES E DIÂMETROS EM MILÍMETROS, EXCETO ONDE INDICADO CONTRÁRIO.
- 2 - NOS TRECHOS HORIZONTAIS DAS TUBULAÇÕES DE ESGOTO SANITÁRIO RECOMENDAM-SE AS SEGUINTES DECLIVIDADES MÍNIMAS:
 - 2% PARA TUBULAÇÕES COM DIÂMETRO NOMINAL IGUAL OU INFERIOR A 75mm;
 - 1% PARA TUBULAÇÕES COM DIÂMETRO NOMINAL IGUAL OU SUPERIOR A 100mm.
- 3 - UTILIZAR ANÉIS DE BORRACHA NAS CONEXÕES DE ESGOTO.
- 4 - PROIBIDO UTILIZAR FOGO NAS TUBULAÇÕES.
- 5 - OS TERMINAIS DE VENTILAÇÃO DOS TUBOS DE VENTILAÇÃO DEVERÃO PASSAR 30CM ACIMA DO TELHADO.
- 6 - UTILIZAR DISPOSITIVO ANTI-ESPUMA NA CAIXA SIFONADA DA ÁREA DE SERVIÇO.
- 7 - TODAS AS TUBULAÇÕES EXPOSTAS DEVERÃO SER FIXADAS COM BRAÇADEIRA

Lista de Materiais - Conexões e Acessórios	
Descrição do Material	Quantidade
	de
	7
Adaptador para Saída de Vaso Sanitário, DN100mm, de PVC Rígido Branco Série Normal, conforme NBR 5688	1
Anel de Borracha, DN50mm, para linha de PVC Rígido Branco Série Normal, conforme NBR 5688	6
Anel de Borracha, DN100mm, para linha de PVC Rígido Branco Série Normal, conforme NBR 5688	9
Caixa de inspeção em alvenaria com tampa de concreto, 60x60cm	1
Caixa Sifonada Girafácil Montada com Grelha e Porta Grelha Quadrados Brancos 100x140x50mm, 5 Entradas, Esgoto	1
Joelho 45°, DN40mm, de PVC Rígido Branco Série Normal, conforme NBR 5688	3
Joelho 45°, DN50mm, de PVC Rígido Branco Série Normal, conforme NBR 5688	1
Joelho 45°, DN100mm, de PVC Rígido Branco Série Normal, conforme NBR 5688	1
Joelho 90° com anel, DN40mm, de PVC Rígido Branco Série Normal, conforme NBR 5688	1
Joelho 90°, DN40mm, de PVC Rígido Branco Série Normal, conforme NBR 5688	1
Joelho 90°, DN100mm, de PVC Rígido Branco Série Normal, conforme NBR 5688	3
Junção 45° de Redução, DN100x50mm, de PVC Rígido Branco Série Normal, conforme NBR 5688	1
Luva Simples, DN50mm, de PVC Rígido Branco Série Normal, conforme NBR 5688	1
Luva Simples, DN100mm, de PVC Rígido Branco Série Normal, conforme NBR 5688	4
Ralo Seco Montado com Grelha e Porta Grelha Quadrados 100x100x40mm, Esgoto	1
Terminal de Ventilação, DN50mm, de PVC Rígido Branco Série Normal, conforme NBR 5688	1
Tê 90°, DN50x50mm, de PVC Rígido Branco Série Normal, conforme NBR 5688	1

Lista de Materiais - Tubos		
Descrição do Material	Diâmetro Nominal (mm)	Comprimento (m)
Tubo de PVC Rígido Branco, conforme NBR5688, Linha Série Normal	Ø100	14,65
Tubo de PVC Rígido Branco, conforme NBR5688, Linha Série Normal	Ø50	5,17
Tubo de PVC Rígido Branco, conforme NBR5688, Linha Série Normal	Ø40	3,41



PENN & WIZE
INSTALAÇÕES PREDIAIS
<https://pennwize.github.io/>



PROJETO: Edifício Derry and Georgie

LOCAL: Rua dos bobos, nº 0. Natal/RN - Brasil

ASSUNTO: Guarita

AUTORES DO PROJETO:
Amanda João Pedro Melo e Letícia Tórres

FOLHA:


E08

REV.:

ESCALA:
Como indicada


DATA:

12/02/2026

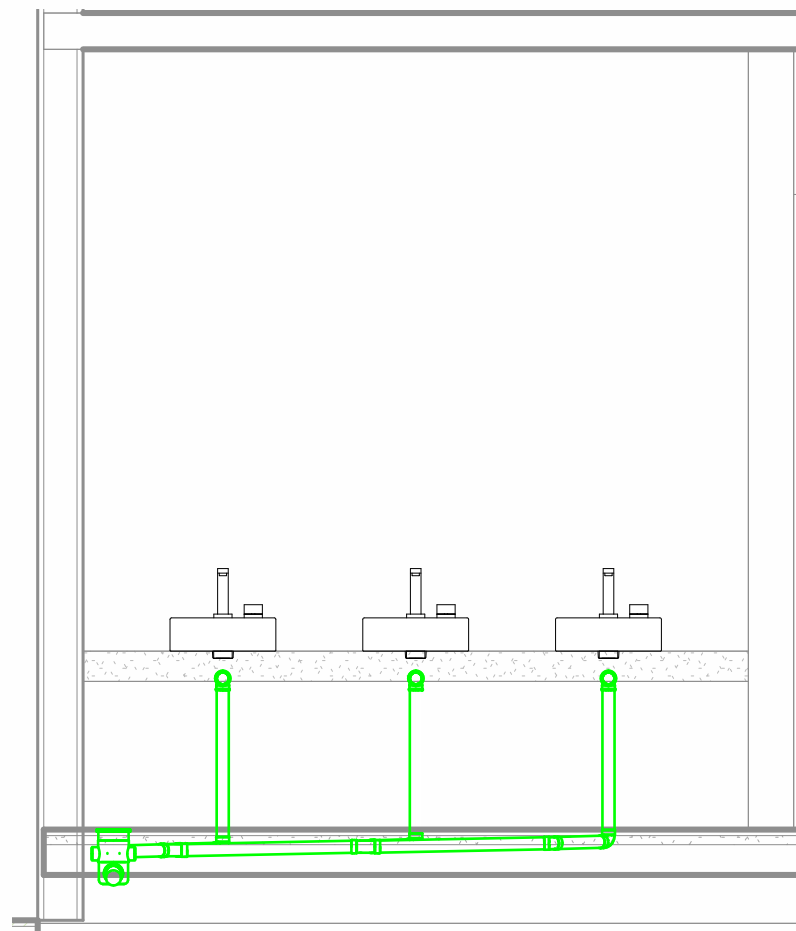

Pias

1 : 25

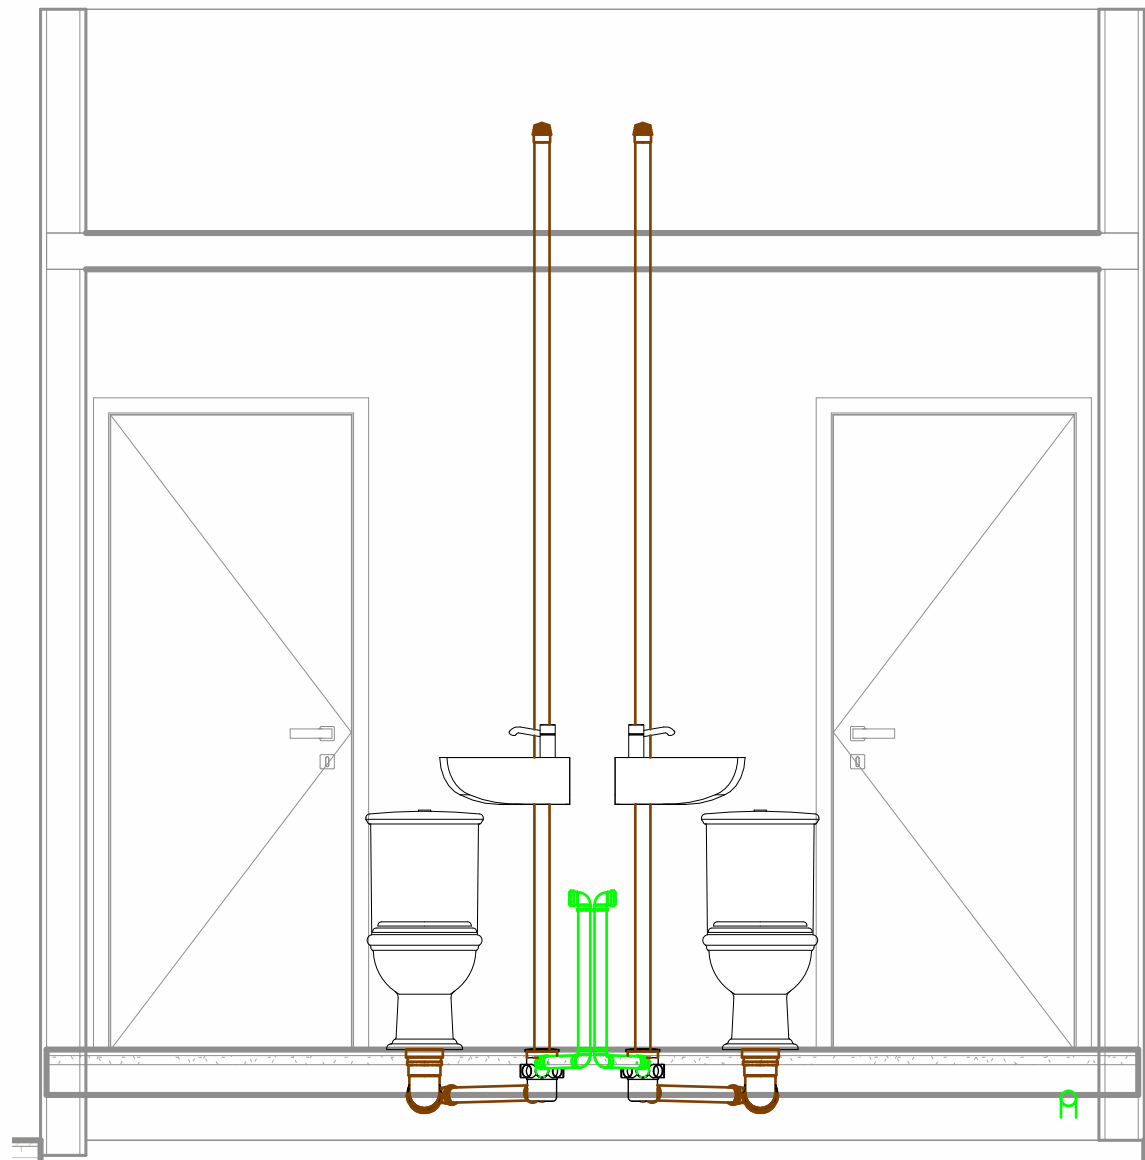


Banheiros

1 : 25




ISO - Salão de Festas

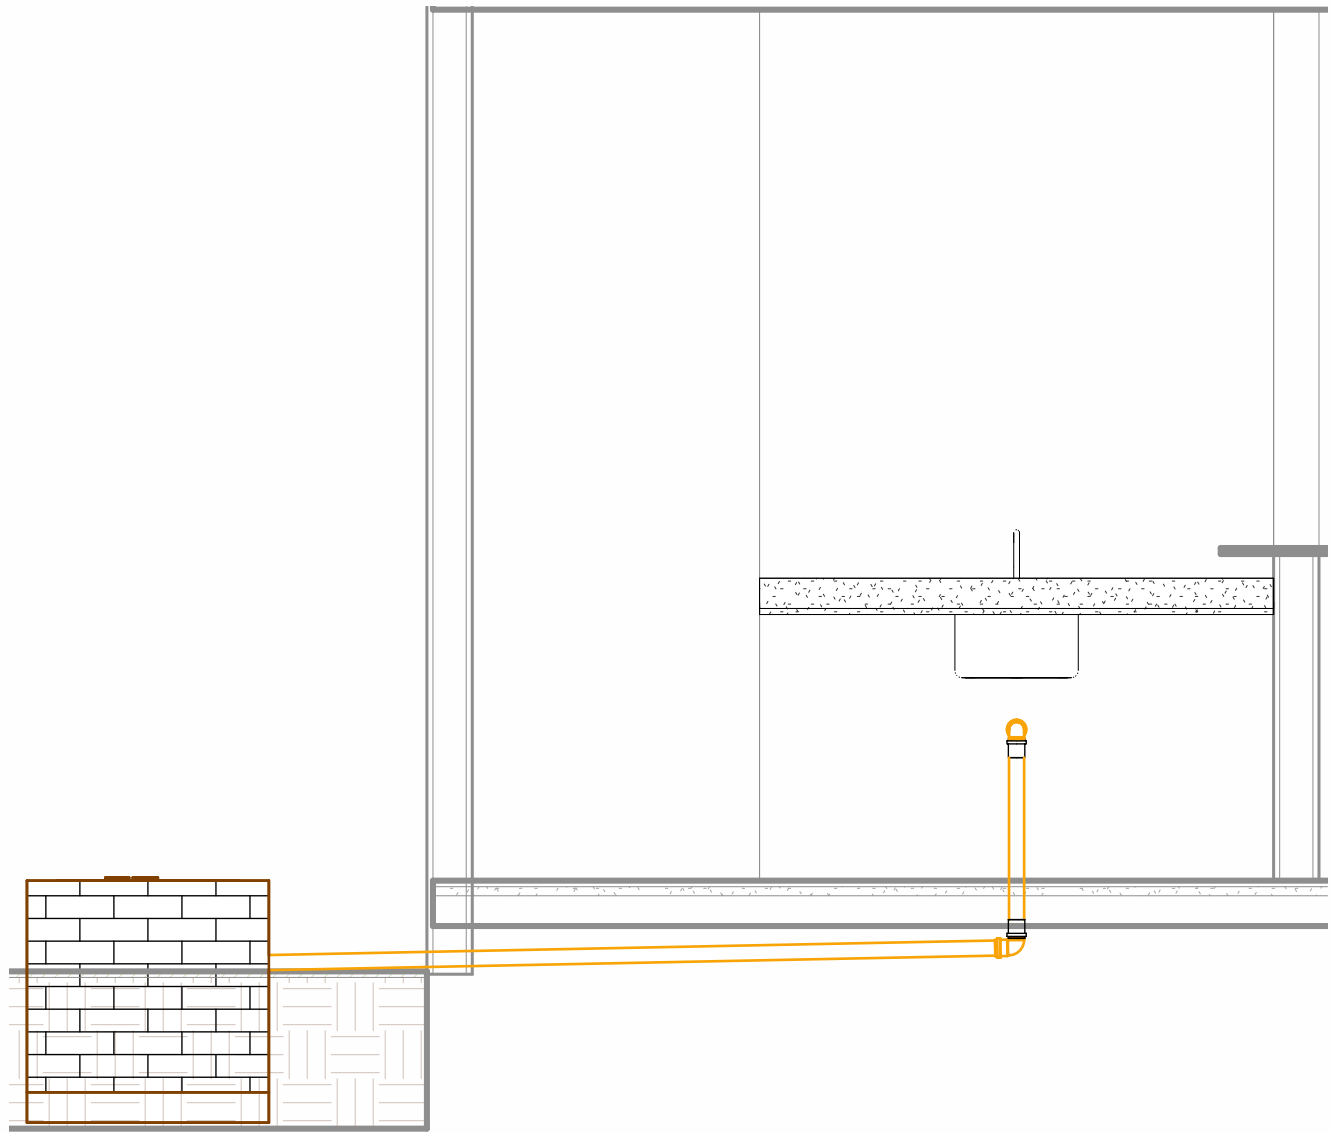

Cozinha

1 : 25

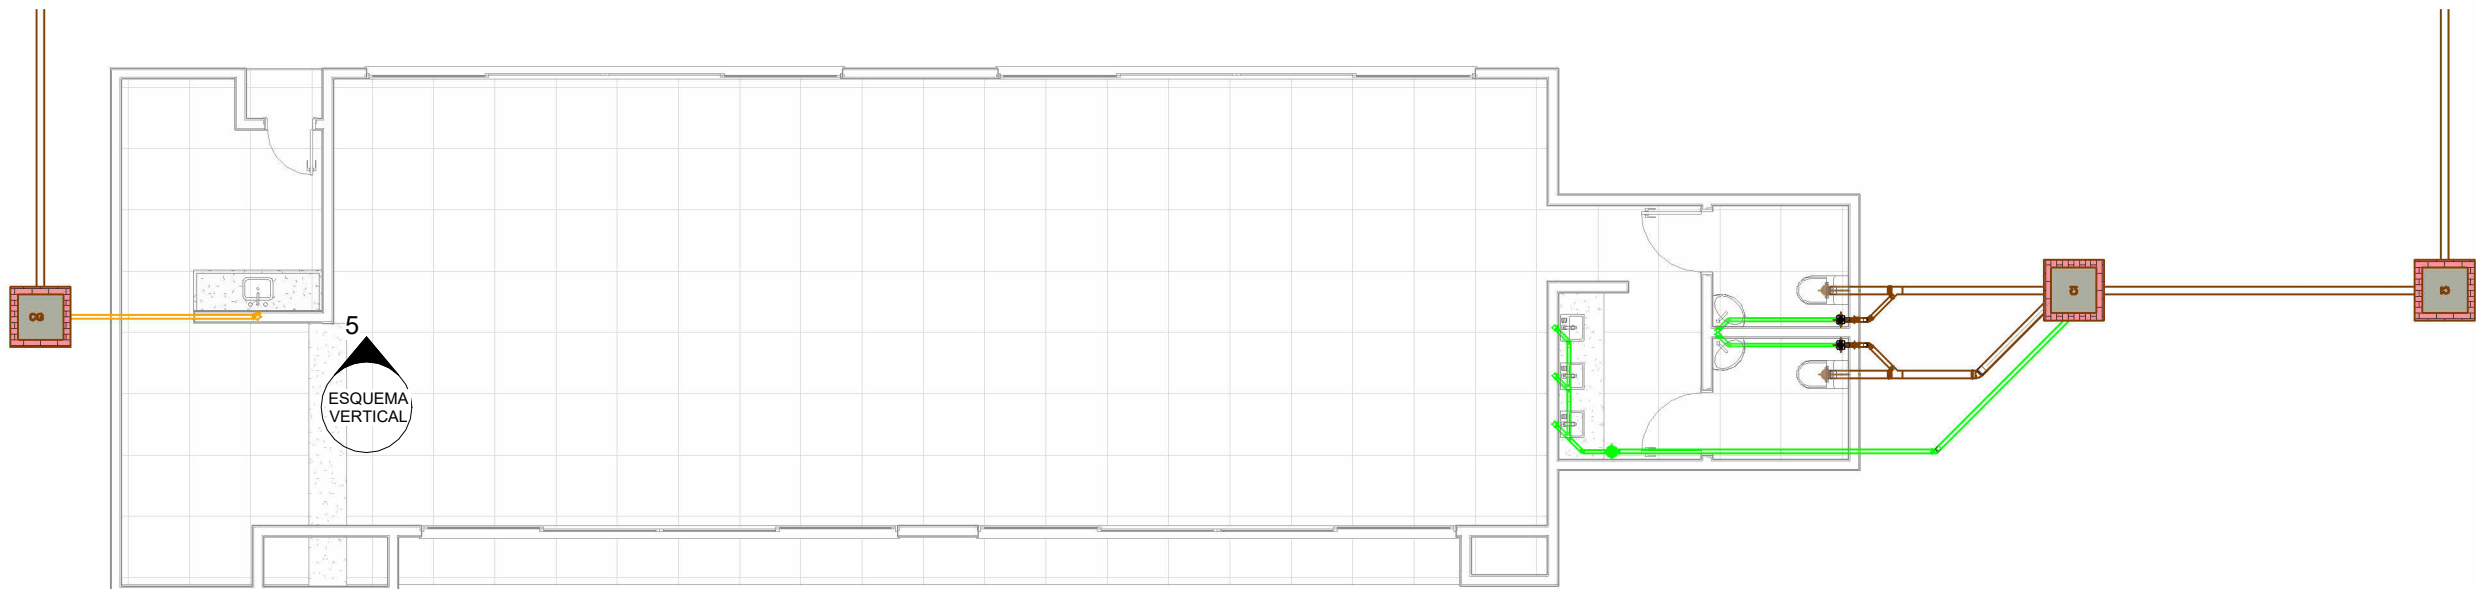

Salão de Festas

1 : 100

LEGENDA:

- TUBULAÇÃO PVC BRANCO SN - ESGOTO PRIMÁRIO
- TUBULAÇÃO PVC BRANCO SN - ESGOTO SECUNDÁRIO
- TUBULAÇÃO PVC BRANCO SN - VENTILAÇÃO ESGOTO
- TUBULAÇÃO PVC BRANCO SN - ESGOTO COM GORDURA

TG-nh
Øxx

-TUBO DE QUEDA DE ESGOTO PRIMÁRIO
nh: número da coluna
xx: diâmetro nominal da coluna

CV-nh
Øxx

-COLUNA DE VENTILAÇÃO
nh: número da coluna
xx: diâmetro nominal da coluna

TG-nh
Øxx

-TUBO DE QUEDA DE GORDURA
nh: número da coluna
xx: diâmetro nominal da coluna

XX

-POSIÇÃO DO ITEM NA LISTA DE MATERIAIS

ABREVIações:

- BS - BACIA SANITÁRIA
- LV - LAVATÓRIO
- CH - CHUVEIRO
- TN - TANQUE
- MLR - MÁQUINA DE LAVAR ROUPAS
- MLL - MÁQUINA DE LAVAR LOUÇAS
- DU - DUCHA HIGIÊNICA
- CS - CAIXA SIFONADA
- RS - RALO SECO
- GSP - CAIXA DE GORDURA PEQUENA
- CI - CAIXA DE INSPEÇÃO

NOTAS:


- DIMENSÕES E DIÂMETROS EM MILÍMETROS, EXCETO ONDE INDICADO CONTRÁRIO.
- NOS TRECHOS HORIZONTAIS DAS TUBULAÇÕES DE ESGOTO SANITÁRIO RECOMENDAM-SE AS SEGUINTE DECLIVIDADES MÍNIMAS:
 - 2% PARA TUBULAÇÕES COM DIÂMETRO NOMINAL IGUAL OU INFERIOR A 75mm;
 - 1% PARA TUBULAÇÕES COM DIÂMETRO NOMINAL IGUAL OU SUPERIOR A 100mm.
- UTILIZAR ANÉIS DE BORRACHA NAS CONEXÕES DE ESGOTO.
- PROIBIDO UTILIZAR FOGO NAS TUBULAÇÕES.
- OS TERMINAIS DE VENTILAÇÃO DOS TUBOS DE VENTILAÇÃO DEVERÃO PASSAR 30CM ACIMA DO TELHADO.
- UTILIZAR DISPOSITIVO ANTI-ESPUMA NA CAIXA SIFONADA DA ÁREA DE SERVIÇO.
- TODAS AS TUBULAÇÕES EXPOSTAS DEVERÃO SER FIXADAS COM BRAÇADEIRA

Lista de Materiais - Conexões e Acessórios	
Descrição do Material	Quantidade
	de
	16
Adaptador para Saída de Vaso Sanitário, DN100mm, de PVC Rígido Branco Série Normal, conforme NBR 5688	2
Anel de Borracha, DN50mm, para linha de PVC Rígido Branco Série Normal, conforme NBR 5688	21
Anel de Borracha, DN100mm, para linha de PVC Rígido Branco Série Normal, conforme NBR 5688	10
Caixa de inspeção em alvenaria com tampa de concreto, 60x60cm	3
Caixa Sifonada Girafácil Montada com Grelha e Porta Grelha Quadrados Brancos 100x140x50mm, 5 Entradas, Esgoto	3
Joelho 45°, DN40mm, de PVC Rígido Branco Série Normal, conforme NBR 5688	4
Joelho 45°, DN50mm, de PVC Rígido Branco Série Normal, conforme NBR 5688	3
Joelho 45°, DN100mm, de PVC Rígido Branco Série Normal, conforme NBR 5688	2
Joelho 90° com anel, DN40mm, de PVC Rígido Branco Série Normal, conforme NBR 5688	5
Joelho 90°, DN40mm, de PVC Rígido Branco Série Normal, conforme NBR 5688	5
Joelho 90°, DN50mm, de PVC Rígido Branco Série Normal, conforme NBR 5688	2
Joelho 90°, DN100mm, de PVC Rígido Branco Série Normal, conforme NBR 5688	2
Junção 45° de Redução, DN100x50mm, de PVC Rígido Branco Série Normal, conforme NBR 5688	2
Junção 45°, DN40x40mm, de PVC Rígido Branco Série Normal, conforme NBR 5688	2
Luva Simples, DN50mm, de PVC Rígido Branco Série Normal, conforme NBR 5688	7
Luva Simples, DN100mm, de PVC Rígido Branco Série Normal, conforme NBR 5688	4
Terminal de Ventilação, DN50mm, de PVC Rígido Branco Série Normal, conforme NBR 5688	2
Tê 90°, DN50x50mm, de PVC Rígido Branco Série Normal, conforme NBR 5688	2
Esgoto Sanitário	
Anel de Borracha, DN100mm, para linha de PVC Rígido Branco Série Normal, conforme NBR 5688	3
Luva Simples, DN100mm, de PVC Rígido Branco Série Normal, conforme NBR 5688	1
Tê 90°, DN100x100mm, de PVC Rígido Branco Série Normal, conforme NBR 5688	1

Lista de Materiais - Tubos		
Descrição do Material	Diâmetro Nominal (mm)	Comprimento (m)
Tubo de PVC Rígido Branco, conforme NBR5688, Linha Série Normal	Ø100	28,68
Tubo de PVC Rígido Branco, conforme NBR5688, Linha Série Normal	Ø50	19,33
Tubo de PVC Rígido Branco, conforme NBR5688, Linha Série Normal	Ø40	8,78



PENN & WIZE
INSTALAÇÕES PREDIAIS
<https://pennwize.github.io/>

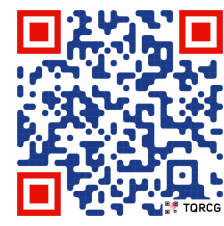

PROJETO: Edifício Derry and George

FOLHA:

LOCAL: Rua dos bobos, nº 0. Natal/RN - Brasil

E09


ASSUNTO: Salão de Festas

REV.:

AUTORES DO PROJETO:
Amanda João Pedro Melo e Letícia Tórres

ESCALA:
Como indicada

DATA:
12/02/2026

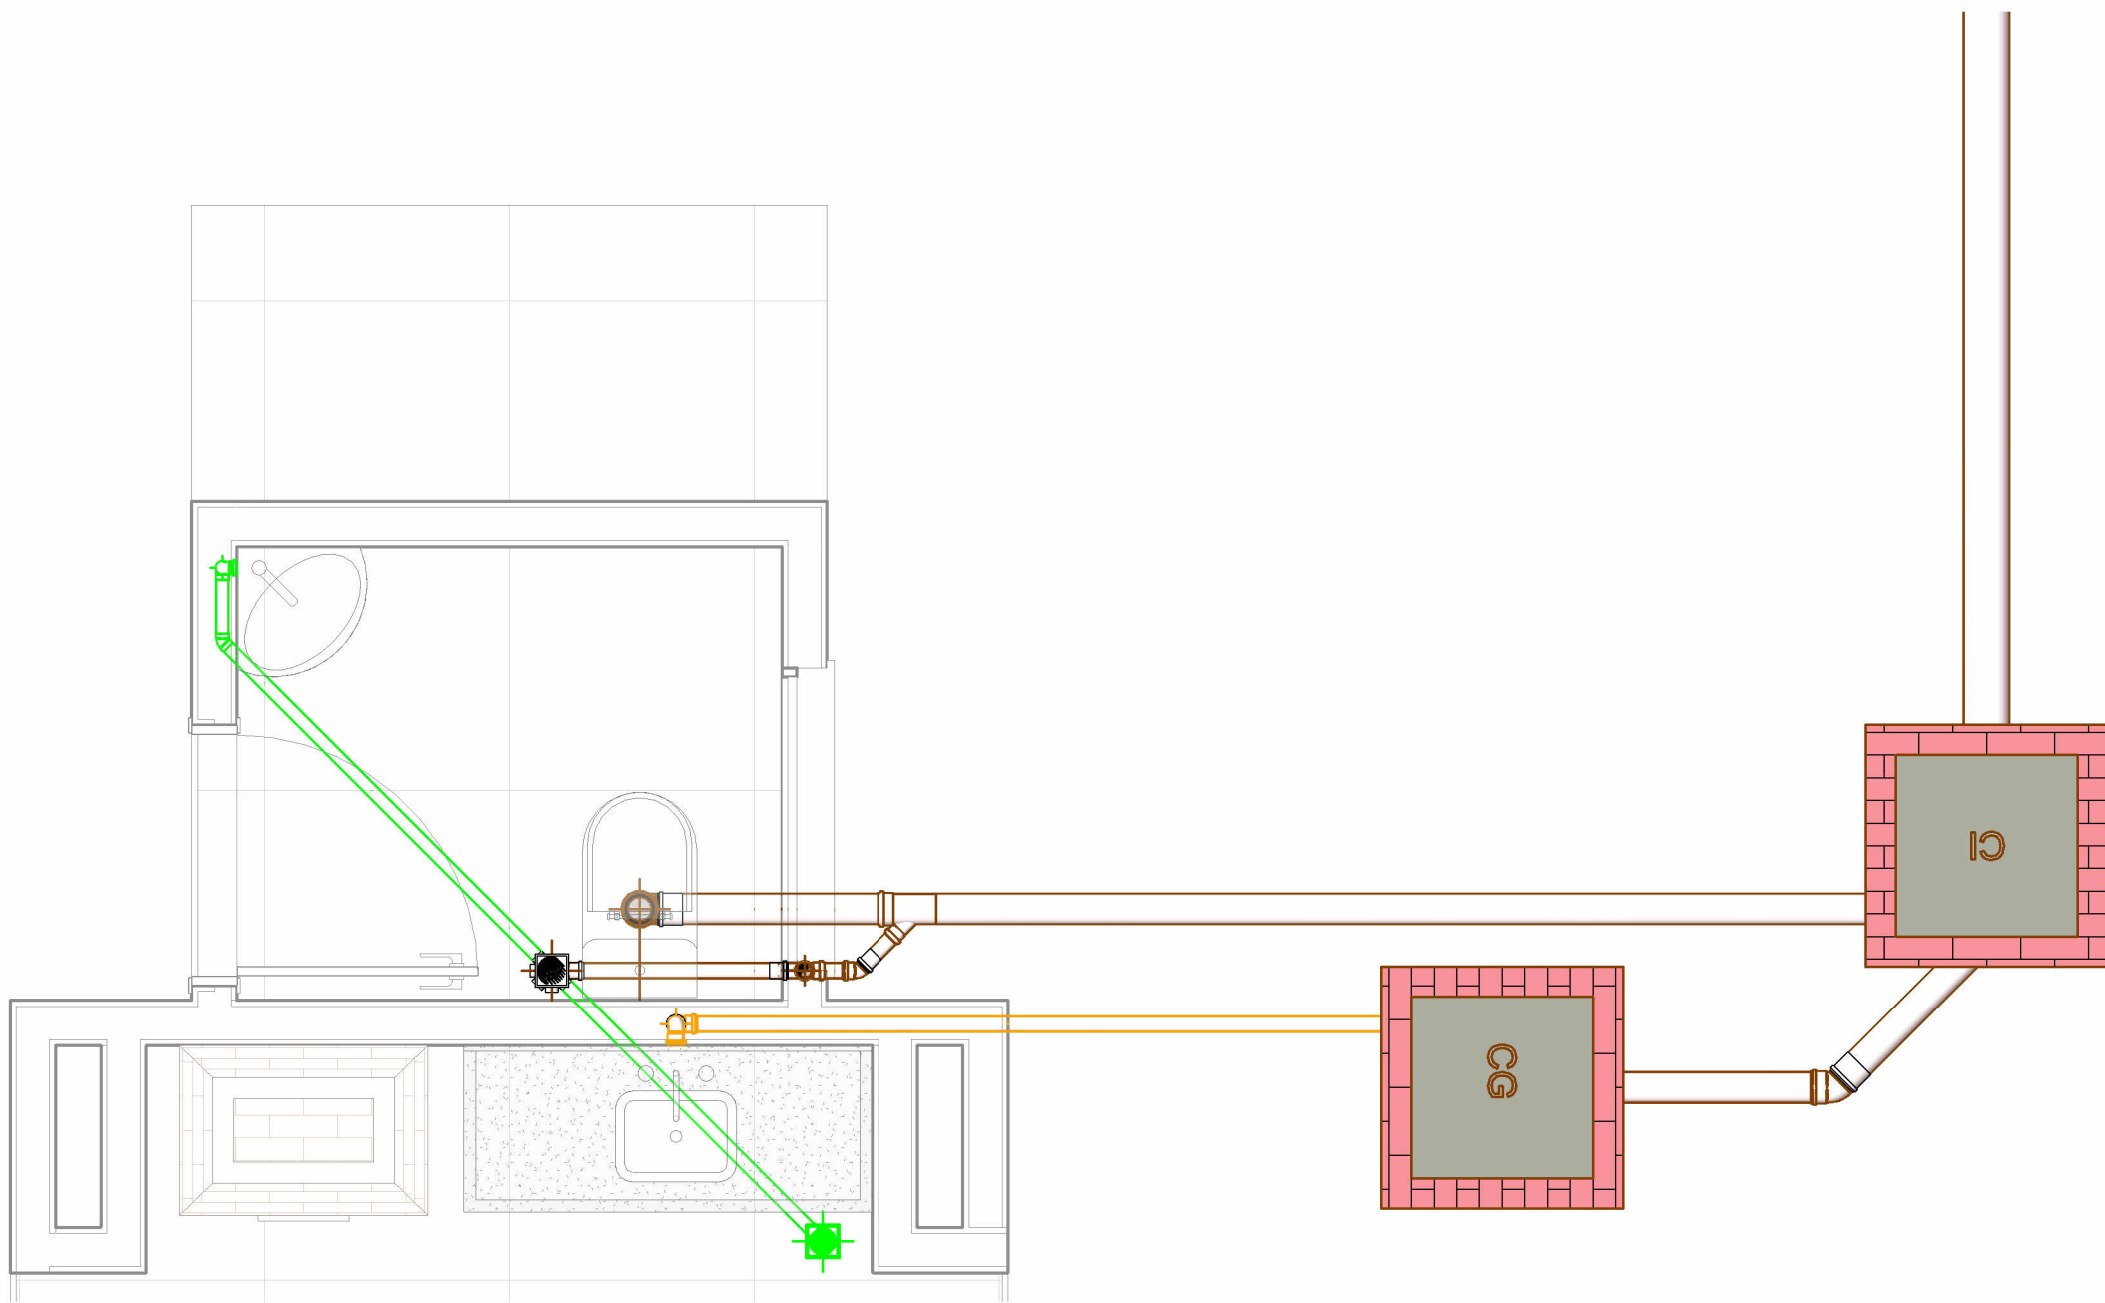

LEGENDA:

- TUBULAÇÃO PVC BRANCO SN - ESGOTO PRIMÁRIO
- TUBULAÇÃO PVC BRANCO SN - ESGOTO SECUNDÁRIO
- TUBULAÇÃO PVC BRANCO SN - VENTILAÇÃO ESGOTO
- TUBULAÇÃO PVC BRANCO SN - ESGOTO COM GORDURA

- TUBO DE QUEDA DE ESGOTO PRIMÁRIO
- COLUNA DE VENTILAÇÃO
- TUBO DE QUEDA DE GORDURA
- POSIÇÃO DO ITEM NA LISTA DE MATERIAIS

ABREVIações:


- BS - BACIA SANITÁRIA
- LV - LAVATÓRIO
- CH - CHUVEIRO
- TN - TANQUE
- MLR - MÁQUINA DE LAVAR ROUPAS
- MLL - MÁQUINA DE LAVAR LOUÇAS
- DU - DUCHA HIGIÊNICA
- CS - CAIXA SIFONADA
- RS - RALO SECO
- CGP - CAIXA DE GORDURA PEQUENA
- CI - CAIXA DE INSPEÇÃO

NOTAS:

- 1 - DIMENSÕES E DIÂMETROS EM MILÍMETROS, EXCETO ONDE INDICADO CONTRÁRIO.
- 2 - NOS TRECHOS HORIZONTAIS DAS TUBULAÇÕES DE ESGOTO SANITÁRIO RECOMENDAM-SE AS SEGUINTEs DECLIVIDADES MÍNIMAS:
 - 2% PARA TUBULAÇÕES COM DIÂMETRO NOMINAL IGUAL OU INFERIOR A 75mm;
 - 1% PARA TUBULAÇÕES COM DIÂMETRO NOMINAL IGUAL OU SUPERIOR A 100mm.
- 3 - UTILIZAR ANÉIS DE BORRACHA NAS CONEXÕES DE ESGOTO.
- 4 - PROIBIDO UTILIZAR FOGO NAS TUBULAÇÕES.
- 5 - OS TERMINAIS DE VENTILAÇÃO DOS TUBOS DE VENTILAÇÃO DEVERÃO PASSAR 30CM ACIMA DO TELHADO.
- 6 - UTILIZAR DISPOSITIVO ANTI-ESPUMA NA CAIXA SIFONADA DA ÁREA DE SERVIÇO.
- 7 - TODAS AS TUBULAÇÕES EXPOSTAS DEVERÃO SER FIXADAS COM BRAÇADEIRA

Churrasqueira

1 : 25

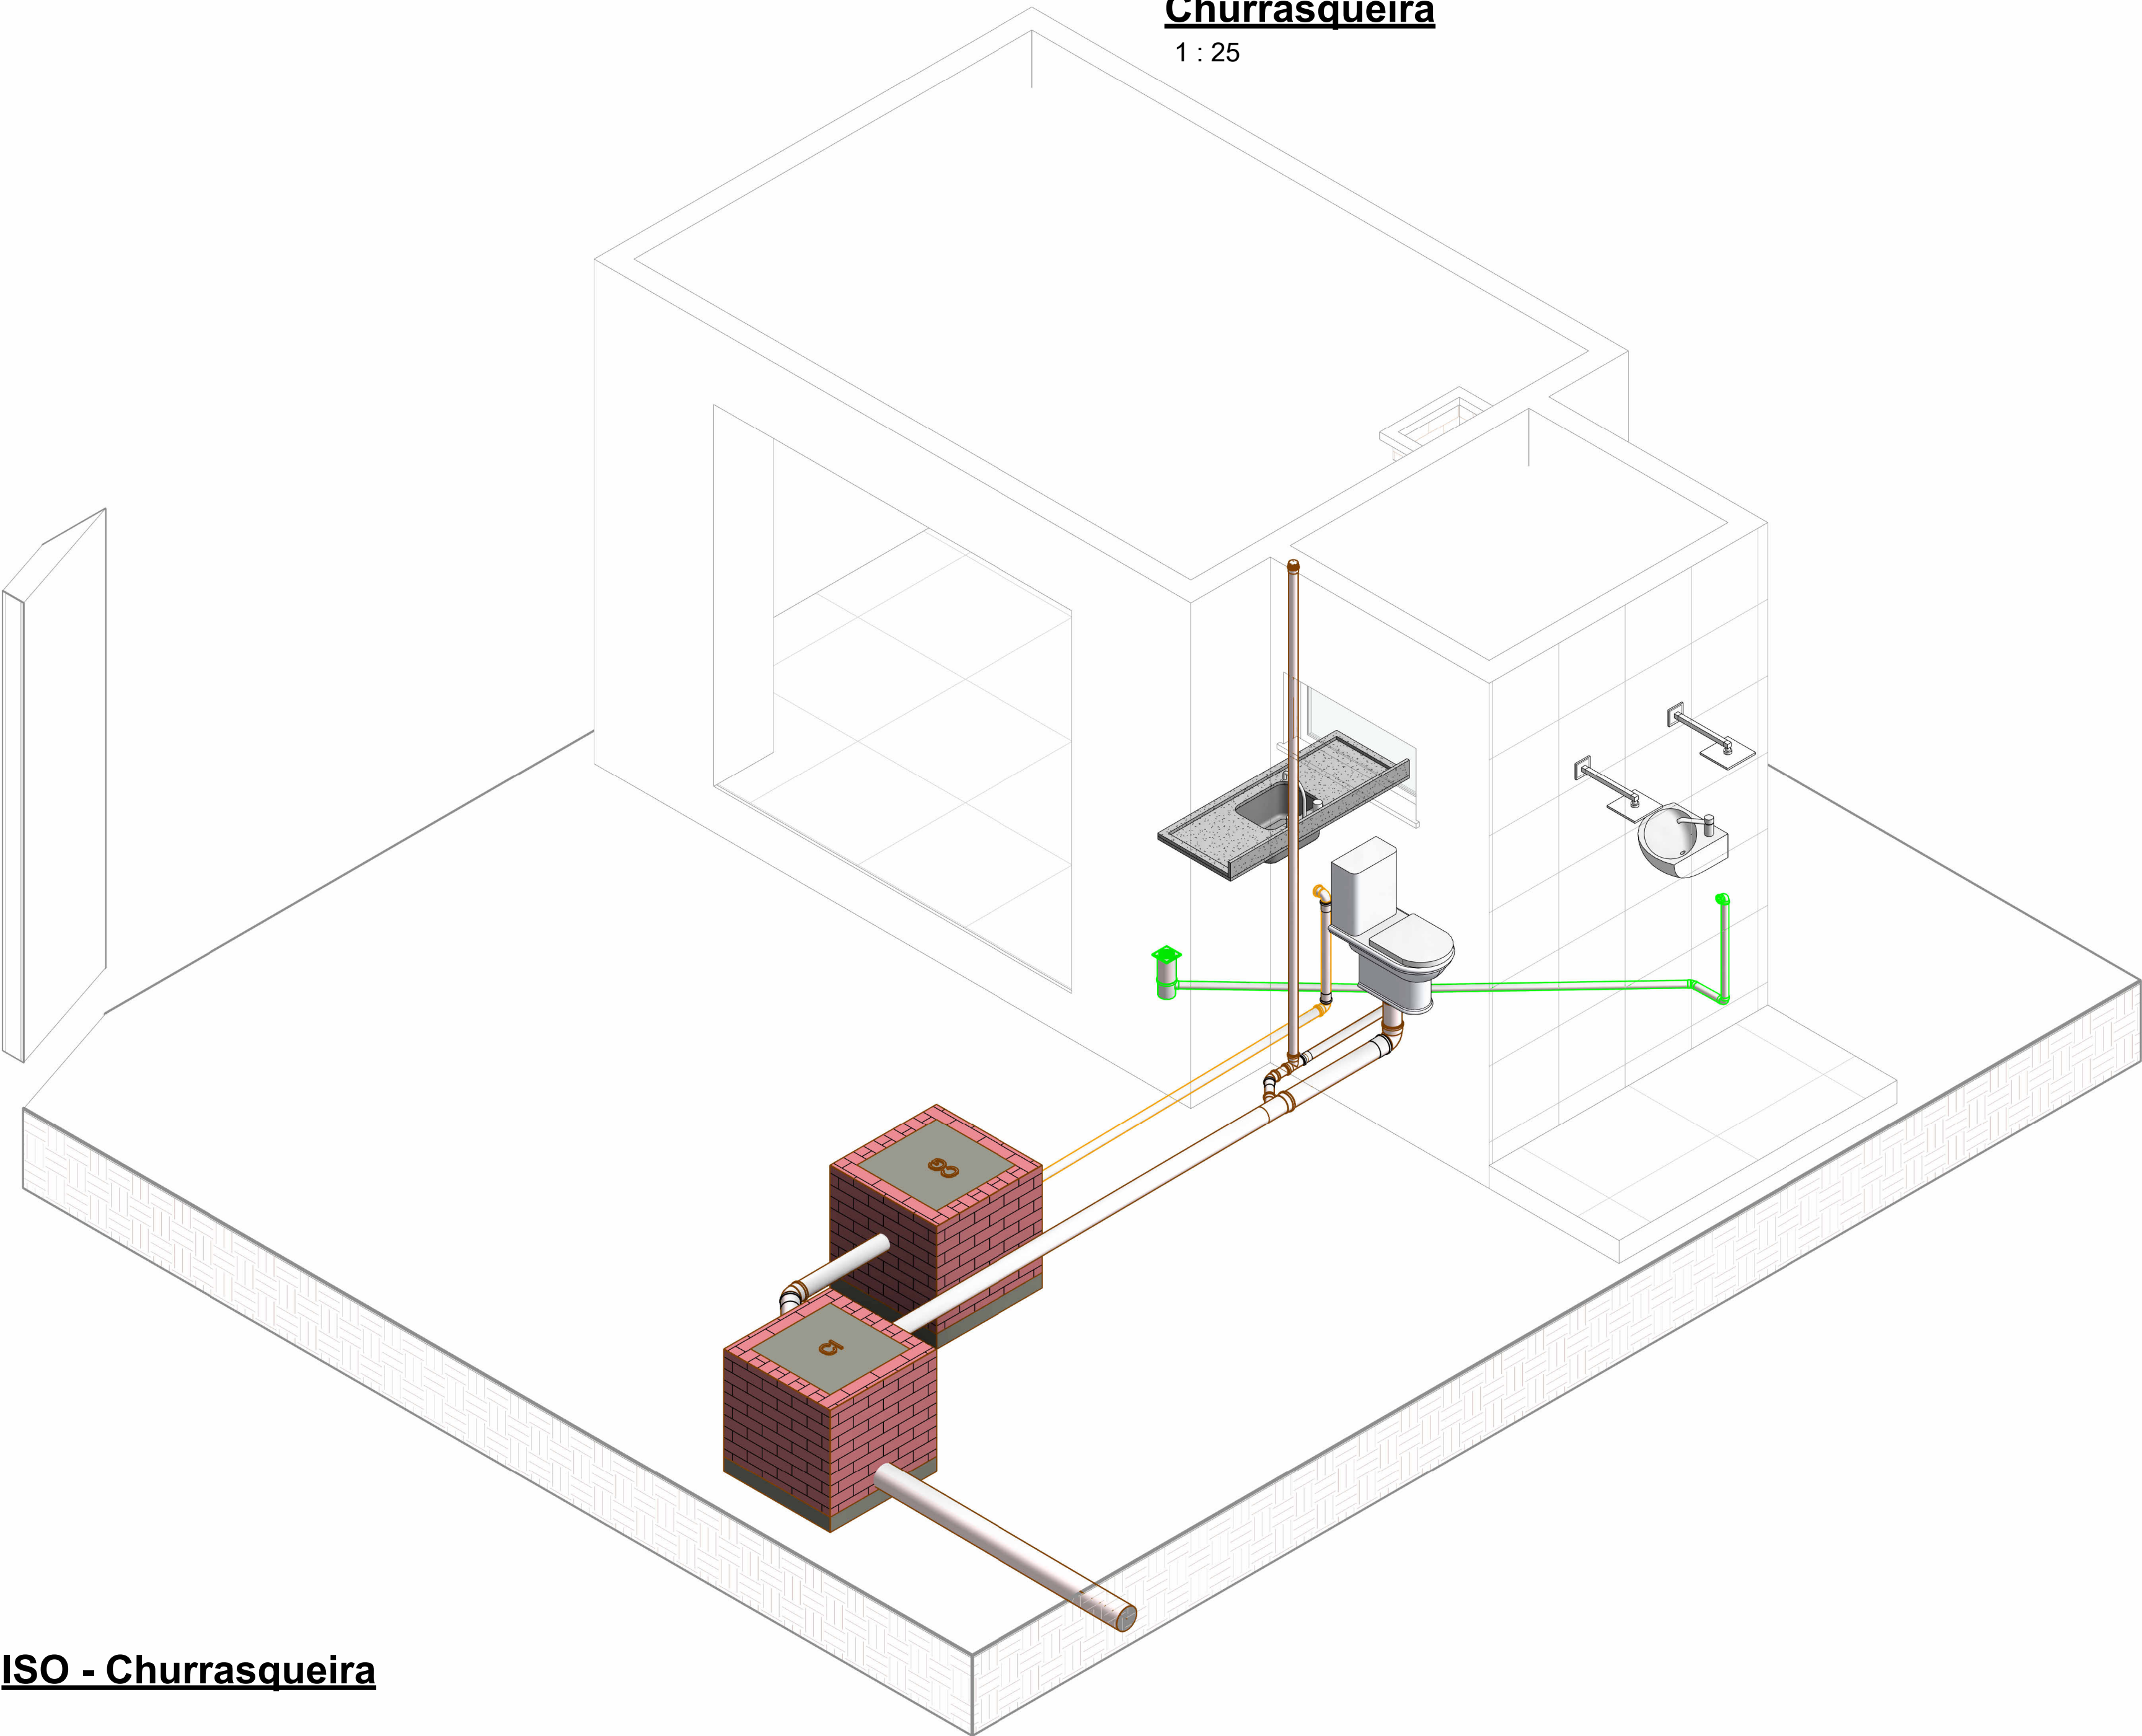


ISO - Churrasqueira

Lista de Materiais - Conexões e Acessórios	
Descrição do Material	Quantidade
	9
Adaptador para Saída de Vaso Sanitário, DN100mm, de PVC Rígido Branco Série Normal, conforme NBR 5688	1
Anel de Borracha, DN50mm, para linha de PVC Rígido Branco Série Normal, conforme NBR 5688	11
Anel de Borracha, DN100mm, para linha de PVC Rígido Branco Série Normal, conforme NBR 5688	5
Caixa de inspeção em alvenaria com tampa de concreto, 60x60cm	2
Caixa Sifonada Girafácil Montada com Grelha e Porta Grelha Quadrados Brancos 100x140x50mm, 5 Entradas, Esgoto	1
Joelho 45°, DN40mm, de PVC Rígido Branco Série Normal, conforme NBR 5688	1
Joelho 45°, DN50mm, de PVC Rígido Branco Série Normal, conforme NBR 5688	1
Joelho 45°, DN100mm, de PVC Rígido Branco Série Normal, conforme NBR 5688	1
Joelho 90° com anel, DN40mm, de PVC Rígido Branco Série Normal, conforme NBR 5688	1
Joelho 90°, DN40mm, de PVC Rígido Branco Série Normal, conforme NBR 5688	1
Joelho 90°, DN50mm, de PVC Rígido Branco Série Normal, conforme NBR 5688	2
Joelho 90°, DN100mm, de PVC Rígido Branco Série Normal, conforme NBR 5688	1
Junção 45° de Redução, DN100x50mm, de PVC Rígido Branco Série Normal, conforme NBR 5688	1
Luva Simples, DN50mm, de PVC Rígido Branco Série Normal, conforme NBR 5688	4
Luva Simples, DN100mm, de PVC Rígido Branco Série Normal, conforme NBR 5688	2
Ralo Seco Montado com Grelha e Porta Grelha Quadrados 100x100x40mm, Esgoto	1
Terminal de Ventilação, DN50mm, de PVC Rígido Branco Série Normal, conforme NBR 5688	1
Tê 90°, DN50x50mm, de PVC Rígido Branco Série Normal, conforme NBR 5688	1
Esgoto Sanitário	
Anel de Borracha, DN100mm, para linha de PVC Rígido Branco Série Normal, conforme NBR 5688	3
Luva Simples, DN100mm, de PVC Rígido Branco Série Normal, conforme NBR 5688	1
Tê 90°, DN100x100mm, de PVC Rígido Branco Série Normal, conforme NBR 5688	1

Lista de Materiais - Tubos		
Descrição do Material	Diâmetro Nominal (mm)	Comprimento (m)
Tubo de PVC Rígido Branco, conforme NBR5688, Linha Série Normal	Ø150	18,54
Tubo de PVC Rígido Branco, conforme NBR5688, Linha Série Normal	Ø100	6,61
Tubo de PVC Rígido Branco, conforme NBR5688, Linha Série Normal	Ø50	8,01
Tubo de PVC Rígido Branco, conforme NBR5688, Linha Série Normal	Ø40	3,84



PENN & WIZE
INSTALAÇÕES PREDIAIS
<https://pennwize.github.io/>

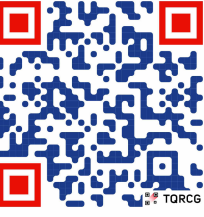

PROJETO:	Edifício Derry and Georgie	FOLHA:	E10
LOCAL:	Rua dos bobos, nº 0. Natal/RN - Brasil	REV.:	ESCALA:
ASSUNTO:	Churrasqueira		Como indicada
AUTORES DO PROJETO:	Amanda João Pedro Melo e Letícia Tórres	DATA:	12/02/2026