



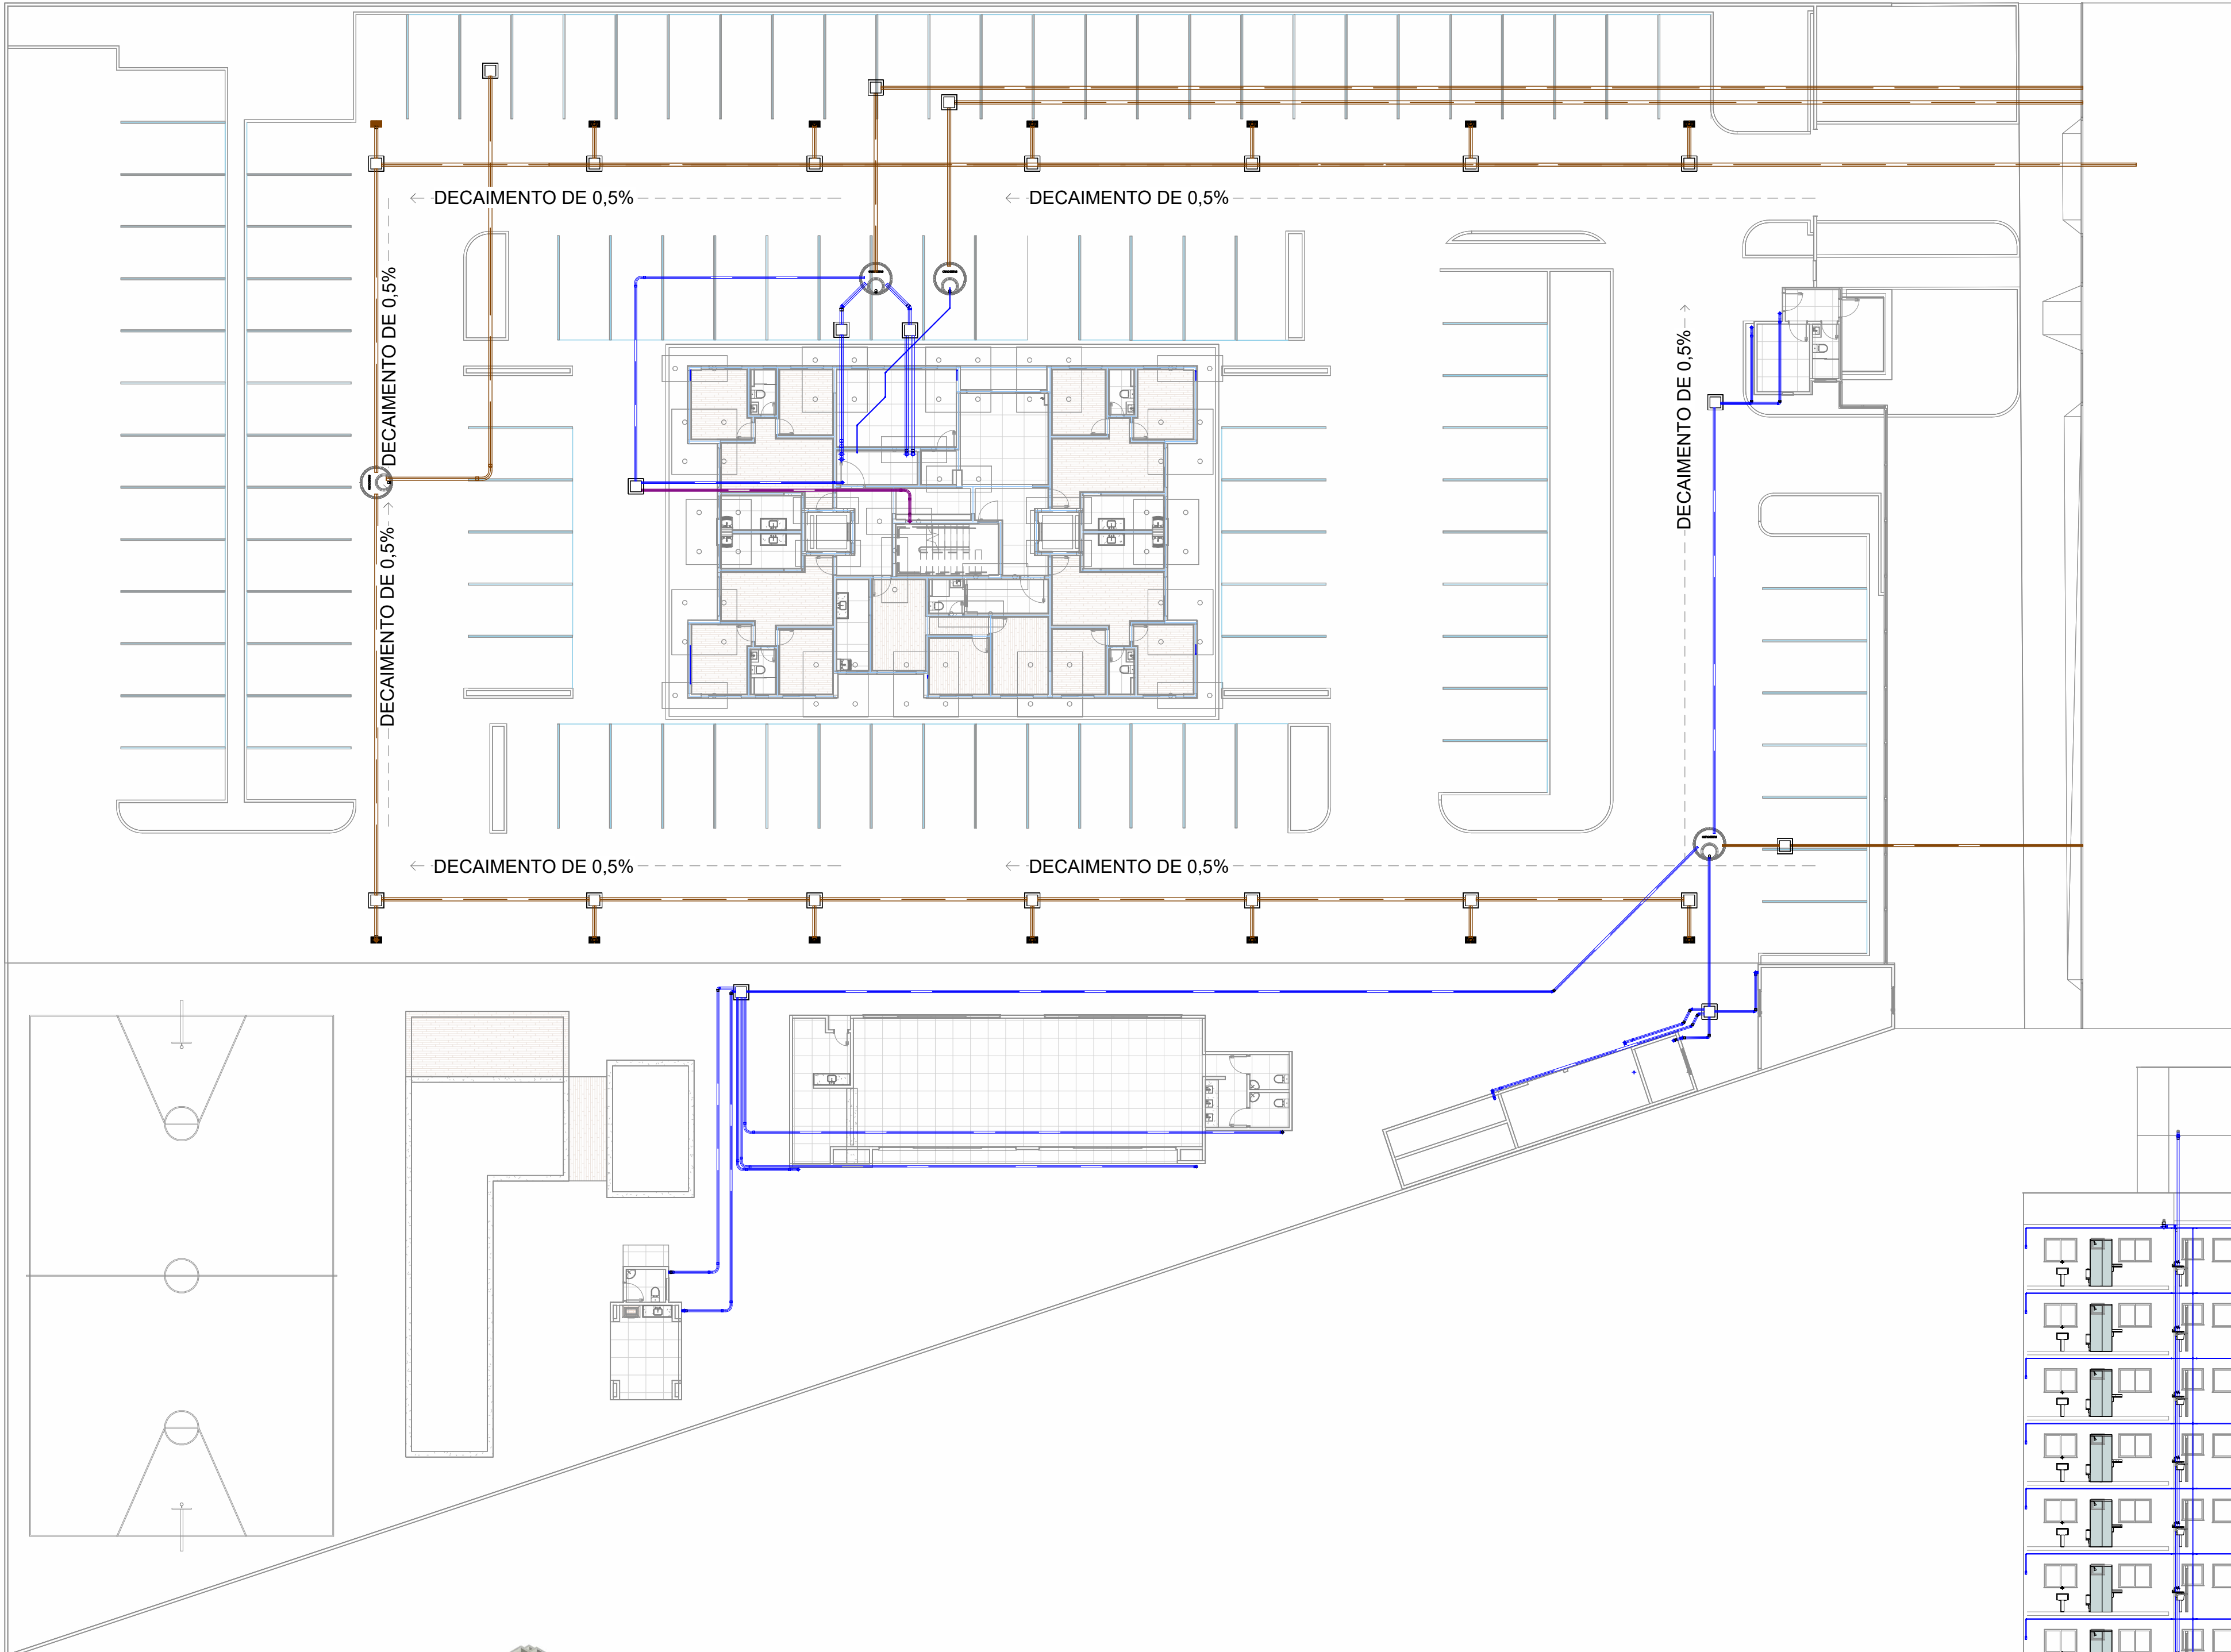


Plano Geral
1 : 200

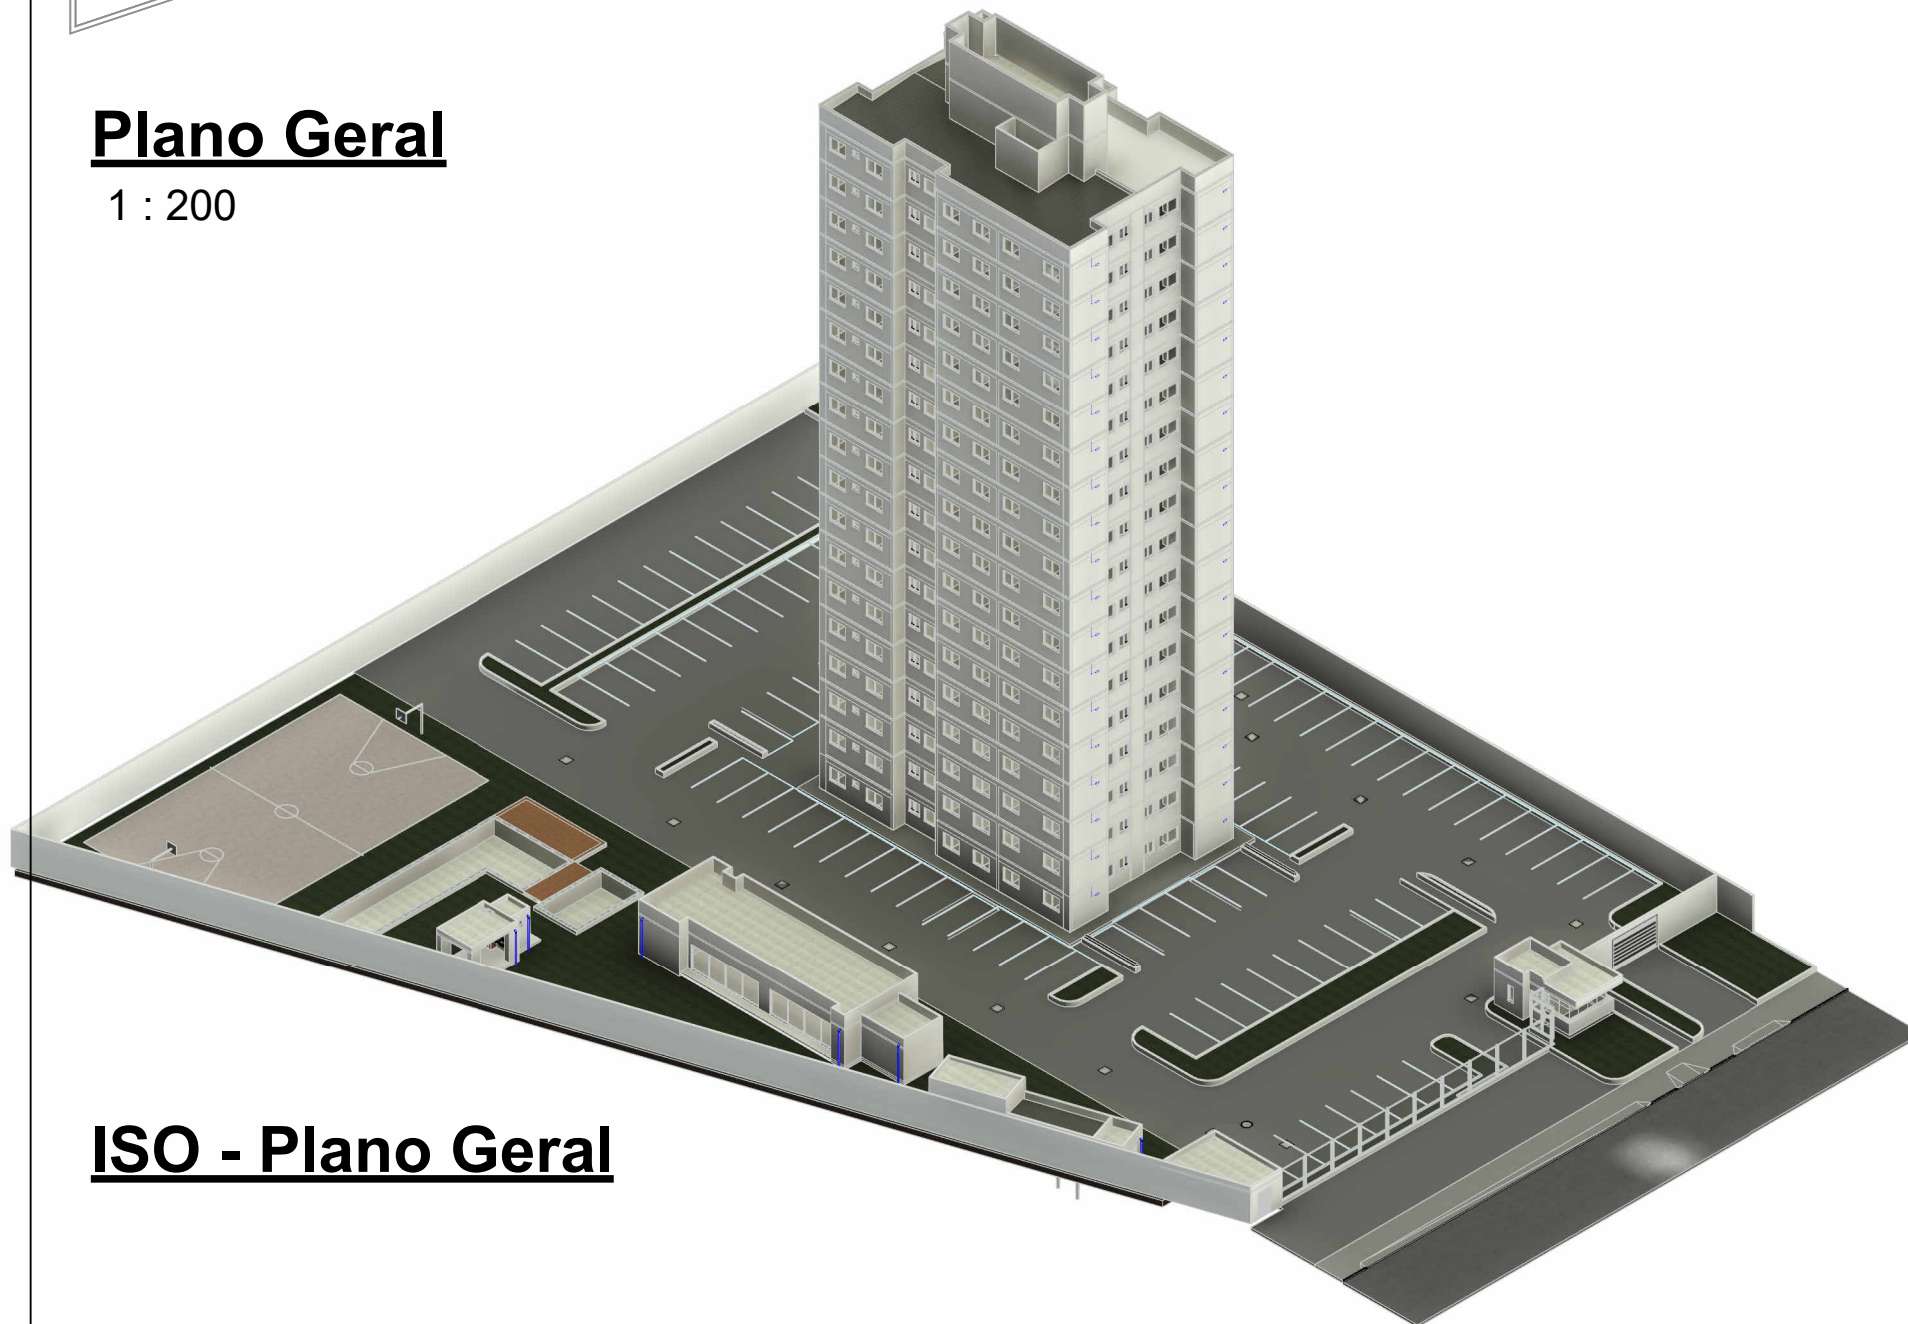

ISO - Plano Geral

Elevação Geral
1 : 200

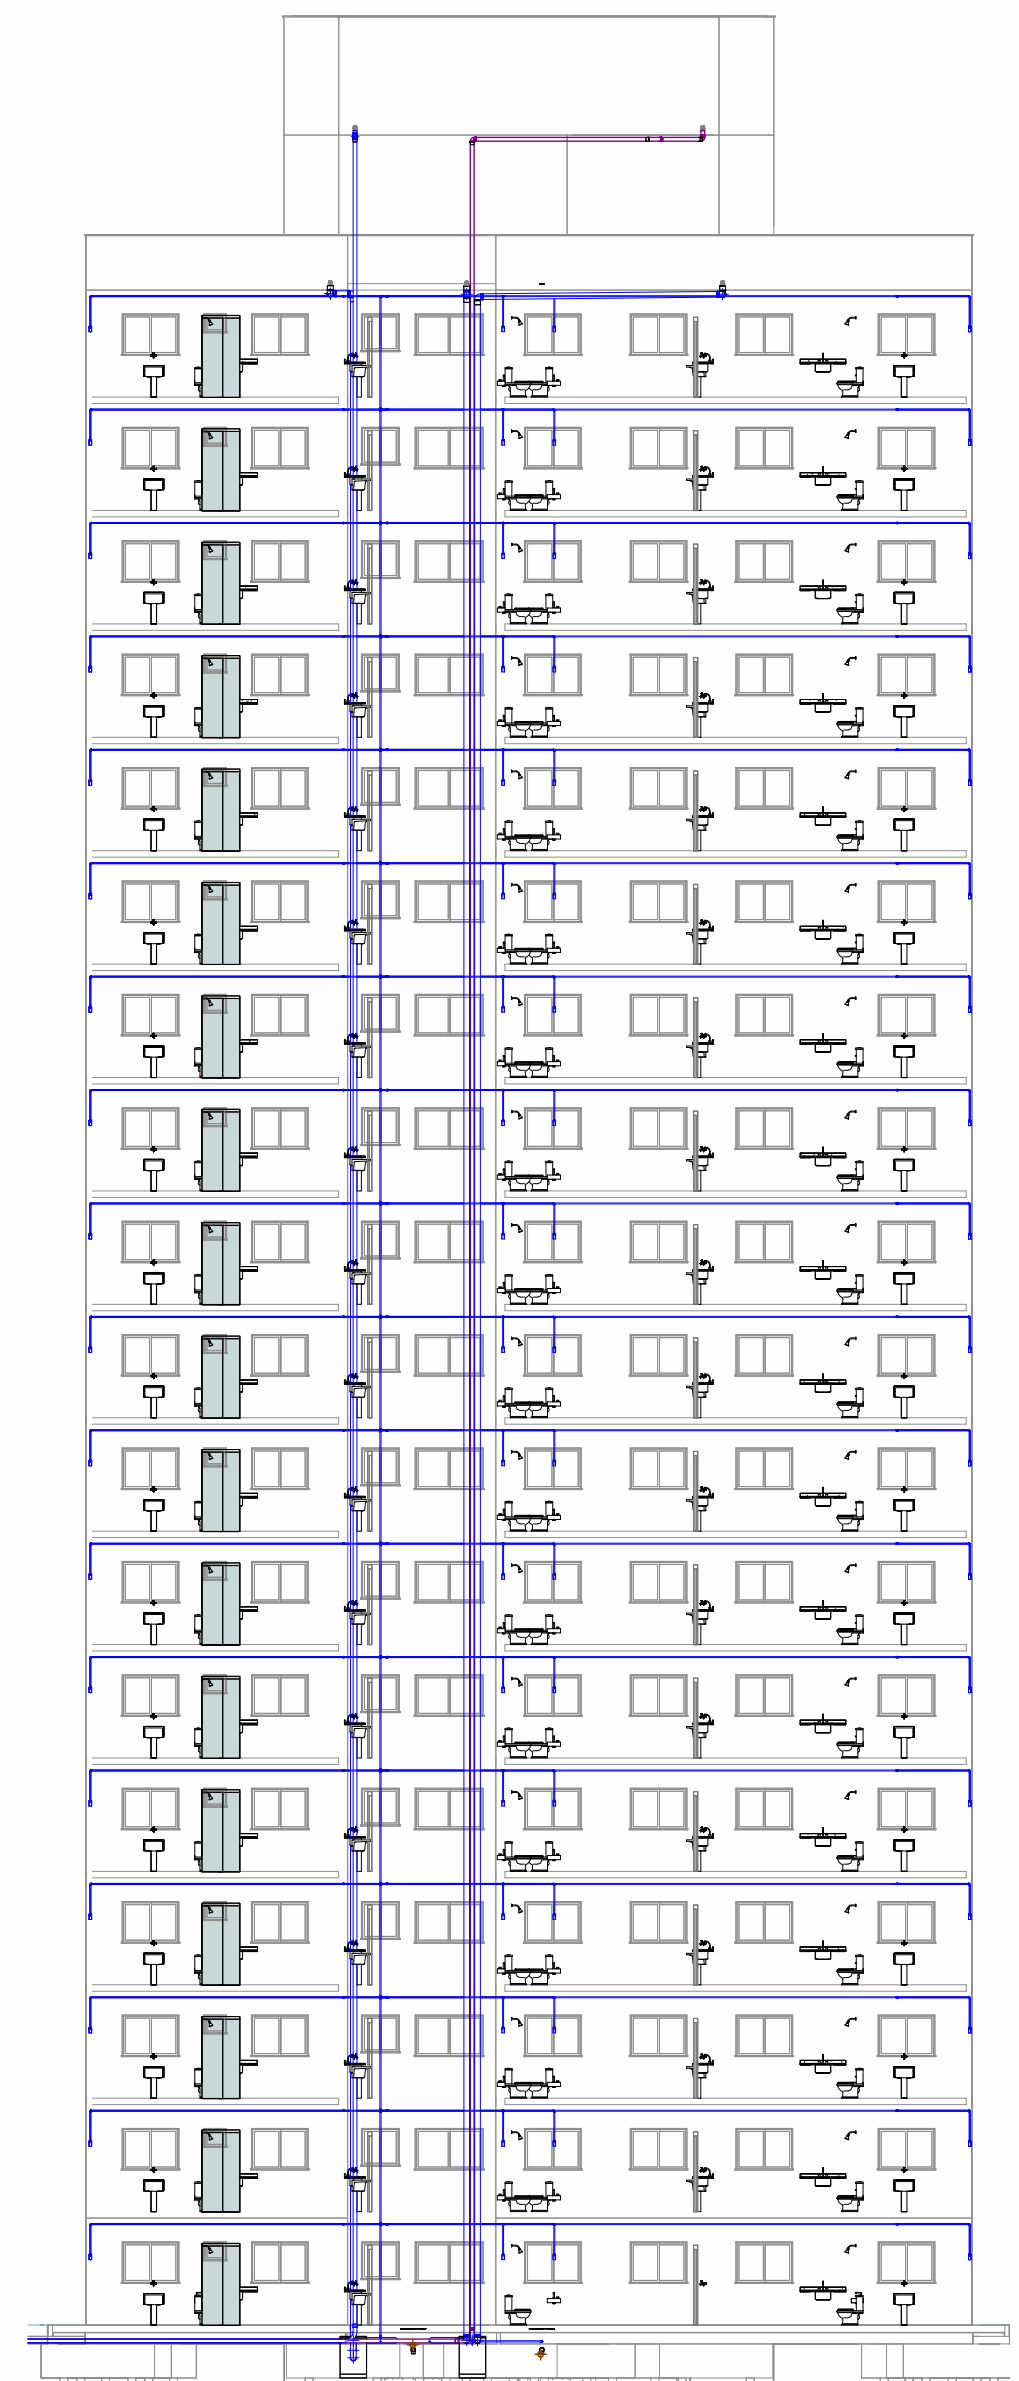

LEGENDA:

- TUBULAÇÃO PVC BRANCO SN - ESGOTO PRIMÁRIO
- TUBULAÇÃO PVC BRANCO SN - ESGOTO SECUNDÁRIO
- TUBO DE QUEDA DE ESGOTO PRIMÁRIO

ABREVIações:

RS - RALO SECO

- NOTAS:**
- DIMENSÕES E DIÂMETROS EM MILÍMETROS, EXCETO ONDE INDICADO CONTRÁRIO.
 - NOS TRECHOS HORIZONTAIS DAS TUBULAÇÕES DE ESGOTO SANITÁRIO RECOMENDAM-SE AS SEGUINTEs DECLIVIDADES MÍNIMAS:
 - 2% PARA TUBULAÇÕES COM DIÂMETRO NOMINAL IGUAL OU INFERIOR A 75mm;
 - 1% PARA TUBULAÇÕES COM DIÂMETRO NOMINAL IGUAL OU SUPERIOR A 100mm;
 - UTILIZAR ANEIS DE BORRACHA NAS CONEXÕES DE ESGOTO.
 - PROIBIDO UTILIZAR FOGO NAS TUBULAÇÕES.
 - OS TERMINAIS DE VENTILAÇÃO DOS TUBOS DE VENTILAÇÃO DEVERÃO PASSAR 30CM ACIMA DO TELHADO.
 - UTILIZAR DISPOSITIVO ANTI-ESPUMA NA CAIXA SIFONADA DA ÁREA DE SERVIÇO.
 - TODAS AS TUBULAÇÕES EXPOSTAS DEVERÃO SER FIXADAS COM BRACADEIRA.
 - A BASE DO RESERVATÓRIO DEVERÁ TER UMA SUPERFÍCIE LISA, NIVELADA E ISENTA DE SUEIRA OU MATERIAIS PONTAGUDOS. A BASE DEVE TER RESISTÊNCIA COMPATIVEL COM O PESO DA CAIXA CHEIA E DEVE SER MAIOR DO QUE A LARGURA DO FUNDO DA CAIXA.

Lista de Materiais - Conexões e Acessórios - Completa	
Descrição do Material	Quantidade (peças)
	246
Anel de Borracha, DN100mm, para linha de PVC Rígido Branco Série Normal, conforme NBR 5688	94
Anel de Borracha, DN150mm, para linha de PVC Rígido Branco Série Normal, conforme NBR 5688	58
Anel de Concreto perfurado, pré moldado, para Sumidouro, Ø Externo 1500mm, Altura 500mm	20
Brita N°4	4
Bucha de Redução Curta, DN32x25mm, PVC Marrom Soldável, conforme NBR 5648	1
Curva Longa 45°, DN100mm, de PVC Rígido Branco Série Normal, conforme NBR 5688	1
Curva Longa 90°, DN100mm, de PVC Rígido Branco Série Normal, conforme NBR 5688	1
inexistente	2
Joelho 45°, DN32mm, PVC Marrom Soldável, conforme NBR 5648	4
Joelho 45°, DN100mm, de PVC Rígido Branco Série Normal, conforme NBR 5688	3
Joelho 45°, DN150mm, de PVC Rígido Branco Série Normal, conforme NBR 5688	2
Joelho 90°, DN25mm, PVC Marrom Soldável, conforme NBR 5648	270
Joelho 90°, DN32mm, PVC Marrom Soldável, conforme NBR 5648	2
Joelho 90°, DN100mm, de PVC Rígido Branco Série Normal, conforme NBR 5688	42
Joelho 90°, DN150mm, de PVC Rígido Branco Série Normal, conforme NBR 5688	27
Laje para fossa, filtro anaeróbico e Sumidouro, Ø Externo 1500mm	4
Luva Simples, DN100mm, de PVC Rígido Branco Série Normal, conforme NBR 5688	45
Luva Simples, DN150mm, de PVC Rígido Branco Série Normal, conforme NBR 5688	29
Luva, DN32mm, PVC Marrom Soldável, conforme NBR 5648	1
Produto inexistente	16
Tampa, para fossa, filtro Anaeróbio e Sumidouro, Ø600mm	4
Tê de Redução, DN32x25mm, PVC Marrom Soldável, conforme NBR 5648	17
Tê, DN25mm, PVC Marrom Soldável, conforme NBR 5648	90


Lista de Materiais - Tubos			
Descrição do Material	Diâmetro Nominal (mm)	Comprimento (m)	Referência de Fabricante
Tubo de PVC Rígido Branco, conforme NBR5688, Linha Série Normal	Ø150	721,35	Tigre
Tubo de PVC Rígido Branco, conforme NBR5688, Linha Série Normal	Ø100	460,91	Tigre
Tubo de PVC Rígido Soldável Marrom, conforme NBR 5648	Ø32	68,70	Tigre
Tubo de PVC Rígido Soldável Marrom, conforme NBR 5648	Ø25	1464,46	Tigre



PENN & WIZE

INSTALAÇÕES PREDIAIS

<https://pennwize.github.io/>

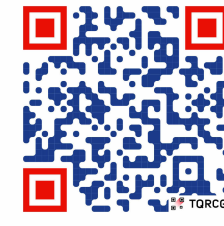

PROJETO: Edifício Derry and George

LOCAL: Rua dos bobos, nº 0. Natal/RN - Brasil


ASSUNTO: Folha - Plano Geral

AUTORES DO PROJETO: Amanda João Pedro Melo e Letícia Tórres

FOLHA: P01

REV.: Como indicada

DATA: 10/02/26

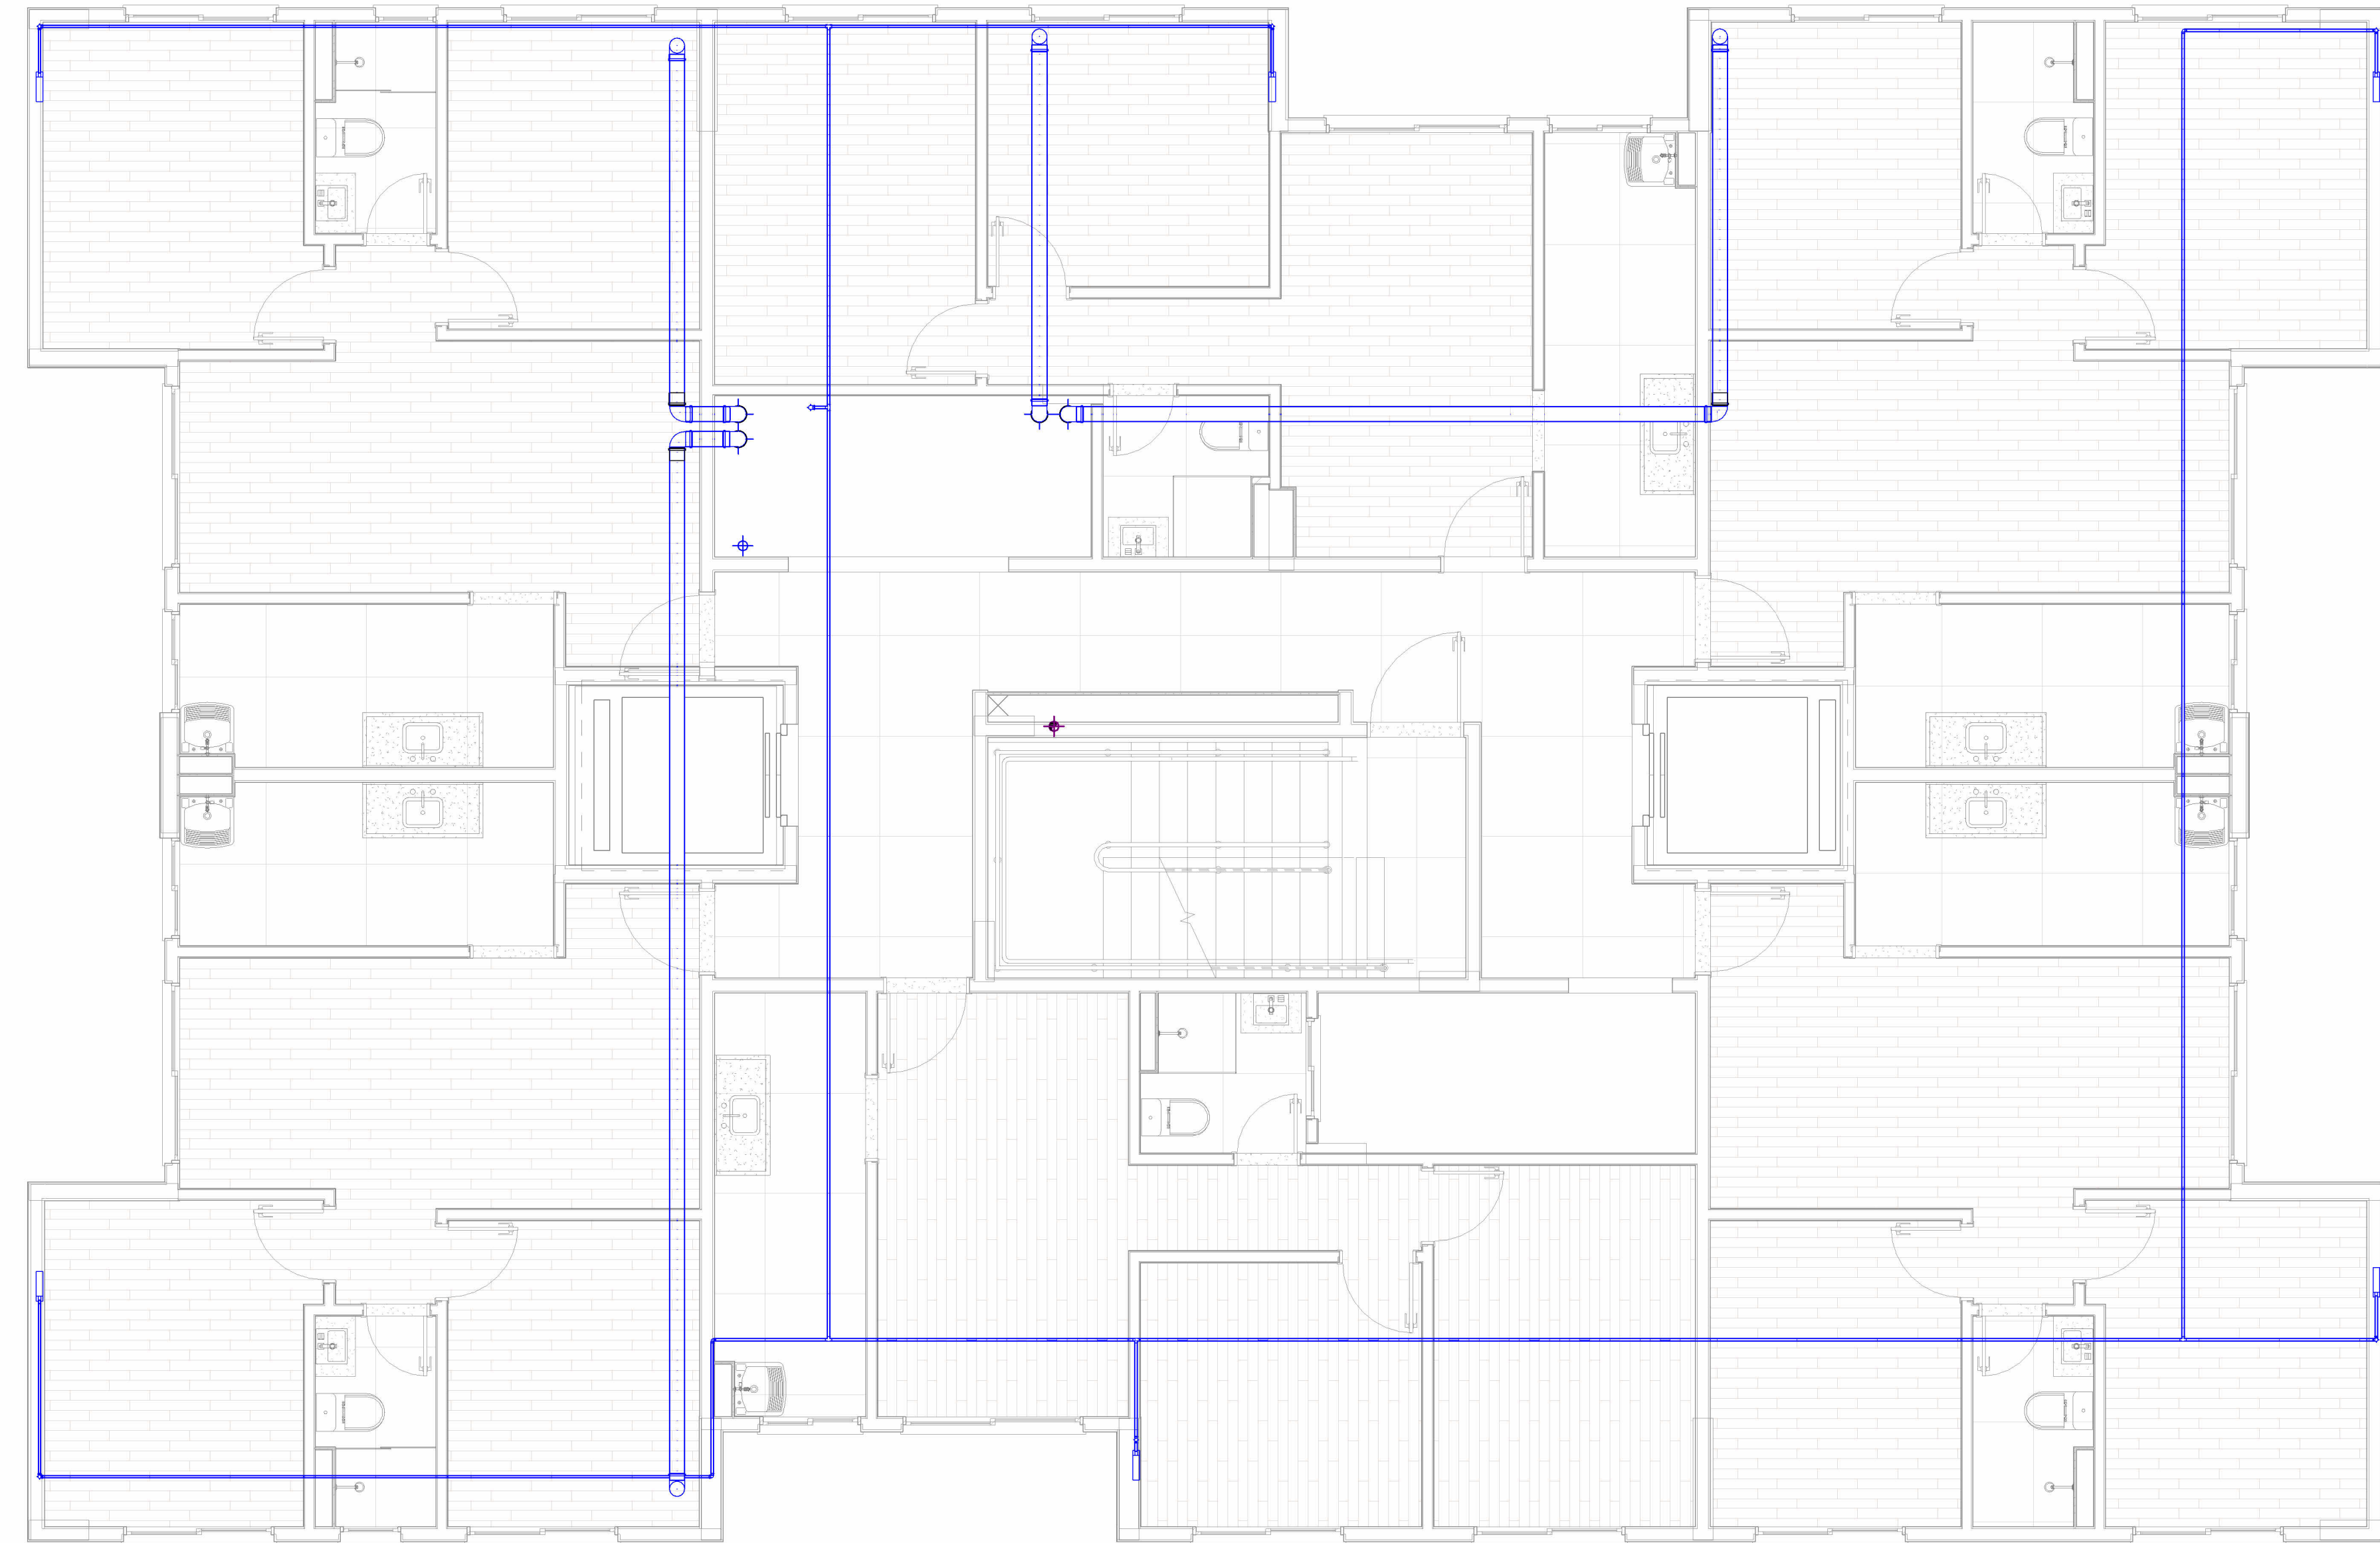

17° Pavimento

1 : 50

LEGENDA:

- TUBULAÇÃO PVC BRANCO SN - ESGOTO PRIMÁRIO
- TUBULAÇÃO PVC BRANCO SN - ESGOTO SECUNDÁRIO
- TUBO DE QUEDA DE ESGOTO PRIMÁRIO

ABREVIações:

RS - RALO SECO

NOTAS:

- DIMENSões E DIâMETROS EM MILIMETROS, EXCETO ONDE INDICADO CONTRÁRIO.
- NOS TRECHOS HORIZONTAIS DAS TUBULAções DE ESGOTO SANITÁRIO RECOMENDAM-SE AS SEGUINTEs DECLIVIDADES MÍNIMAS:
 - 2% PARA TUBULAções COM DIâMETRO NOMINAL IGUAL OU INFERIOR A 75mm;
 - 1% PARA TUBULAções COM DIâMETRO NOMINAL IGUAL OU SUPERIOR A 100mm;
- UTILIZAR ANEIS DE BORRACHA NAS CONEXões DE ESGOTO.
- PROIBIDO UTILIZAR FOGO NAS TUBULAções.
- OS TERMINAIS DE VENTILAÇÃO DOS TUBOS DE VENTILAÇÃO DEVERÃO PASSAR 30CM ACIMA DO TELHADO.
- UTILIZAR DISPOSITIVO ANTI-ESPUMA NA CAIXA SIFONADA DA ÁREA DE SERVIÇO.
- TODAS AS TUBULAções EXPOSTAS DEVERÃO SER FIXADAS COM BRACADEIRA
- A BASE DO RESERVATÓRIO DEVERÁ TER UMA SUPERFÍCIE LISA, NIVELADA E ISENTA DE SUEIRA OU MATERIAIS PONTAGUDOS. A BASE DEVE TER RESISTÊNCIA COMPATIVEL COM O PESO DA CAIXA CHEIA E DEVE SER MAIOR DO QUE A LARGURA DO FUNDO DA CAIXA.

Lista de Materiais - Conexões e Acessórios - Completa

Descrição do Material	Quantidade (peças)
	30
Anel de Borracha, DN150mm, para linha de PVC Rígido Branco Série Normal, conforme NBR 5688	5
Bucha de Redução Curta, DN32x25mm, PVC Marrom Soldável, conforme NBR 5648	1
Joelho 90°, DN25mm, PVC Marrom Soldável, conforme NBR 5648	15
Joelho 90°, DN32mm, PVC Marrom Soldável, conforme NBR 5648	1
Joelho 90°, DN150mm, de PVC Rígido Branco Série Normal, conforme NBR 5688	11
Luva Simples, DN150mm, de PVC Rígido Branco Série Normal, conforme NBR 5688	7
Tê, DN25mm, PVC Marrom Soldável, conforme NBR 5648	5

Lista de Materiais - Tubos

Descrição do Material	Diâmetro Nominal (mm)	Comprimento (m)	Referência de Fabricante
Tubo de PVC Rígido Branco, conforme NBR5688, Linha Série Normal	Ø150	268,07	Tigre
Tubo de PVC Rígido Branco, conforme NBR5688, Linha Série Normal	Ø100	127,35	Tigre
Tubo de PVC Rígido Soldável Marrom, conforme NBR 5648	Ø32	3,25	Tigre
Tubo de PVC Rígido Soldável Marrom, conforme NBR 5648	Ø25	61,36	Tigre




PENN & WIZE
INSTALAÇÕES PREDIAIS
<https://pennwize.github.io/>



PROJETO: Edifício Derry and Georgie
LOCAL: Rua dos bobos, nº 0. Natal/RN - Brasil
ASSUNTO: Folha - 17° Pavimento
AUTORES DO PROJETO: Amanda João Pedro Melo e Letícia Tórres

FOLHA: P02
REV.:
ESCALA: 1 : 50
DATA: 10/02/26

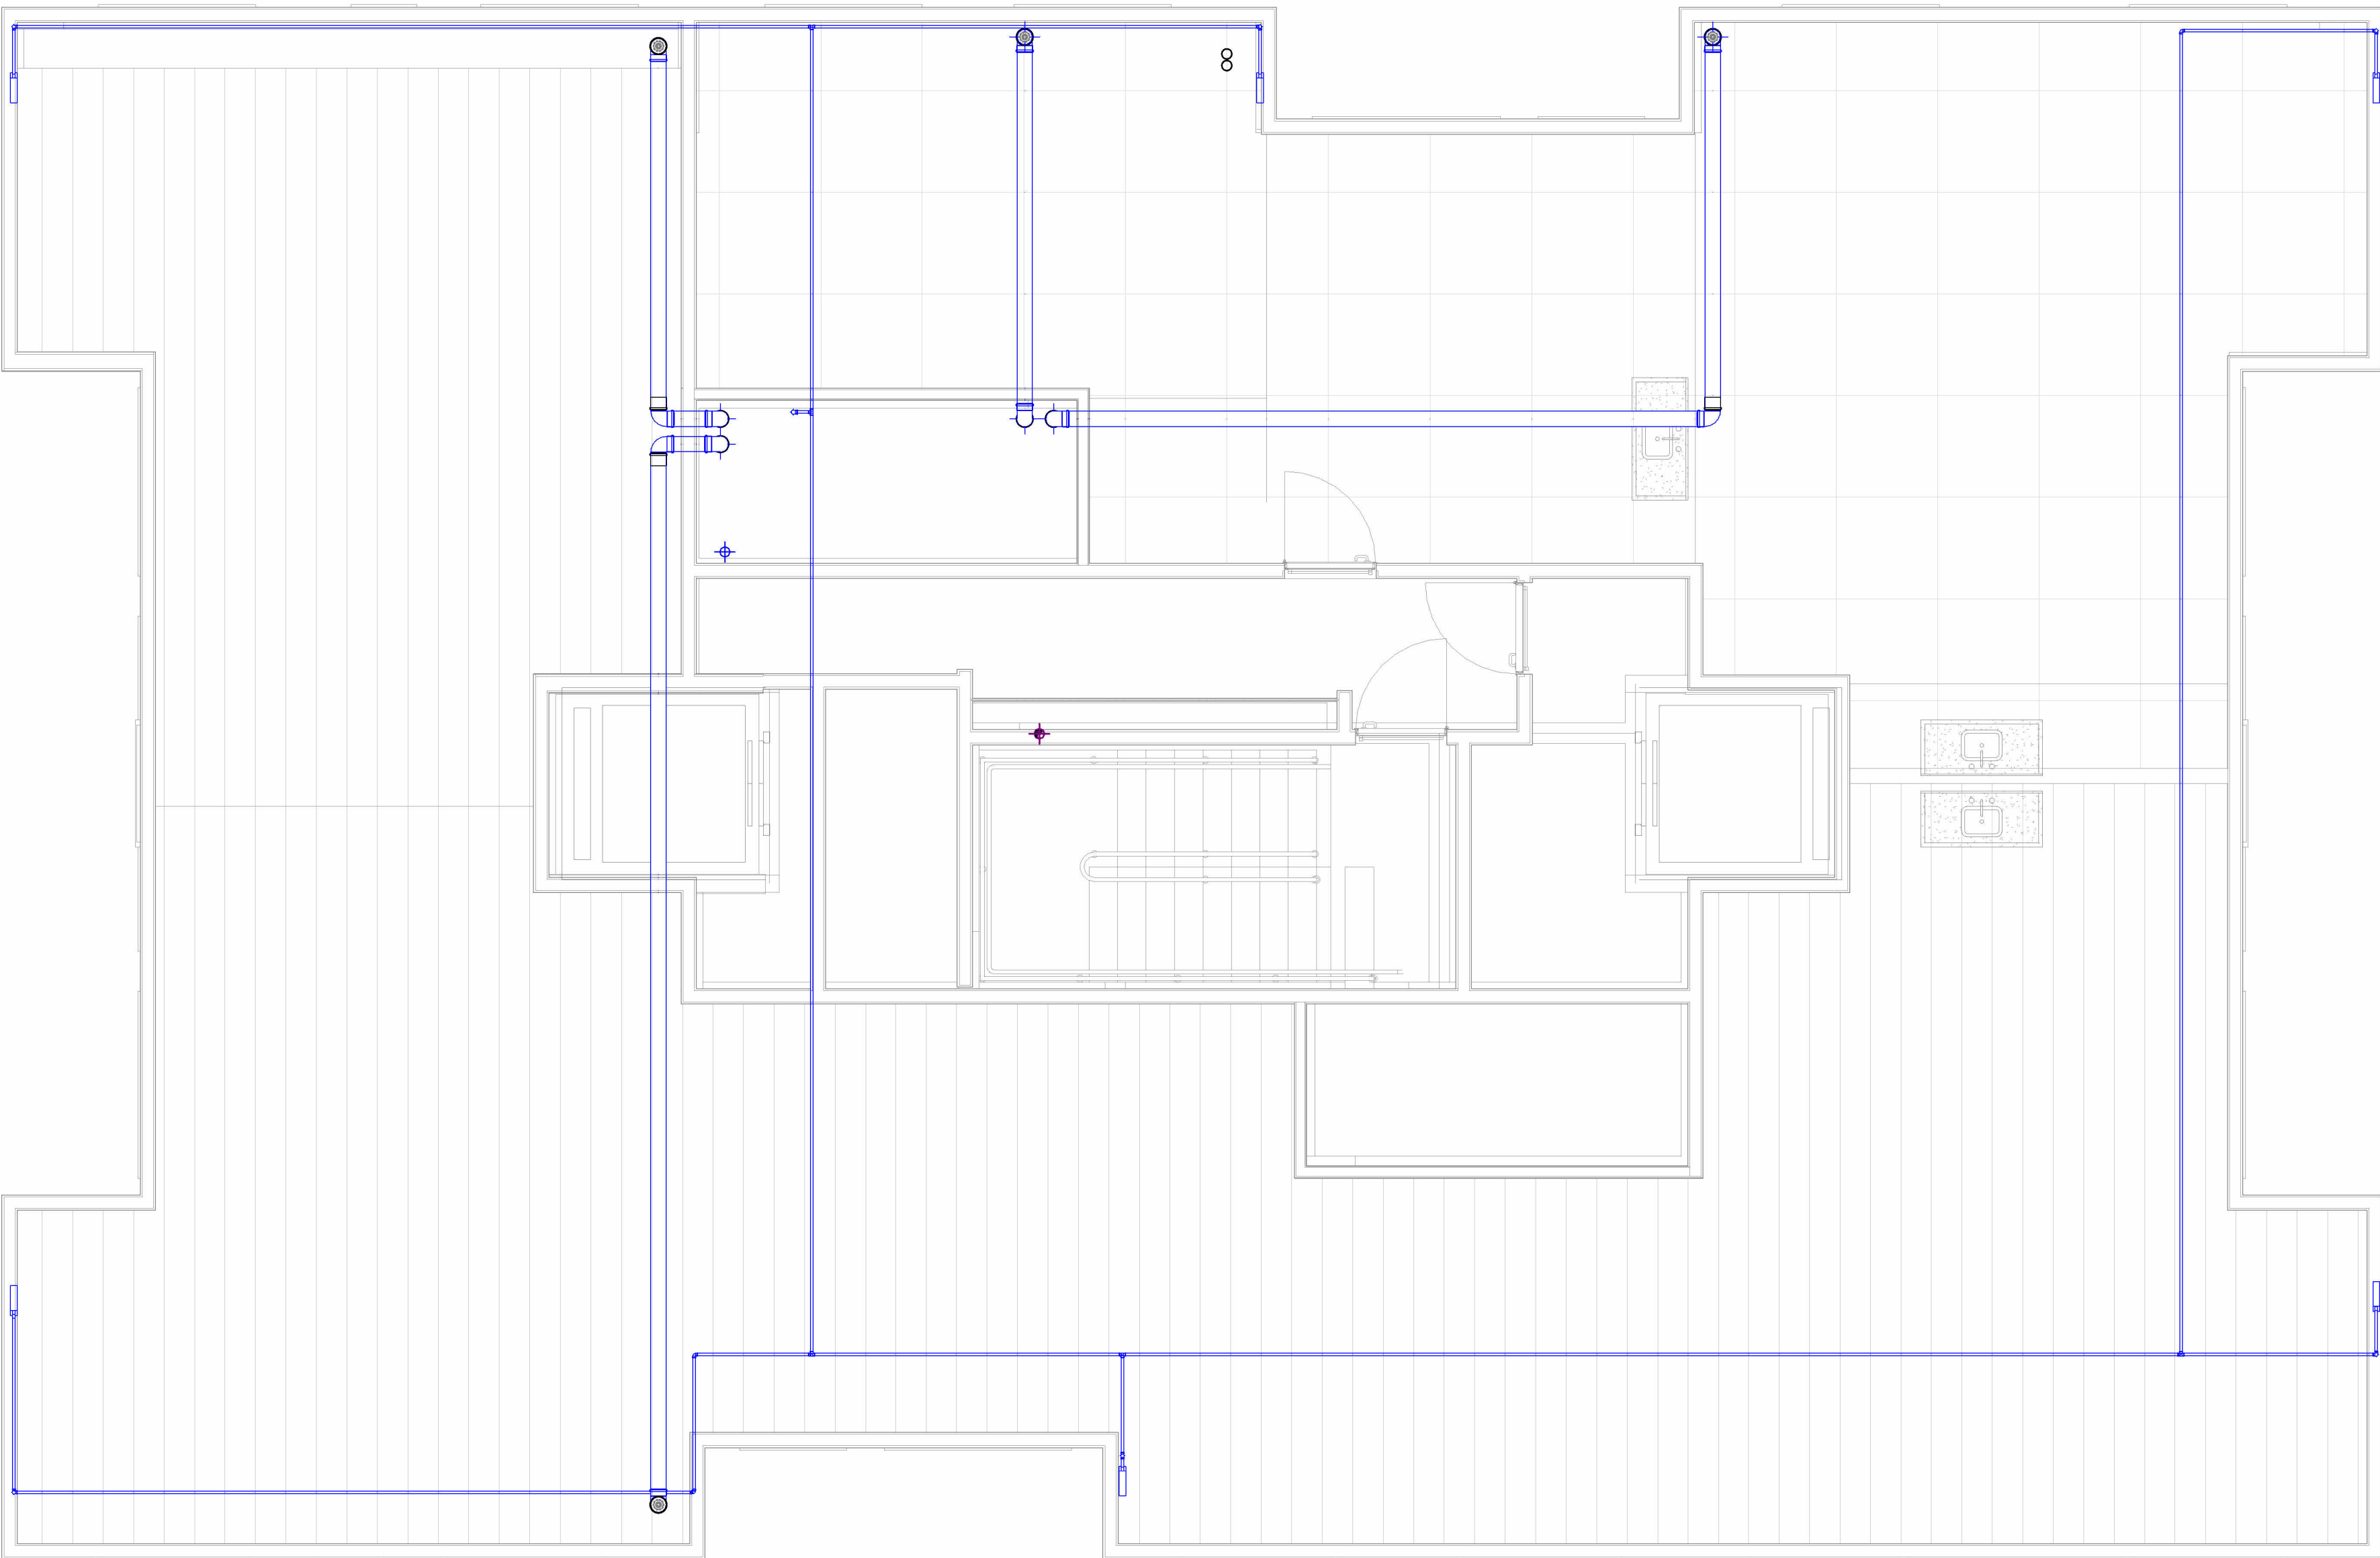

Cobertura/Resgate

1 : 50

LEGENDA:

- TUBULAÇÃO PVC BRANCO SN - ESGOTO PRIMÁRIO
- TUBULAÇÃO PVC BRANCO SN - ESGOTO SECUNDÁRIO
- TUBO DE QUEDA DE ESGOTO PRIMÁRIO

ABREVIações:

RS - RALO SECO

NOTAS:

- DIMENSões E DIâMETROS EM MILIMETROS, EXCETO ONDE INDICADO CONTRÁRIO.
- NOS TRECHOS HORIZONTAIS DAS TUBULAções DE ESGOTO SANITÁRIO RECOMENDAM-SE AS SEGUINTEs DECLIVIDADES MÍNIMAS:
 - 2% PARA TUBULAções COM DIâMETRO NOMINAL IGUAL OU INFERIOR A 75mm;
 - 1% PARA TUBULAções COM DIâMETRO NOMINAL IGUAL OU SUPERIOR A 100mm;
- UTILIZAR ANEIS DE BORRACHA NAS CONEXões DE ESGOTO.
- PROIBIDO UTILIZAR FOGO NAS TUBULAções.
- OS TERMINAIS DE VENTILAÇÃO DOS TUBOS DE VENTILAÇÃO DEVERÃO PASSAR 30CM ACIMA DO TELHADO.
- UTILIZAR DISPOSITIVO ANTI-ESPUMA NA CAIXA SIFONADA DA ÁREA DE SERVIÇO.
- TODAS AS TUBULAções EXPOSTAS DEVERÃO SER FIXADAS COM BRACADEIRA
- A BASE DO RESERVATÓRIO DEVERÁ TER UMA SUPERFÍCIE LISA, NIVELADA E ISENTA DE SUEIRA OU MATERIAIS PONTAGUDOS. A BASE DEVE TER RESISTÊNCIA COMPATIVEL COM O PESO DA CAIXA CHEIA E DEVE SER MAIOR DO QUE A LARGURA DO FUNDO DA CAIXA.

Lista de Materiais - Conexões e Acessórios - Completa

Descrição do Material	Quantidade (peças)
	36
Anel de Borracha, DN150mm, para linha de PVC Rígido Branco Série Normal, conforme NBR 5688	22
Bucha de Redução Curta, DN32x25mm, PVC Marrom Soldável, conforme NBR 5648	1
Joelho 90°, DN25mm, PVC Marrom Soldável, conforme NBR 5648	15
Joelho 90°, DN32mm, PVC Marrom Soldável, conforme NBR 5648	1
Joelho 90°, DN150mm, de PVC Rígido Branco Série Normal, conforme NBR 5688	11
Luva Simples, DN150mm, de PVC Rígido Branco Série Normal, conforme NBR 5688	11
Tê, DN25mm, PVC Marrom Soldável, conforme NBR 5648	5

Lista de Materiais - Tubos

Descrição do Material	Diâmetro Nominal (mm)	Comprimento (m)	Referência de Fabricante
Tubo de PVC Rígido Branco, conforme NBR5688, Linha Série Normal	Ø150	268,39	Tigre
Tubo de PVC Rígido Branco, conforme NBR5688, Linha Série Normal	Ø100	127,35	Tigre
Tubo de PVC Rígido Soldável Marrom, conforme NBR 5648	Ø32	3,25	Tigre
Tubo de PVC Rígido Soldável Marrom, conforme NBR 5648	Ø25	61,36	Tigre



PENN & WIZE
INSTALAÇÕES PREDIAIS
<https://pennwize.github.io/>



PROJETO: Edifício Derry and Georgie

LOCAL: Rua dos bobos, nº 0. Natal/RN - Brasil

ASSUNTO: Folha - Cobertura/Resgate

AUTORES DO PROJETO:
Amanda João Pedro Melo e Letícia Tórres

FOLHA:

P03

REV.:

ESCALA:

1 : 50

DATA:

10/02/26




Elevação Reservatório Superior

1 : 50



Reservatório Fundo

1 : 50

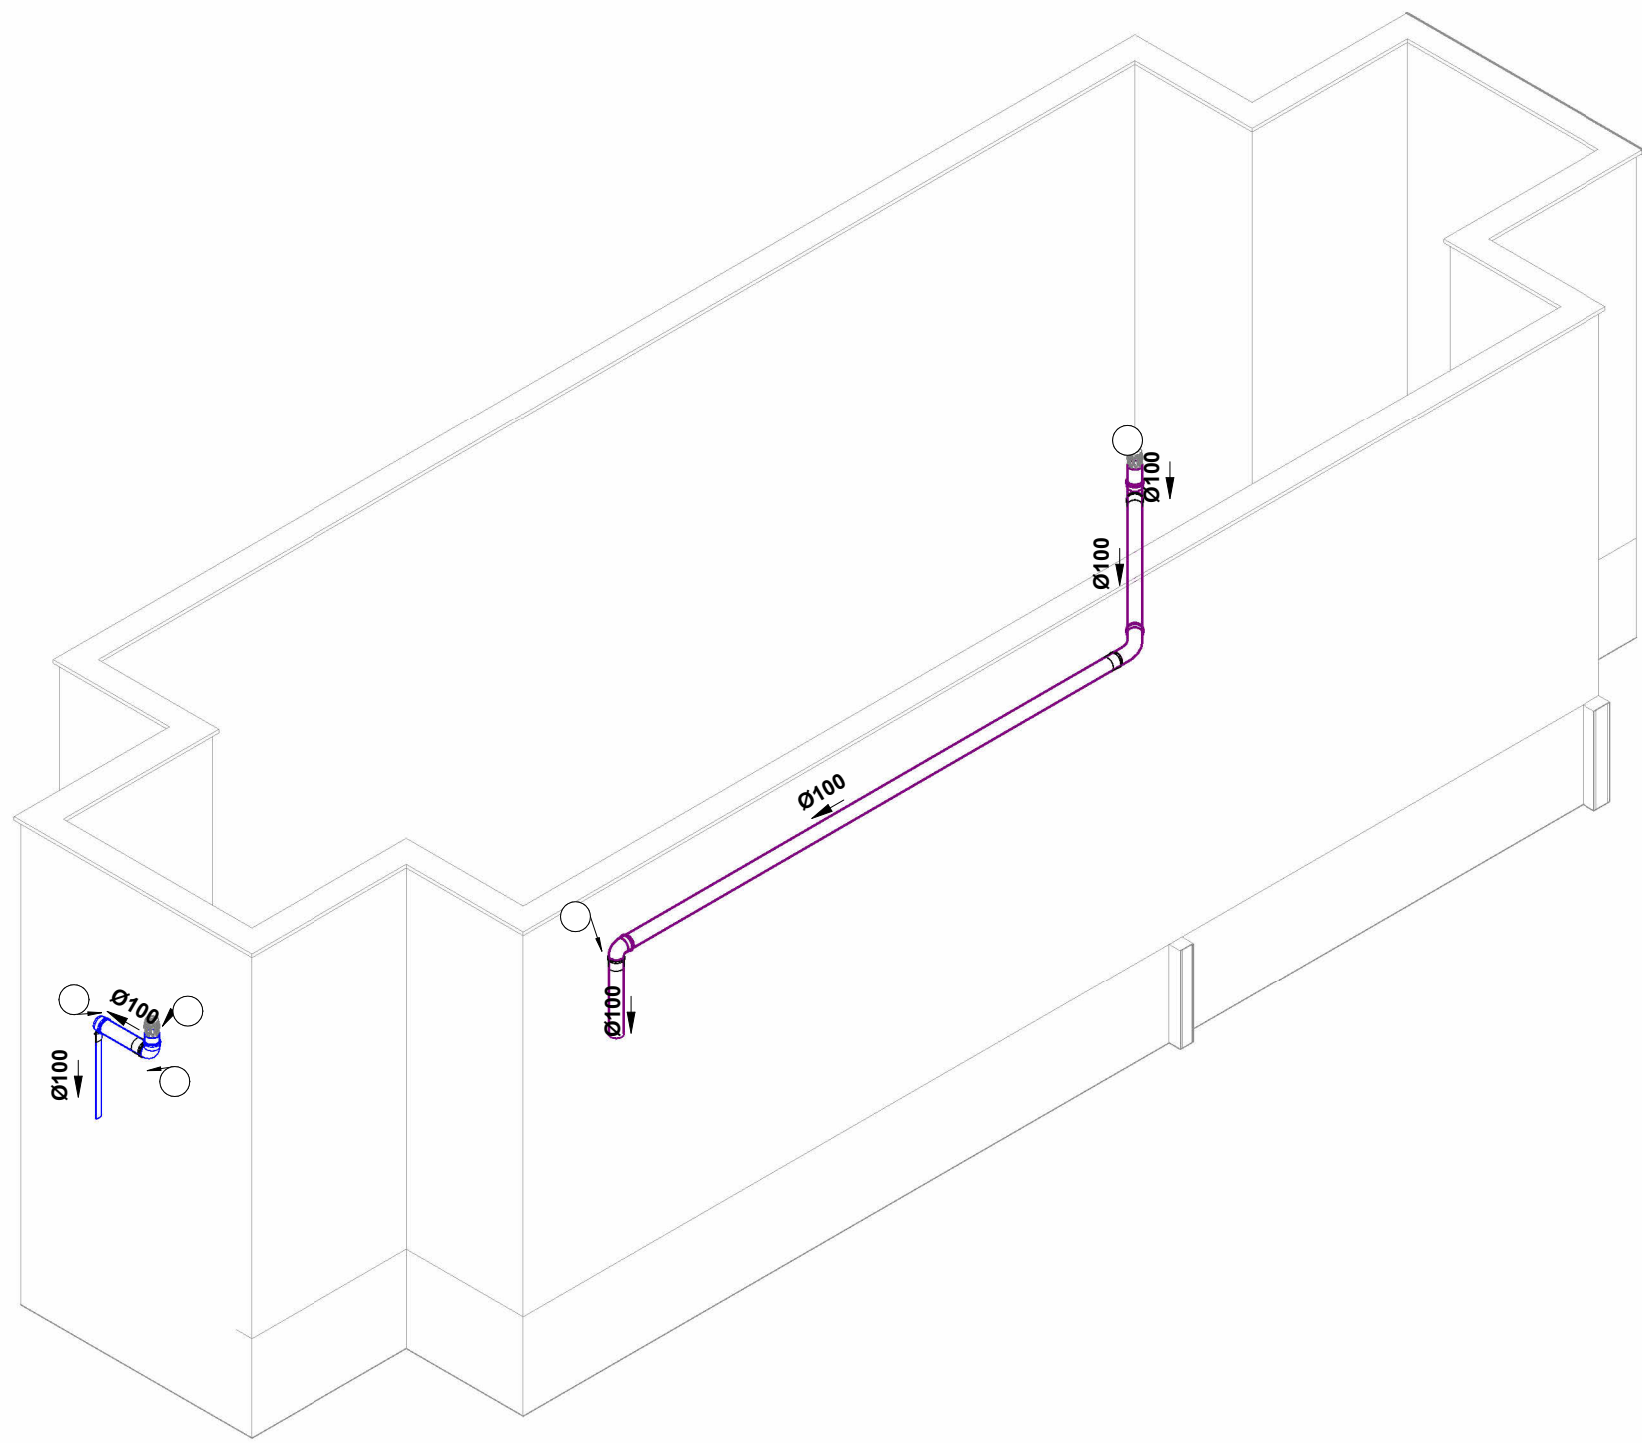

ISO - Reservatório Superior

LEGENDA:

- TUBULAÇÃO PVC BRANCO SN - ESGOTO PRIMÁRIO
- TUBULAÇÃO PVC BRANCO SN - ESGOTO SECUNDÁRIO
- TUBO DE QUEDA DE ESGOTO PRIMÁRIO

ABREVIações:

RS - RALO SECO

NOTAS:

- DIMENSÕES E DIÂMETROS EM MILÍMETROS, EXCETO ONDE INDICADO CONTRÁRIO.
- NOS TRECHOS HORIZONTAIS DAS TUBULAÇÕES DE ESGOTO SANITÁRIO RECOMENDAM-SE AS SEGUINTEs DECLIVIDADES MÍNIMAS:
 - 2% PARA TUBULAÇÕES COM DIÂMETRO NOMINAL IGUAL OU INFERIOR A 75mm;
 - 1% PARA TUBULAÇÕES COM DIÂMETRO NOMINAL IGUAL OU SUPERIOR A 100mm;
- UTILIZAR ANEIS DE BORRACHA NAS CONEXÕES DE ESGOTO.
- PROIBIDO UTILIZAR FOGO NAS TUBULAÇÕES.
- OS TERMINAIS DE VENTILAÇÃO DOS TUBOS DE VENTILAÇÃO DEVERÃO PASSAR 30CM ACIMA DO TELHADO.
- UTILIZAR DISPOSITIVO ANTI-ESPUMA NA CAIXA SIFONADA DA ÁREA DE SERVIÇO.
- TODAS AS TUBULAÇÕES EXPOSTAS DEVERÃO SER FIXADAS COM BRACADEIRA.
- A BASE DO RESERVATÓRIO DEVERÁ TER UMA SUPERFÍCIE LISA, NIVELADA E ISENTA DE SUEIRA OU MATERIAIS PONTAGUDOS. A BASE DEVE TER RESISTÊNCIA COMPATIVEL COM O PESO DA CAIXA CHEIA E DEVE SER MAIOR DO QUE A LARGURA DO FUNDO DA CAIXA.

Lista de Materiais - Conexões e Acessórios - Completa

Descrição do Material	Quantidade (peças)
	23
Anel de Borracha, DN100mm, para linha de PVC Rígido Branco Série Normal, conforme NBR 5688	10
Curva Longa 45°, DN100mm, de PVC Rígido Branco Série Normal, conforme NBR 5688	1
Joelho 90°, DN100mm, de PVC Rígido Branco Série Normal, conforme NBR 5688	4
Luva Simples, DN100mm, de PVC Rígido Branco Série Normal, conforme NBR 5688	5

Lista de Materiais - Tubos


Descrição do Material	Diâmetro Nominal (mm)	Comprimento (m)	Referência de Fabricante
Tubo de PVC Rígido Branco, conforme NBR5688, Linha Série Normal	Ø100	134,90	Tigre




PENN & WIZE
INSTALAÇÕES PREDIAIS
<https://pennwize.github.io/>




PROJETO:	Edifício Derry and Georgie	FOLHA:	P04
LOCAL:	Rua dos bobos, nº 0. Natal/RN - Brasil	REV.:	ESCALA:
ASSUNTO:	Folha - Reservatório		1 : 50
AUTORES DO PROJETO:	Amanda João Pedro Melo e Letícia Tórres	DATA:	10/02/26

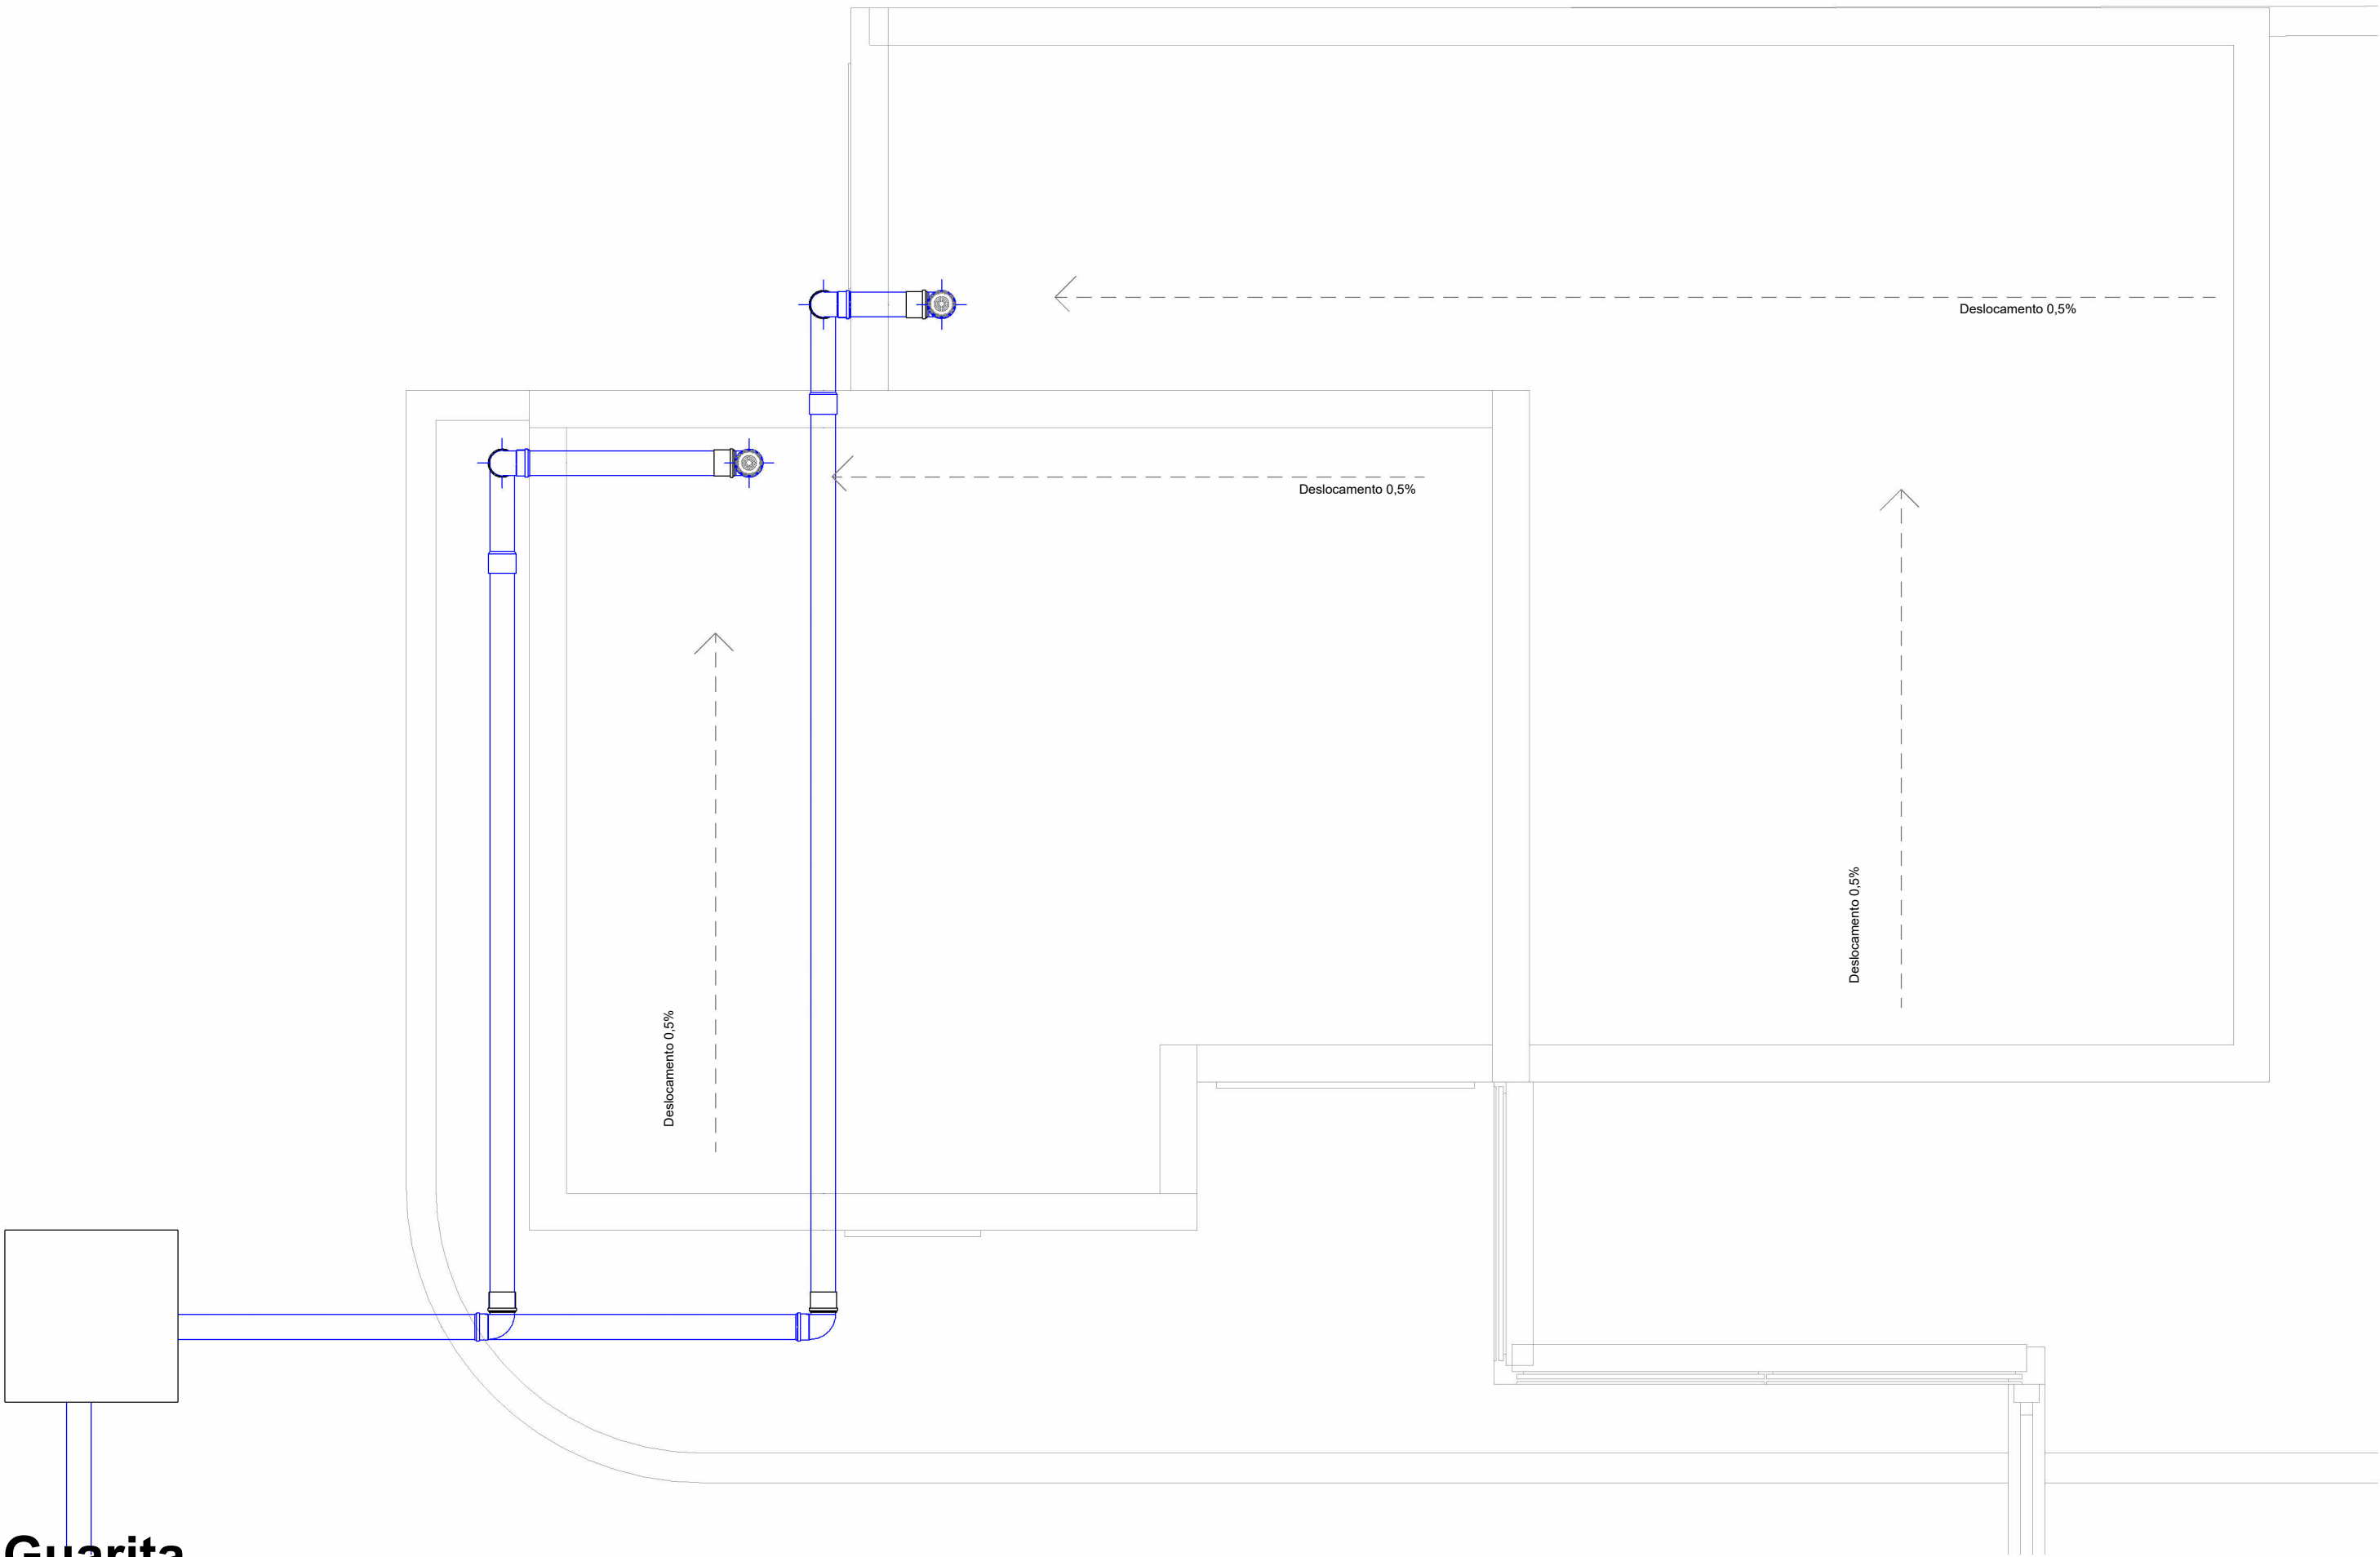

Guarita
1 : 25

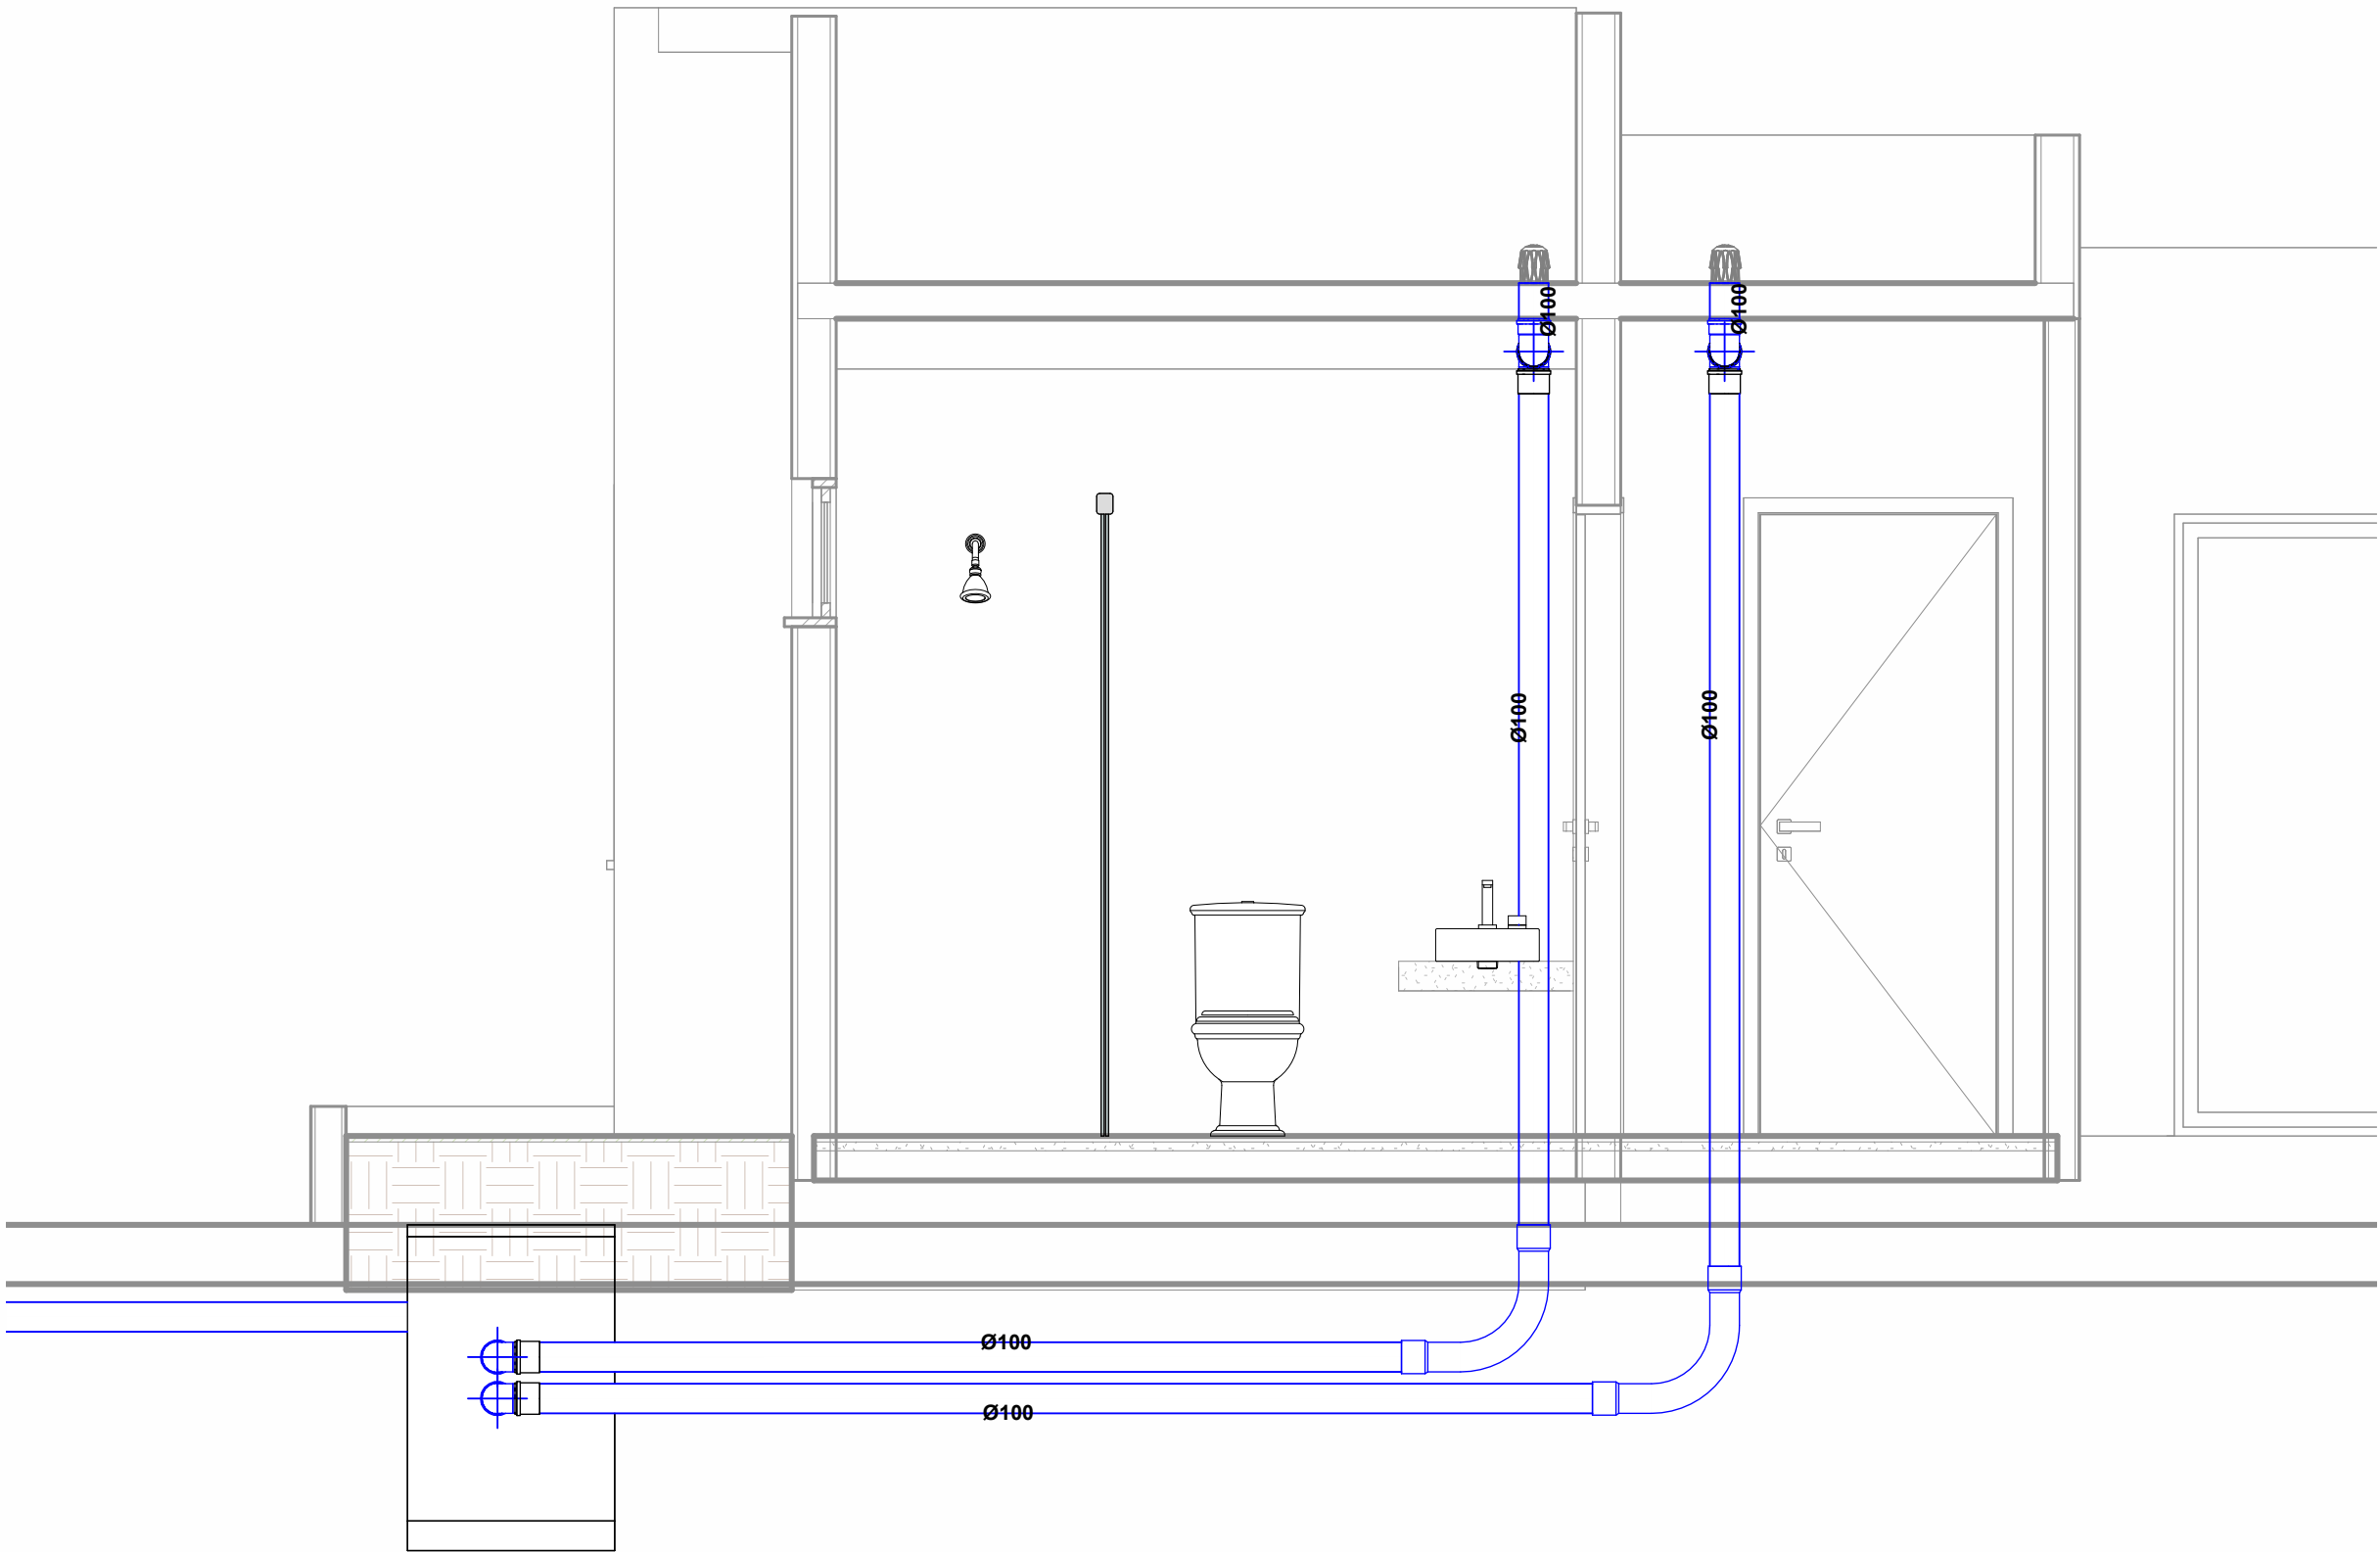

Elevação Guarita
1 : 25

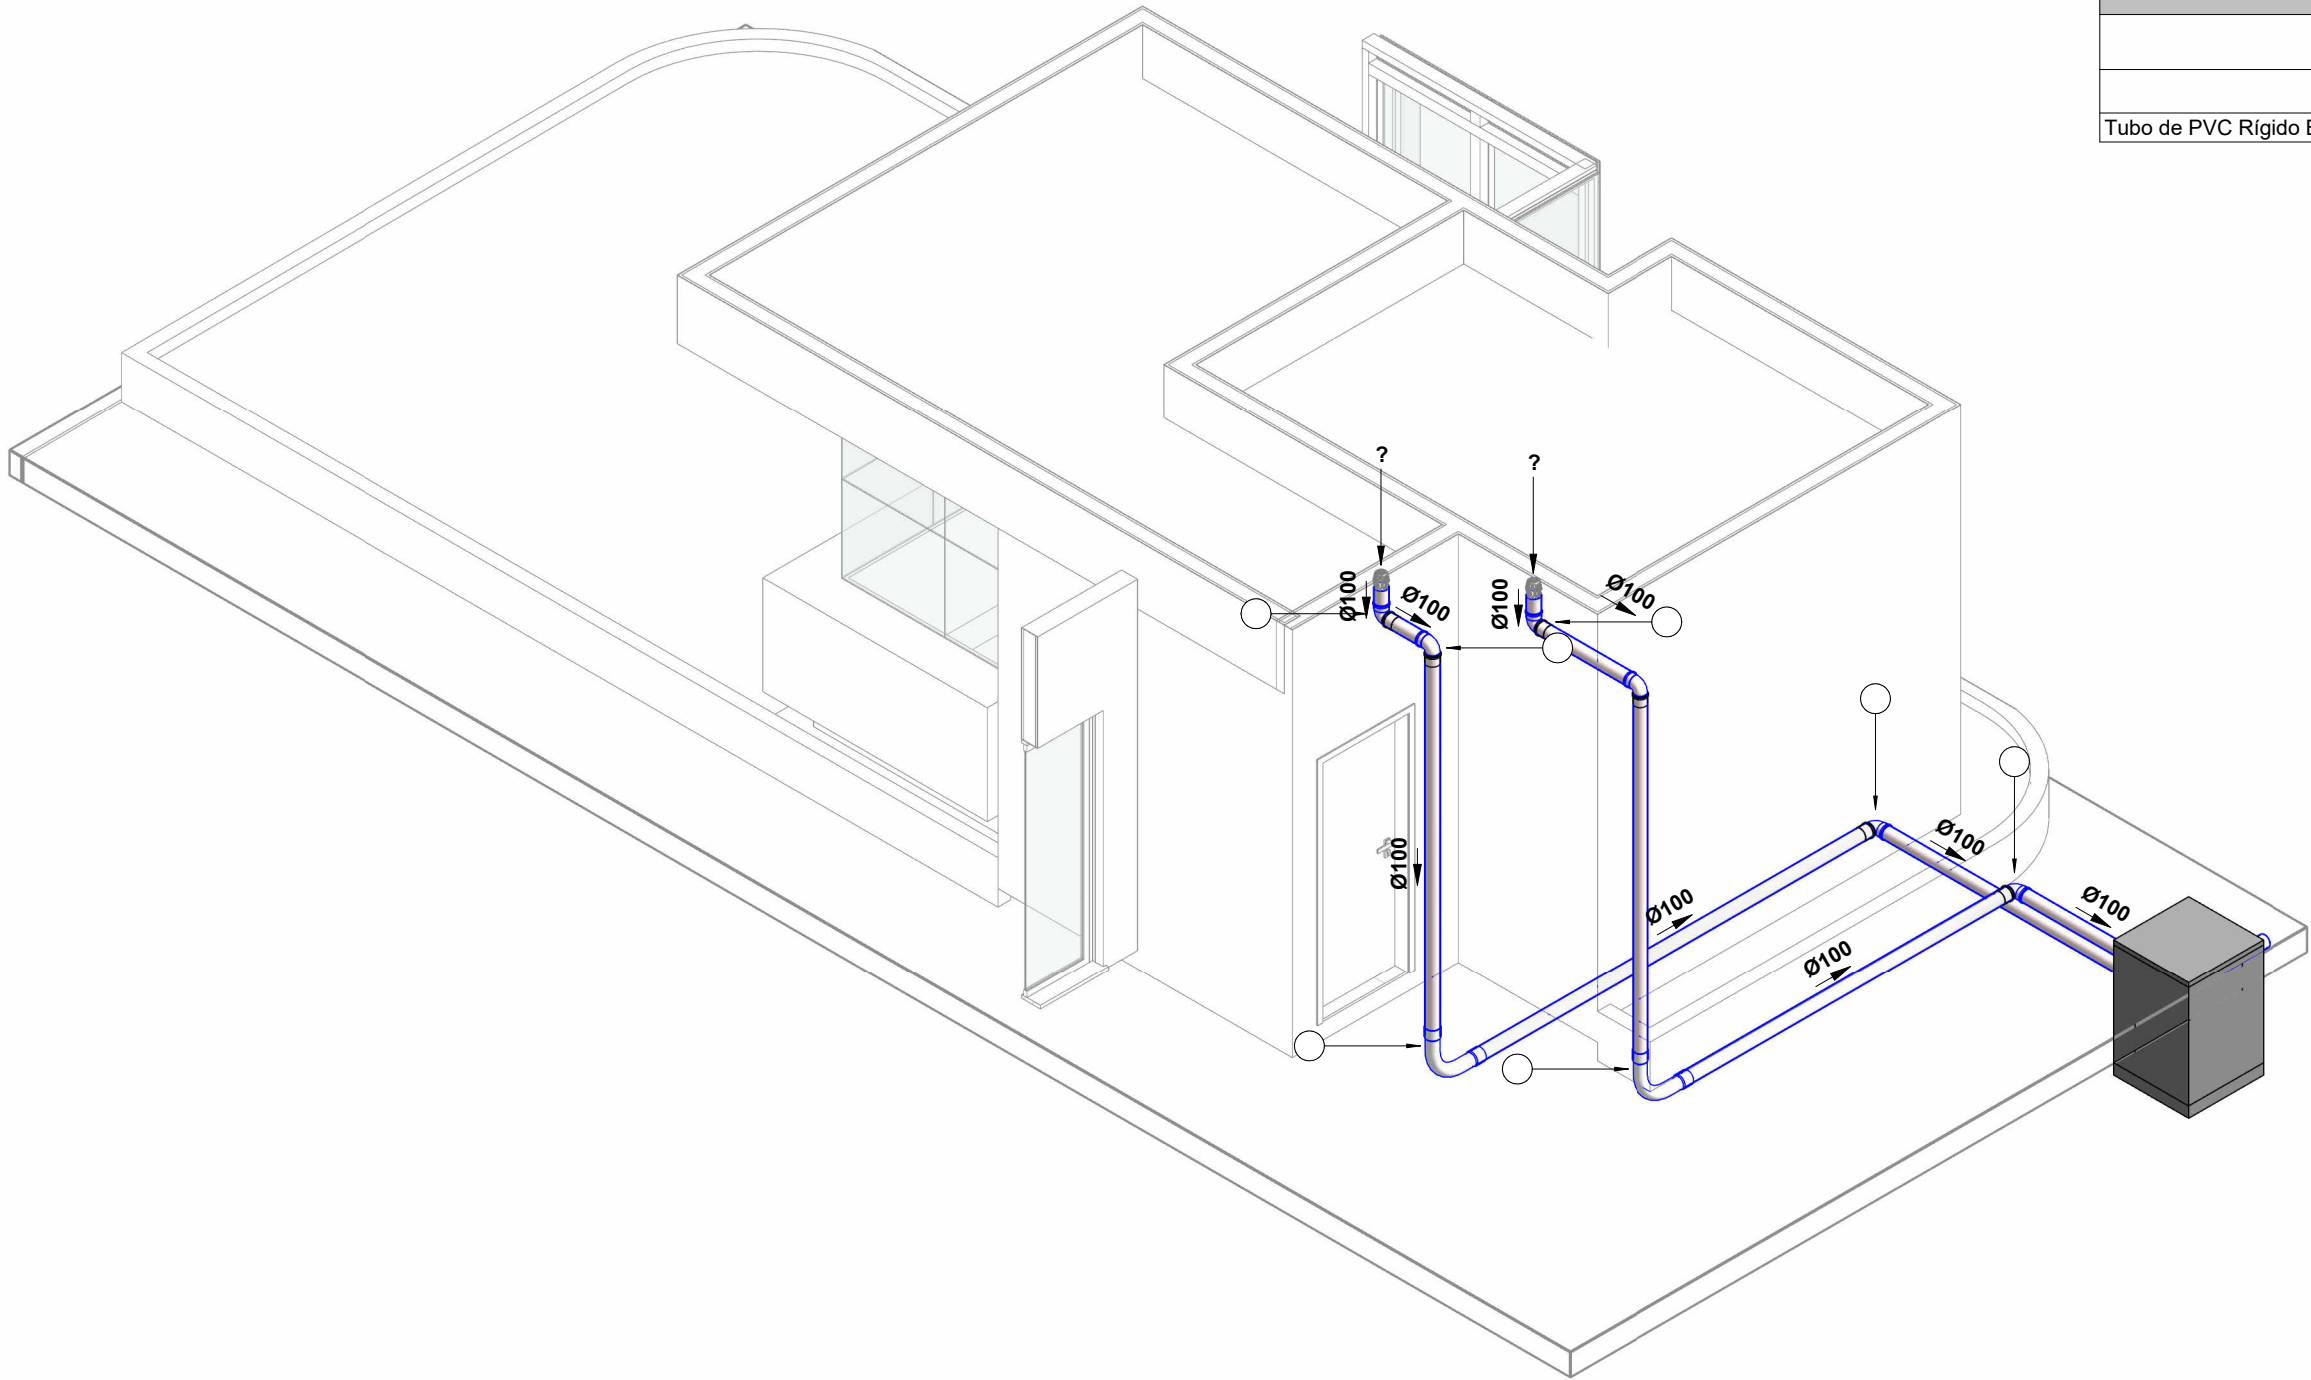

ISO - Guarita

LEGENDA:

- TUBULAÇÃO PVC BRANCO SN - ESGOTO PRIMÁRIO
- TUBULAÇÃO PVC BRANCO SN - ESGOTO SECUNDÁRIO
- TUBO DE QUEDA DE ESGOTO PRIMÁRIO

ABREVIações:

RS - RALO SECO

NOTAS:

- DIMENSÕES E DIÂMETROS EM MILÍMETROS, EXCETO ONDE INDICADO CONTRÁRIO.
- NOS TRECHOS HORIZONTAIS DAS TUBULAÇÕES DE ESGOTO SANITÁRIO RECOMENDAM-SE AS SEGUINTEs DECLIVIDADES MÍNIMAS:
 - 2% PARA TUBULAÇÕES COM DIÂMETRO NOMINAL IGUAL OU INFERIOR A 75mm;
 - 1% PARA TUBULAÇÕES COM DIÂMETRO NOMINAL IGUAL OU SUPERIOR A 100mm;
- UTILIZAR ANEIS DE BORRACHA NAS CONEXÕES DE ESGOTO.
- PROIBIDO UTILIZAR FOGO NAS TUBULAÇÕES.
- OS TERMINAIS DE VENTILAÇÃO DOS TUBOS DE VENTILAÇÃO DEVERÃO PASSAR 30CM ACIMA DO TELHADO.
- UTILIZAR DISPOSITIVO ANTI-ESPUMA NA CAIXA SIFONADA DA ÁREA DE SERVIÇO.
- TODAS AS TUBULAÇÕES EXPOSTAS DEVERÃO SER FIXADAS COM BRACADEIRA.
- A BASE DO RESERVATÓRIO DEVERÁ TER UMA SUPERFÍCIE LISA, NIVELADA E ISENTA DE SUEIRA OU MATERIAIS PONTAGUDOS. A BASE DEVE TER RESISTÊNCIA COMPATÍVEL COM O PESO DA CAIXA CHEIA E DEVE SER MAIOR DO QUE A LARGURA DO FUNDO DA CAIXA.

Lista de Materiais - Conexões e Acessórios - Completa

Descrição do Material	Quantidade (peças)
	6
Anel de Borracha, DN100mm, para linha de PVC Rígido Branco Série Normal, conforme NBR 5688	12
Joelho 90°, DN100mm, de PVC Rígido Branco Série Normal, conforme NBR 5688	6
Luva Simples, DN100mm, de PVC Rígido Branco Série Normal, conforme NBR 5688	6
Produto Inexistente	2

Lista de Materiais - Tubos


Descrição do Material	Diâmetro Nominal (mm)	Comprimento (m)	Referência de Fabricante
Tubo de PVC Rígido Branco, conforme NBR5688, Linha Série Normal	Ø100	41,88	Tigre



PENN & WIZE
INSTALAÇÕES PREDIAIS
<https://pennwize.github.io/>



PROJETO:	Edifício Derry and Georgie	FOLHA:	P05
LOCAL:	Rua dos bobos, nº 0. Natal/RN - Brasil	REV.:	Como indicada
ASSUNTO:	Folha - Guarita	DATA:	10/02/26
AUTORES DO PROJETO:	Amanda João Pedro Melo e Letícia Tórres		

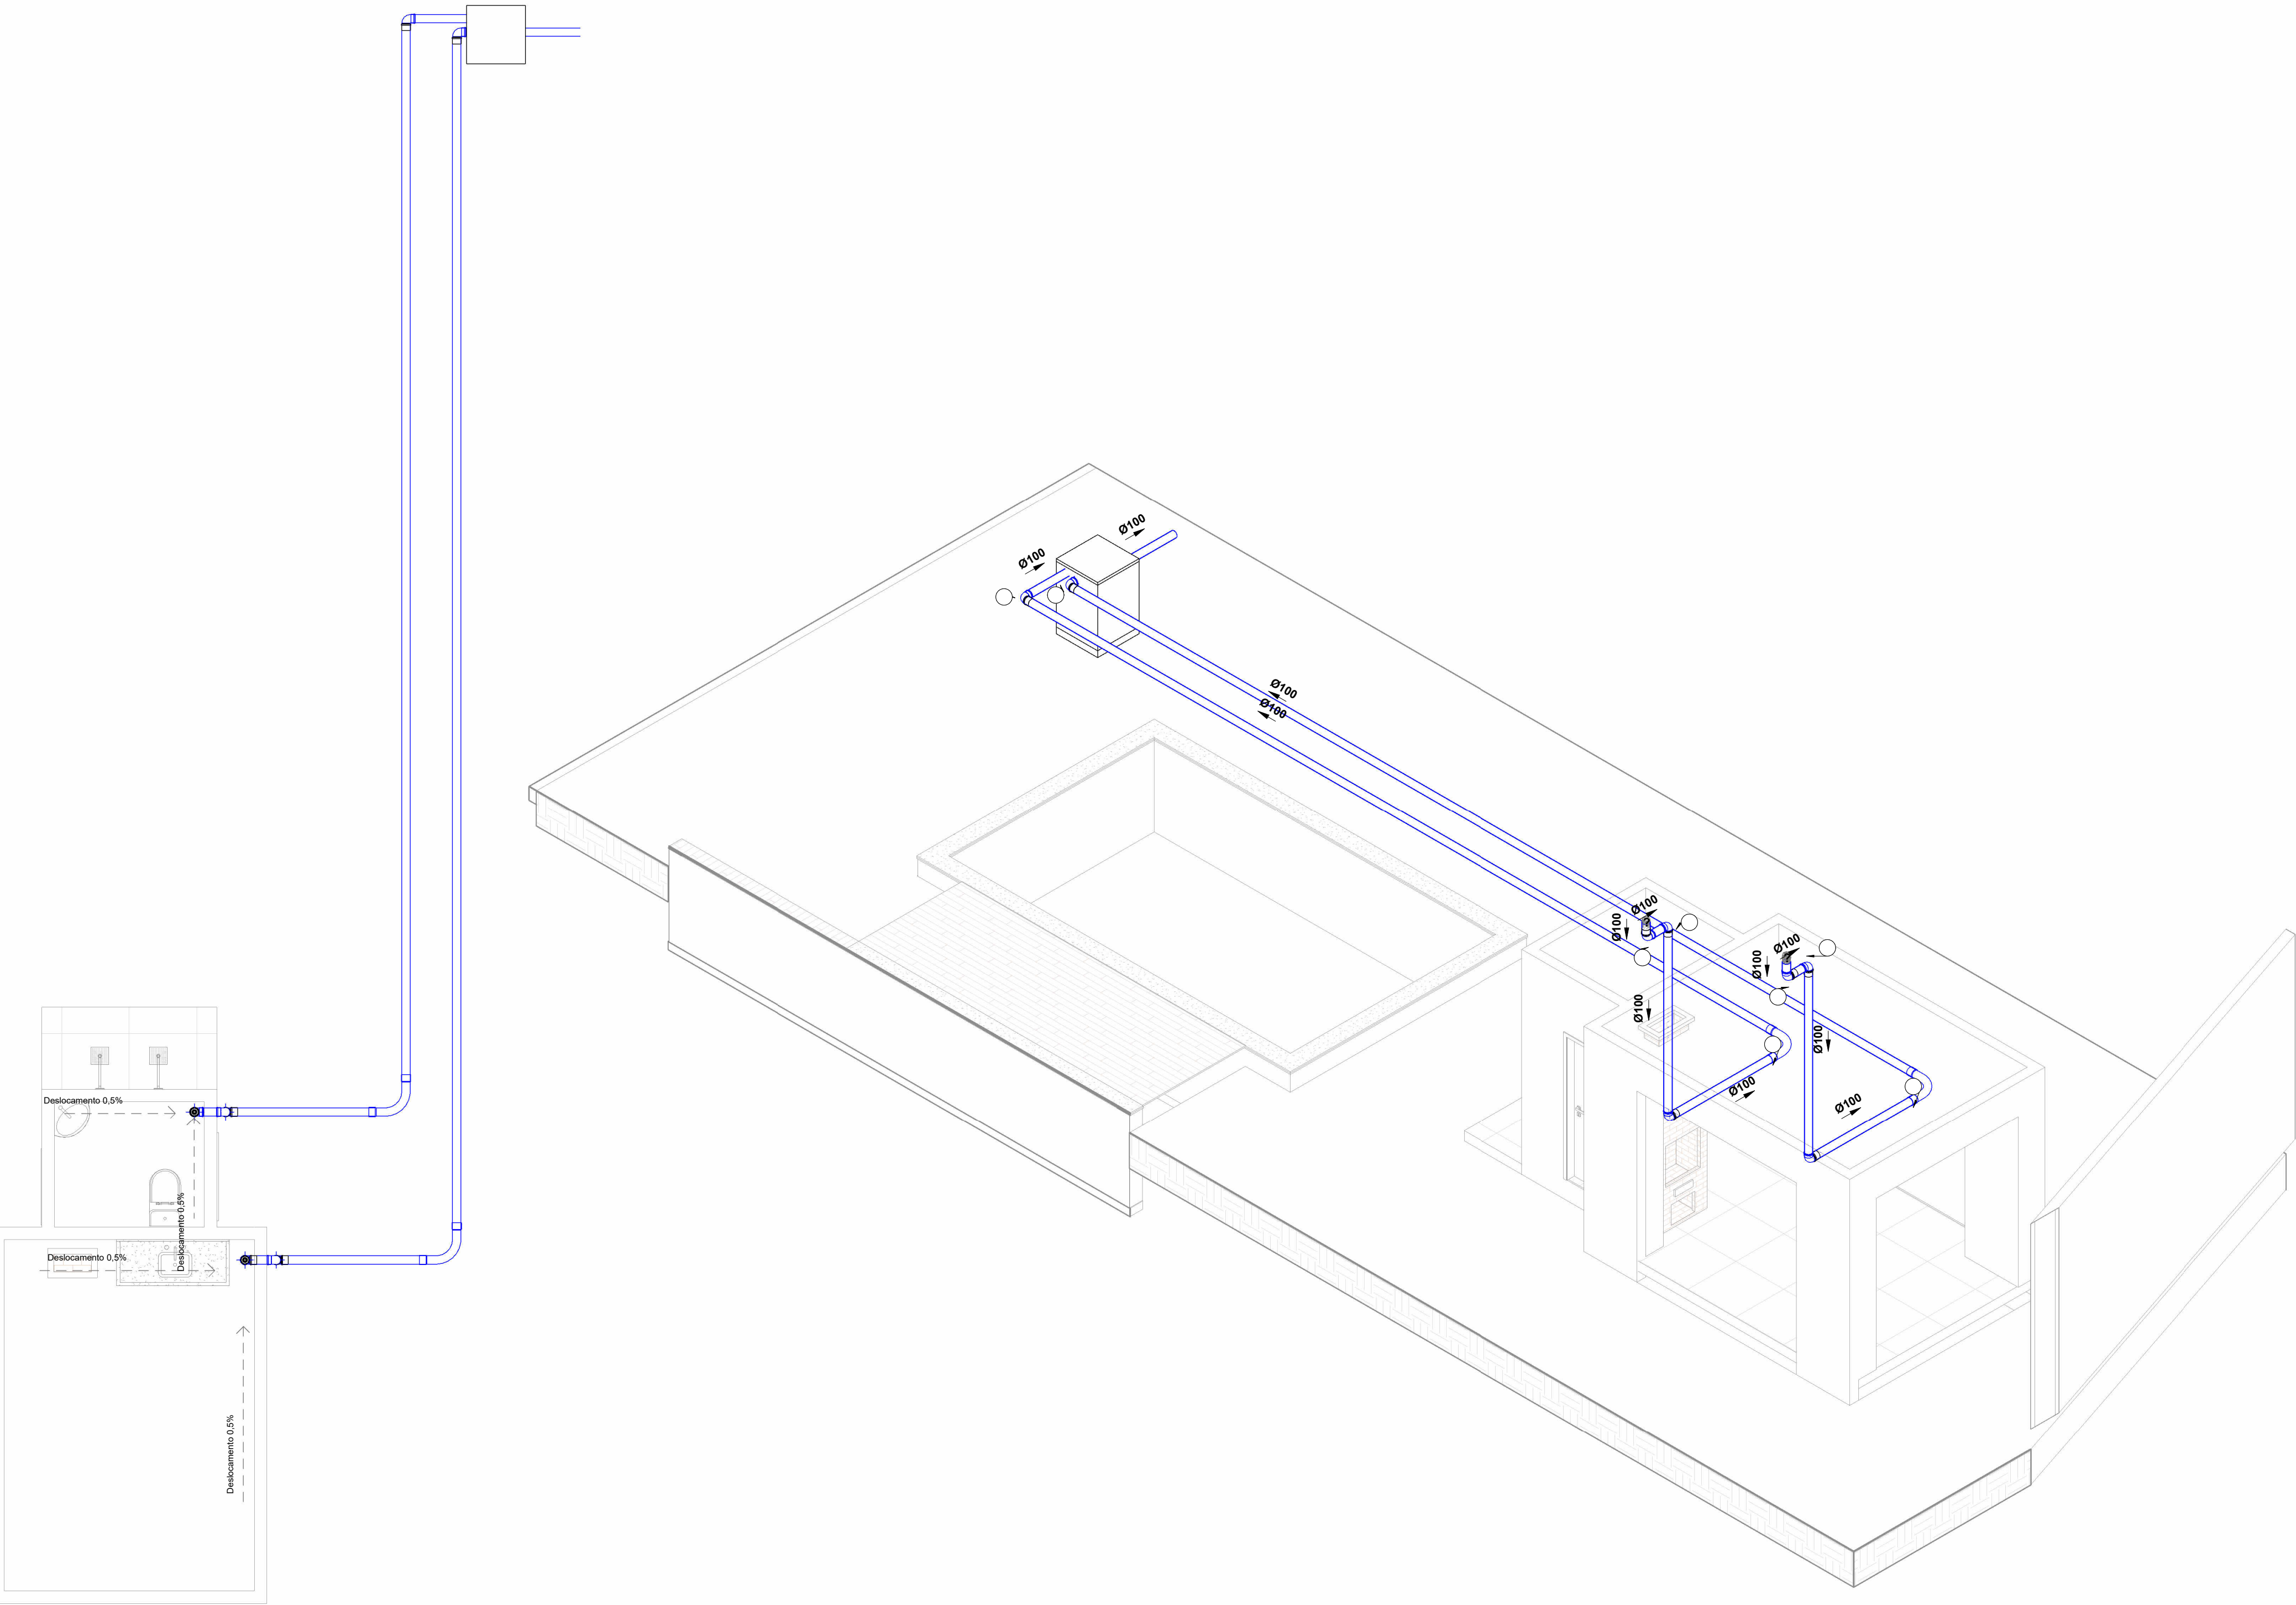

Churrasqueira
1 : 50

ISO - Churrasqueira

LEGENDA:

- TUBULAÇÃO PVC BRANCO SN - ESGOTO PRIMÁRIO
- TUBULAÇÃO PVC BRANCO SN - ESGOTO SECUNDÁRIO
- TUBO DE QUEDA DE ESGOTO PRIMÁRIO

ABREVIações:

RS - RALO SECO

NOTAS:

- 1 - DIMENSÕES E DIÂMETROS EM MILÍMETROS, EXCETO ONDE INDICADO CONTRÁRIO.
- 2 - NOS TRECHOS HORIZONTAIS DAS TUBULAÇÕES DE ESGOTO SANITÁRIO RECOMENDAM-SE AS SEGUINTEs DECLIVIDADES MÍNIMAS:
 - 2% PARA TUBULAÇÕES COM DIÂMETRO NOMINAL IGUAL OU INFERIOR A 75mm;
 - 1% PARA TUBULAÇÕES COM DIÂMETRO NOMINAL IGUAL OU SUPERIOR A 100mm;
- 3 - UTILIZAR ANEIS DE BORRACHA NAS CONEXÕES DE ESGOTO.
- 4 - PROIBIDO UTILIZAR FOGO NAS TUBULAÇÕES.
- 5 - OS TERMINAIS DE VENTILAÇÃO DOS TUBOS DE VENTILAÇÃO DEVERÃO PASSAR 30CM ACIMA DO TELHADO.
- 6 - UTILIZAR DISPOSITIVO ANTI-ESPUMA NA CAIXA SIFONADA DA ÁREA DE SERVIÇO.
- 7 - TODAS AS TUBULAÇÕES EXPOSTAS DEVERÃO SER FIXADAS COM BRACADEIRA.
- 9 - A BASE DO RESERVATÓRIO DEVERÁ TER UMA SUPERFÍCIE LISA, NIVELADA E ISENTA DE SUEIRA OU MATERIAIS PONTAGUDOS. A BASE DEVE TER RESISTÊNCIA COMPATIVEL COM O PESO DA CAIXA CHEIA E DEVE SER MAIOR DO QUE A LARGURA DO FUNDO DA CAIXA.

Lista de Materiais - Conexões e Acessórios - Completa

Descrição do Material	Quantidade (peças)
	6
Anel de Borracha, DN100mm, para linha de PVC Rígido Branco Série Normal, conforme NBR 5688	16
Joelho 90°, DN100mm, de PVC Rígido Branco Série Normal, conforme NBR 5688	8
Luva Simples, DN100mm, de PVC Rígido Branco Série Normal, conforme NBR 5688	8
Produto Inexistente	2

Lista de Materiais - Tubos

Descrição do Material	Diâmetro Nominal (mm)	Comprimento (m)	Referência de Fabricante
Tubo de PVC Rígido Branco, conforme NBR5688, Linha Série Normal	Ø100	82,17	Tigre



PENN & WIZE
INSTALAÇÕES PREDIAIS
<https://pennwize.github.io/>



PROJETO: Edifício Derry and Georgie

LOCAL: Rua dos bobos, nº 0. Natal/RN - Brasil

ASSUNTO: Folha - Churrasqueira

AUTORES DO PROJETO:
Amanda João Pedro Melo e Letícia Tórres

FOLHA:


P06

REV.:


1 : 50

DATA:

10/02/26

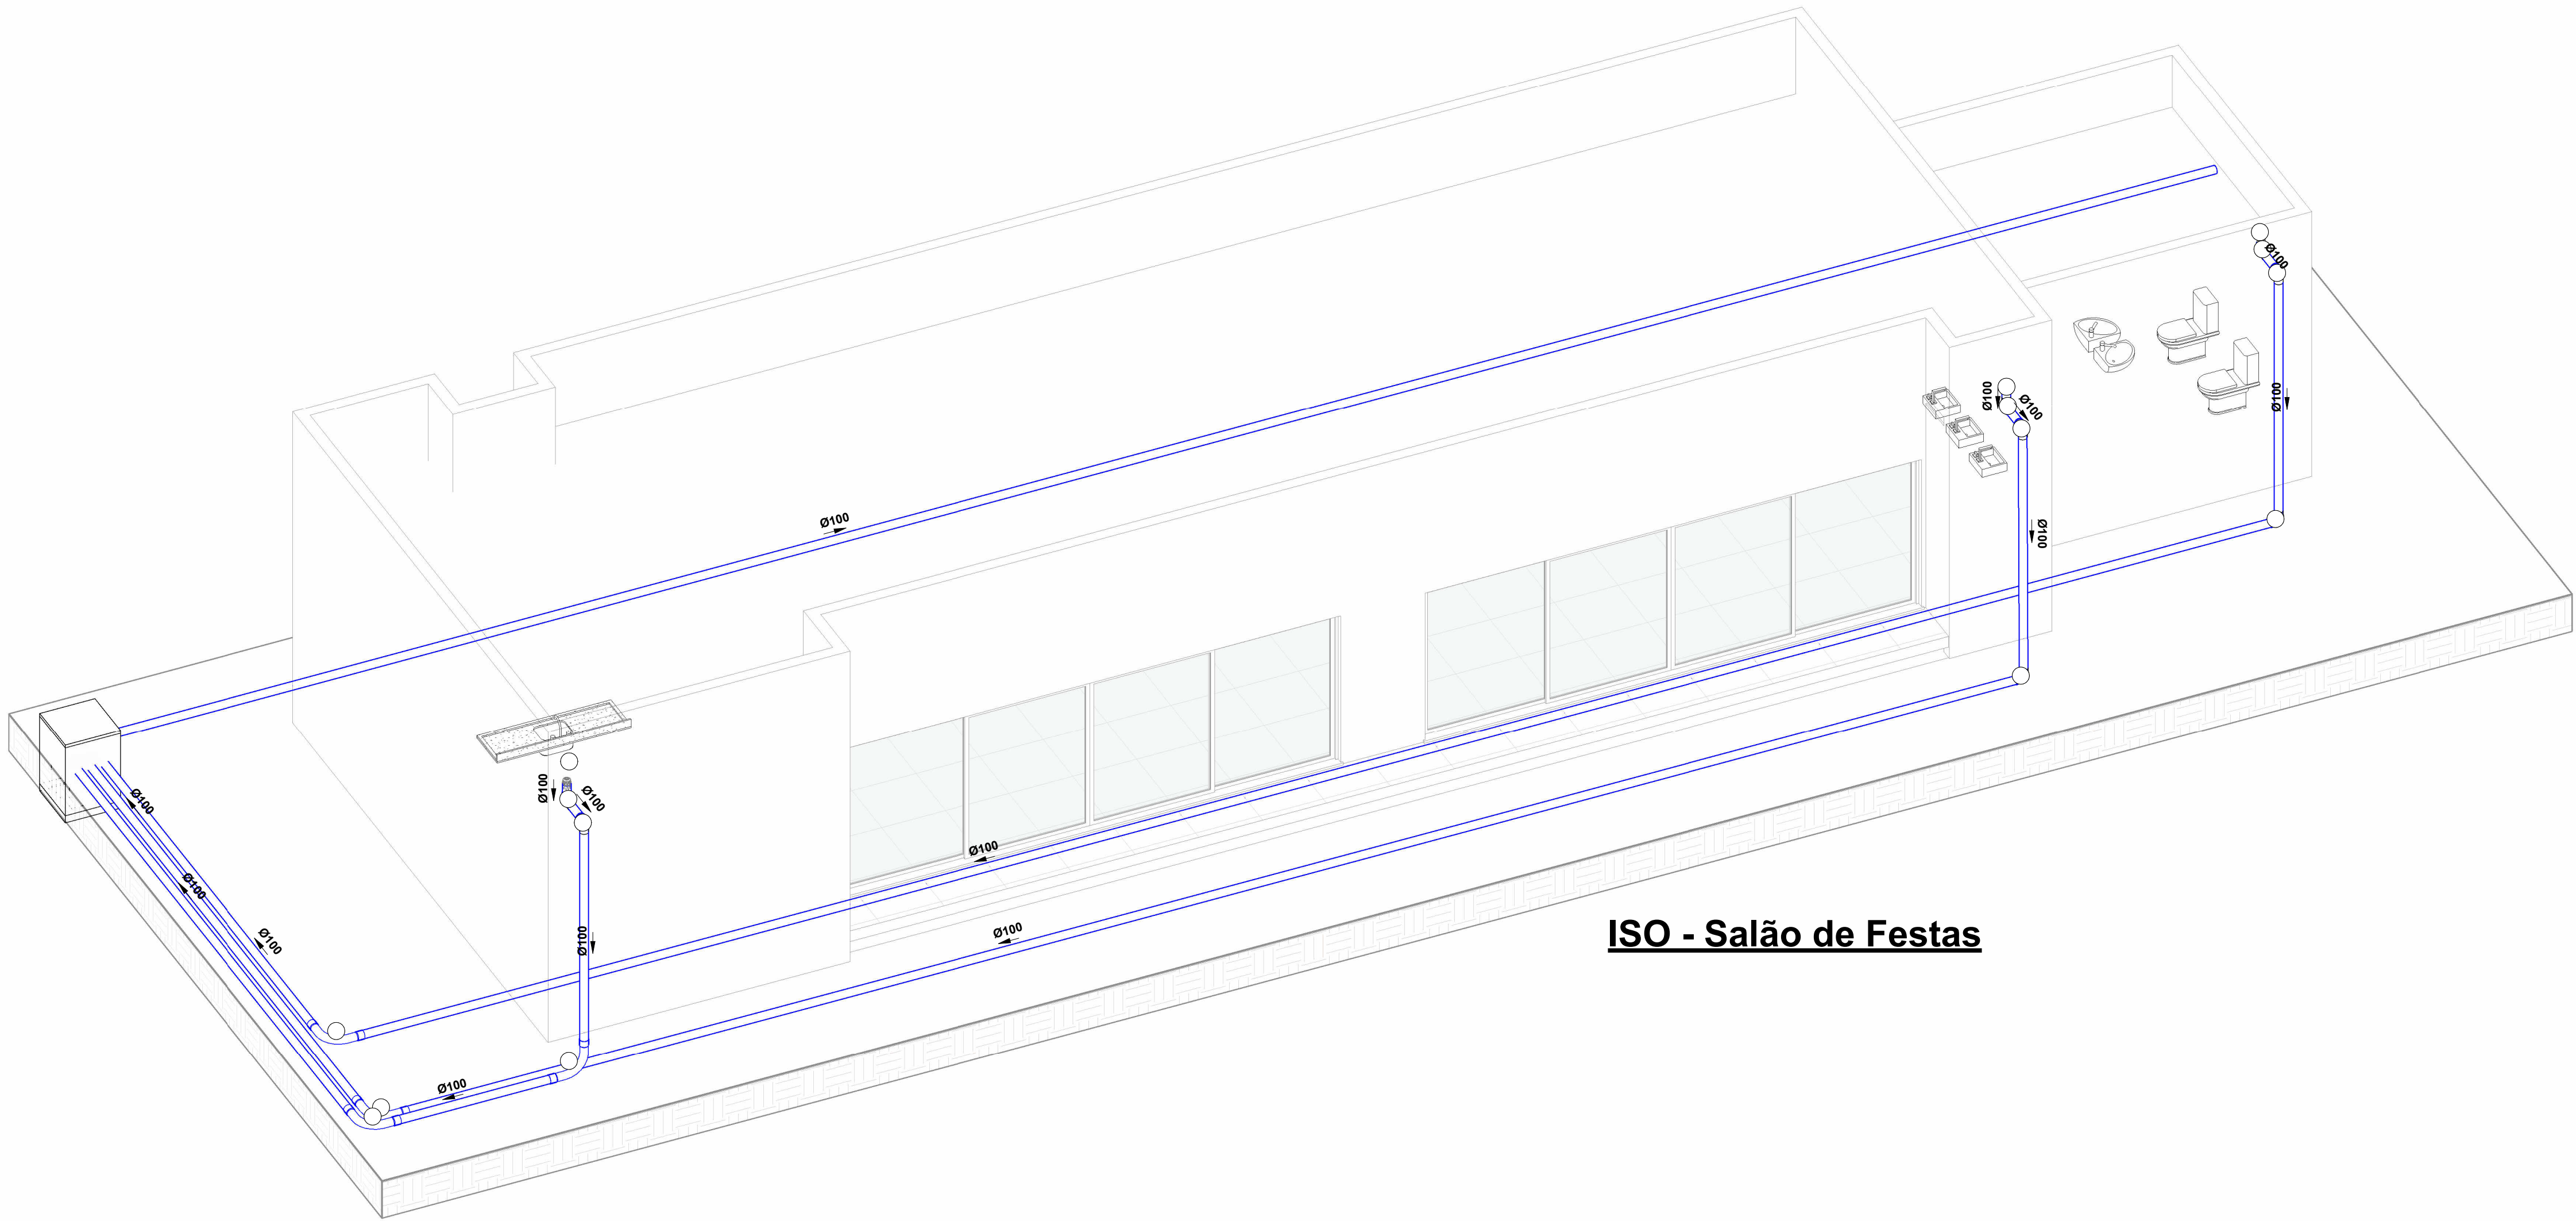

ISO - Salão de Festas

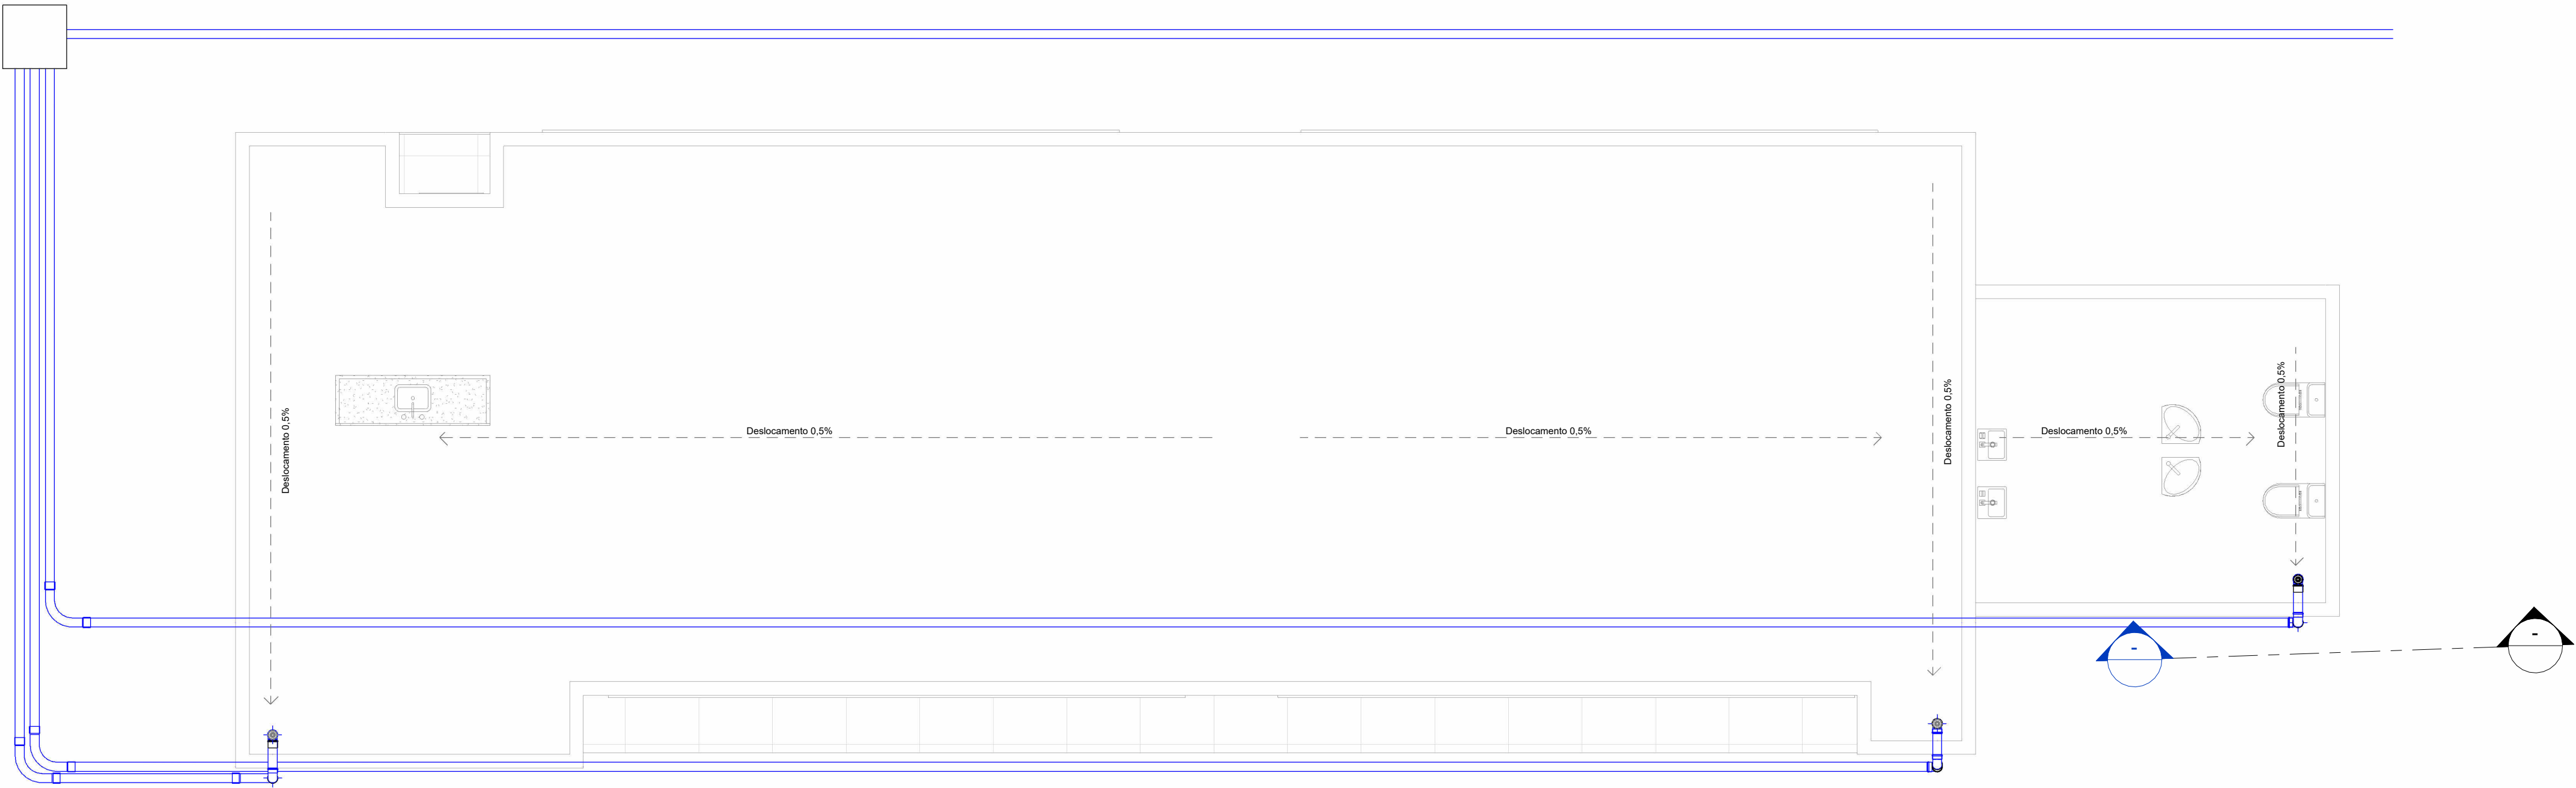

Salão de Festas

1 : 50

LEGENDA:

- TUBULAÇÃO PVC BRANCO SN - ESGOTO PRIMÁRIO
- TUBULAÇÃO PVC BRANCO SN - ESGOTO SECUNDÁRIO
- TUBO DE QUEDA DE ESGOTO PRIMÁRIO

ABREVIações:

RS - RALO SECO

NOTAS:

- DIMENSÕES E DIÂMETROS EM MILÍMETROS, EXCETO ONDE INDICADO CONTRÁRIO.
- NOS TRECHOS HORIZONTAIS DAS TUBULAÇÕES DE ESGOTO SANITÁRIO RECOMENDAM-SE AS SEGUINTEs DECLIVIDADES MÍNIMAS:
 - 2% PARA TUBULAÇÕES COM DIÂMETRO NOMINAL IGUAL OU INFERIOR A 75mm;
 - 1% PARA TUBULAÇÕES COM DIÂMETRO NOMINAL IGUAL OU SUPERIOR A 100mm;
- UTILIZAR ANÉIS DE BORRACHA NAS CONEXÕES DE ESGOTO.
- PROIBIDO UTILIZAR FOGO NAS TUBULAÇÕES.
- OS TERMINAIS DE VENTILAÇÃO DOS TUBOS DE VENTILAÇÃO DEVERÃO PASSAR 30CM ACIMA DO TELHADO.
- UTILIZAR DISPOSITIVO ANTI-ESPUMA NA CAIXA SIFONADA DA ÁREA DE SERVIÇO.
- TODAS AS TUBULAÇÕES EXPOSTAS DEVERÃO SER FIXADAS COM BRACADEIRA.
- A BASE DO RESERVATÓRIO DEVERÁ TER UMA SUPERFÍCIE LISA, NIVELADA E ISENTA DE SUJEIRA OU MATERIAIS PONTAGUDOS. A BASE DEVE TER RESISTÊNCIA COMPATIVEL COM O PESO DA CAIXA CHEIA E DEVE SER MAIOR DO QUE A LARGURA DO FUNDO DA CAIXA.

Lista de Materiais - Conexões e Acessórios - Completa

Descrição do Material	Quantidade (peças)
	9
Anel de Borracha, DN100mm, para linha de PVC Rígido Branco Série Normal, conforme NBR 5688	16
Joelho 90°, DN100mm, de PVC Rígido Branco Série Normal, conforme NBR 5688	8
Luva Simples, DN100mm, de PVC Rígido Branco Série Normal, conforme NBR 5688	8
Produto Inexistente	4

Lista de Materiais - Tubos

Descrição do Material	Diâmetro Nominal (mm)	Comprimento (m)	Referência de Fabricante
Tubo de PVC Rígido Branco, conforme NBR5688, Linha Série Normal	Ø100	127,57	Tigre



PENN & WIZE
INSTALAÇÕES PREDIAIS
<https://pennwize.github.io/>



PROJETO: Edifício Derry and Georgie

LOCAL: Rua dos bobos, nº 0. Natal/RN - Brasil

ASSUNTO: Folha - Salão de Festas

AUTORES DO PROJETO:
Amanda João Pedro Melo e Letícia Tórres

FOLHA:

P07

REV.:

ESCALA:

1 : 50

DATA:

10/02/26

LEGENDA:

- TUBULAÇÃO PVC BRANCO SN - ESGOTO PRIMÁRIO
- TUBULAÇÃO PVC BRANCO SN - ESGOTO SECUNDÁRIO
- TQ-nn

Øxx

-TUBO DE QUEDA DE ESGOTO PRIMÁRIO

nn: número da coluna

xx: diâmetro nominal da coluna

ABREVIações:

RS - RALO SECO

NOTAS:

- 1 - DIMENSÕES E DIÂMETROS EM MILÍMETROS, EXCETO ONDE INDICADO CONTRÁRIO.
- 2 - NOS TRECHOS HORIZONTAIS DAS TUBULAÇÕES DE ESGOTO SANITÁRIO RECOMENDAM-SE AS SEGUINTEs DECLIVIDADES MINIMAS:

-2% PARA TUBULAÇÕES COM DIÂMETRO NOMINAL IGUAL OU INFERIOR A 75mm;


-1% PARA TUBULAÇÕES COM DIÂMETRO NOMINAL IGUAL OU SUPERIOR A 100mm;
- 3 - UTILIZAR ANEIS DE BORRACHA NAS CONEXÕES DE ESGOTO.
- 4 - PROIBIDO UTILIZAR FOGO NAS TUBULAÇÕES.
- 5 - OS TERMINAIS DE VENTILAÇÃO DOS TUBOS DE VENTILAÇÃO DEVERÃO PASSAR 30CM ACIMA DO TELHADO.
- 6 - UTILIZAR DISPOSITIVO ANTI-ESPUMA NA CAIXA SIFONADA DA ÁREA DE SERVIÇO.
- 7 - TODAS AS TUBULAÇÕES EXPOSTAS DEVERÃO SER FIXADAS COM BRACADEIRA
- 9 - A BASE DO RESERVATÓRIO DEVERÁ TER UMA SUPERFÍCIE LISA, NIVELADA E ISENTA DE SUEIRA OU MATERIAIS PONTIAGUDOS. A BASE DEVE TER RESISTÊNCIA COMPATIVEL COM O PESO DA CAIXA CHEIA E DEVE SER MAIOR DO QUE A LARGURA DO FUNDO DA CAIXA.

Lista de Materiais - Conexões e Acessórios - Completa

Descrição do Material	Quantidade (peças)
	4
Anel de Borracha, DN100mm, para linha de PVC Rígido Branco Série Normal, conforme NBR 5688	1
Anel de Concreto perfurado, pré moldado, para Sumidouro, Ø Externo 1500mm, Altura 500mm	6
Brita N°4	1
Joelho 90°, DN100mm, de PVC Rígido Branco Série Normal, conforme NBR 5688	1
Laje para fossa, filtro anaeróbio e Sumidouro, Ø Externo 1500mm	1
Tampa, para fossa, filtro Anaeróbio e Sumidouro, Ø600mm	1

Lista de Materiais - Tubos

Descrição do Material	Diâmetro Nominal (mm)	Comprimento (m)	Referência de Fabricante
Tubo de PVC Rígido Branco, conforme NBR5688, Linha Série Normal	Ø100	42,29	Tigre

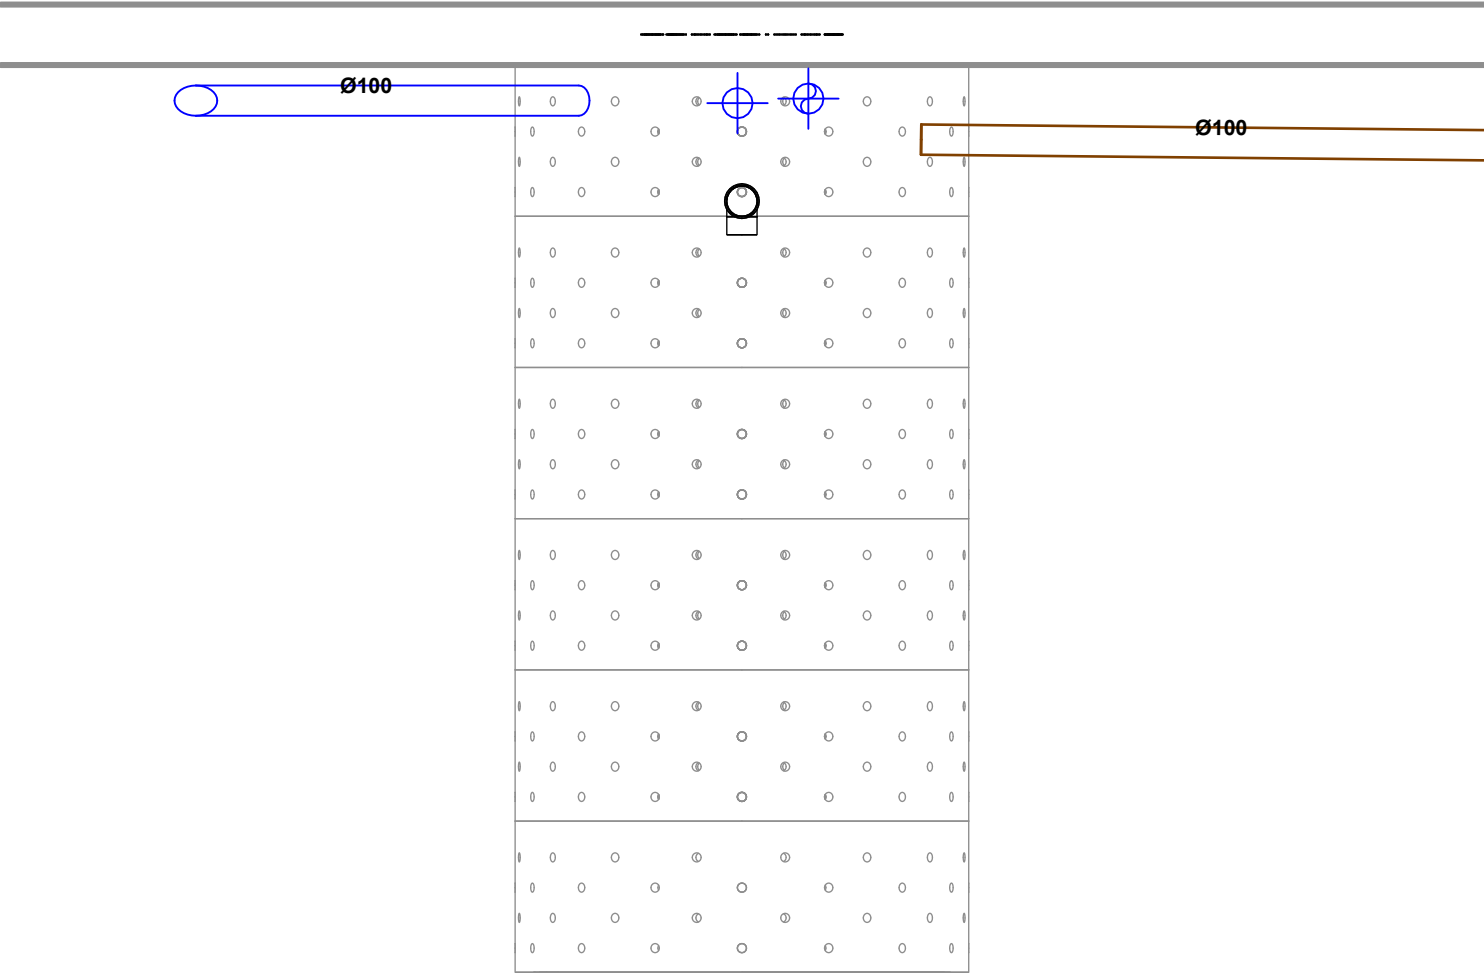

Elevação Sumidouro

1 : 25



PENN & WIZE
INSTALAÇÕES PREDIAIS
<https://pennwize.github.io/>



PROJETO:	Edifício Derry and Georgie	FOLHA:	P08
LOCAL:	Rua dos bobos, nº 0. Natal/RN - Brasil	REV.:	
ASSUNTO:	Folha - Caixa de Areia e Poços Absorventes	ESCALA:	Como indicada
AUTORES DO PROJETO:	Amanda João Pedro Melo e Letícia Tórres	DATA:	10/02/26